

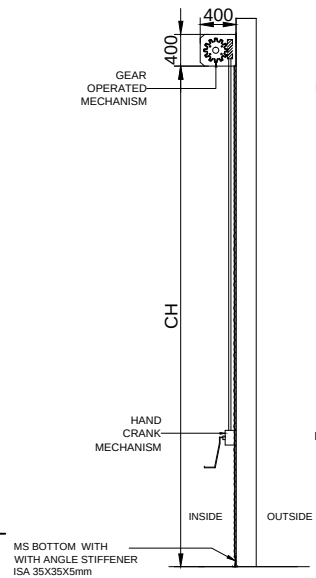



SIDE VIEW

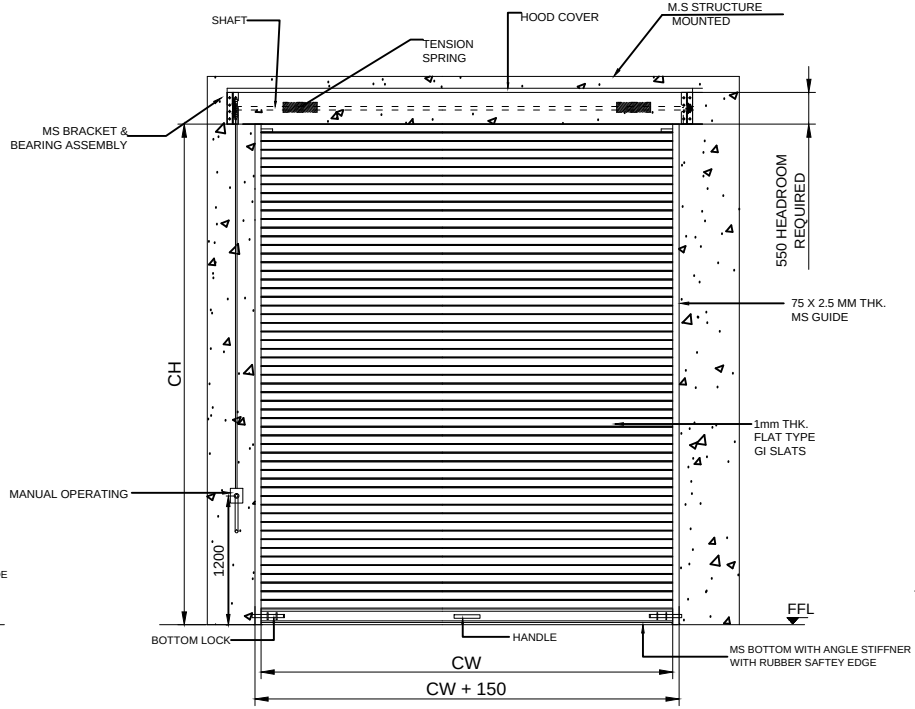


INSIDE ELEVATION

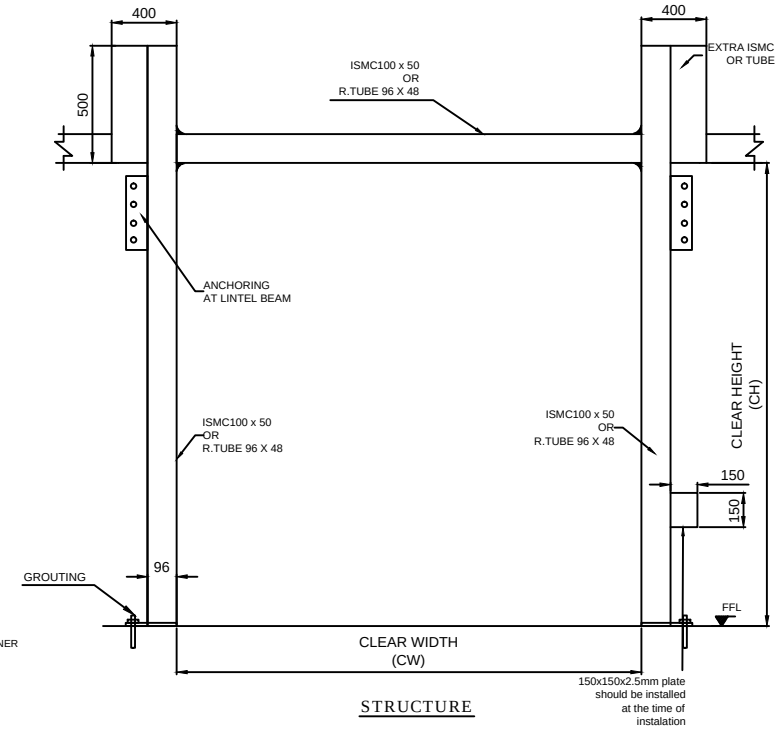


STRUCTURE

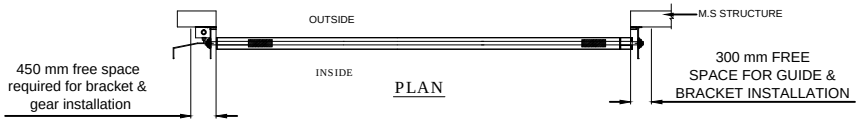

PLAN

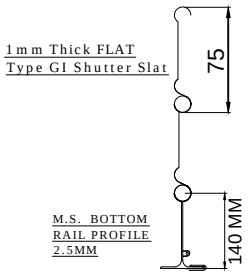

M.S. BOTTOM RAIL PROFILE 2.5MM

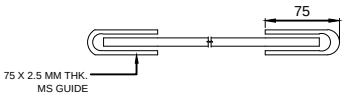

RAL : 9010

TOLERANCE - ±10mm

REV NO	DATE	DRAWN	REMARK
			2.CLEAR HEIGHT INCREASE
R01	20.07.20	P.A	1.STRUCTURE DETAIL ADDED

This drawing & design is the property of NIHVA TECHNOLOGIES. Not to be sold or copied to any other concern.

TITLE
GEAR OPERATED ROLLING SHUTTER

NIHVA TECHNOLOGIES PVT. LTD.

NIHVA TECHNOLOGIES PVT. LTD. PUNE
Tel : 020 66304033
Email:- info@nihva.com
Website:- www.nihva.com

	NAME	SIGN	DATE
DRAWN	P.A		04.06.2020
CHECK	G.J		04.06.2020
APPRD.			

CLIENT - SYNERGY
PROJECT-EMBASSY INDUSTRIAL PARKS PVT. LTD
SITE LOCATION - CHAKAN
If any queries contact : design@nihva.com
DWG. NO. : NIHVA/20-21/0013/R01
REV- R01
ALL DIMENSION ARE IN mm
SCALE: NTS
WT:
SHEET: 01 OF 01

SR NO	(CW) CLEAR WIDTH	(CH) CLEAR HEIGHT	QUANTITY
1	2500	2900	01 NO

NOTE-
1. ALL CIVIL WORK WILL BE CLIENT'S SCOPE.
2.M.S STRUCTURE REQUIRED FOR SHUTTER IS IN CLIENT'S SCOPE.