

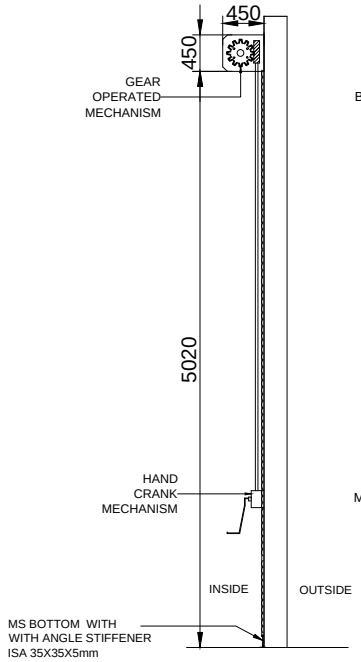



SIDE VIEW

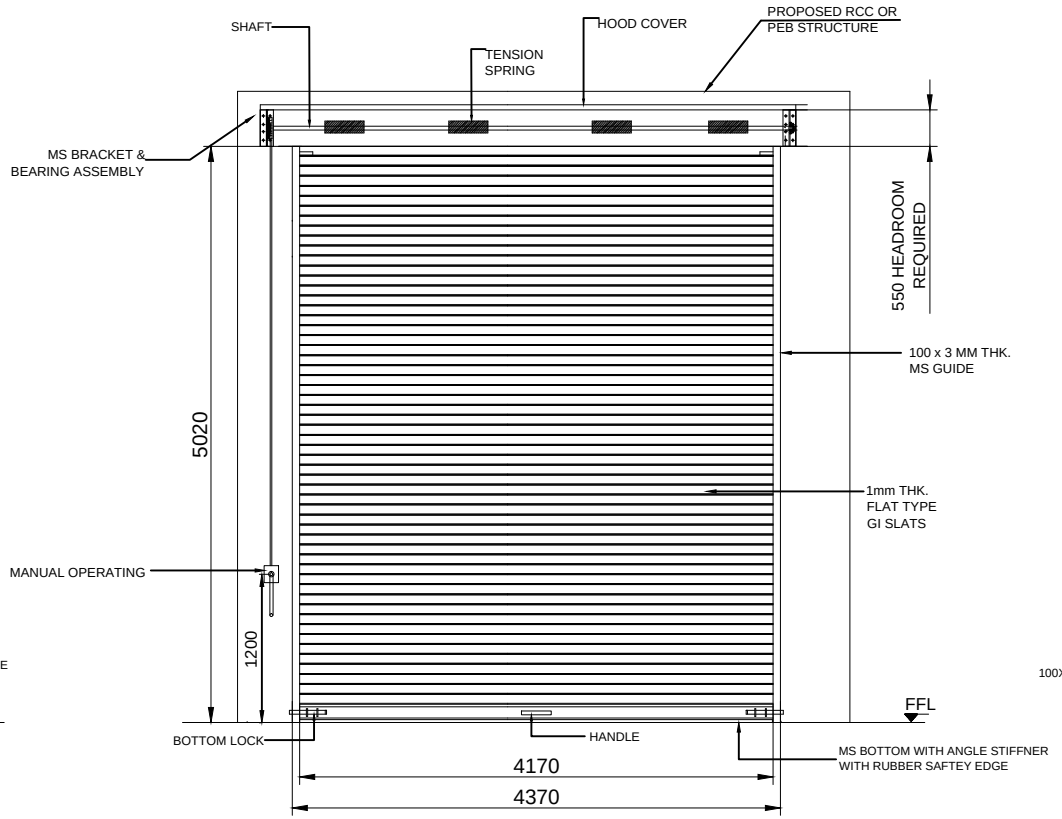


INSIDE ELEVATION

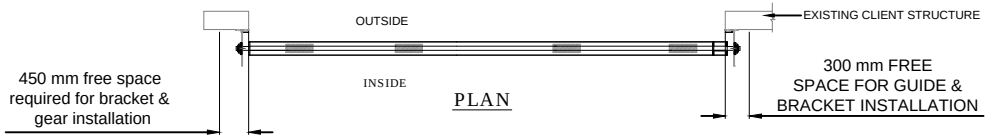

PLAN

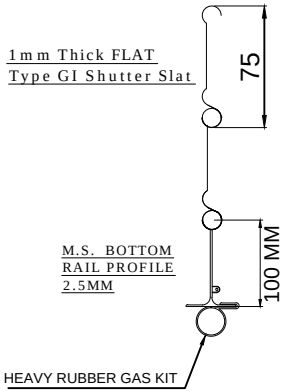

M.S. BOTTOM RAIL PROFILE 2.5MM

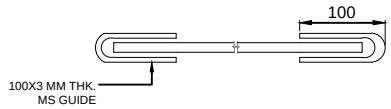

SR.NO.	RAL COLOR	
01	RAL 9002 (WHITE GREY)	OUTSIDE
02	RAL 7040 (WINDOW GREY)	INSIDE

SR.NO.	SIZE	QUANTITY
01	4170(W)X5020(H)	08

S.NO	FEATURE	EQUIPMENT DETAILS
01	SLATS MODEL	GALVANISE STEEL(GI) SLATS 1mm THK.
02	GUIDE RAIL	100 X 3mm THK MILD STEEL(MS).
03	BOTTOM RAIL	2.5mm THK MILD STEEL (M.S.).
04	HOOD COVER	0.9mm THK GALVANISE STEEL (GI).
05	RAL COLOR	RAL 9002 (OUTSIDE OF SHUTTER) RAL 7040 (INSIDE OF SHUTTER)

NOTE-
1. ALL CIVIL WORK WILL BE CLIENT'S SCOPE.

TOLERANCE - ±10mm

This drawing & design is the property of NIHVA TECHNOLOGIES. Not to be sold or copied to any other concern.

TITLE
GEAR OPERATED ROLLING SHUTTER 4mX5m(FLAT PROFILE

	NAME	SIGN	DATE
DRAWN	PRADEEP		14-07-2018
CHECK	R.D		14-07-2018
APPRD.	V.T		14-07-2018

NIHVA TECHNOLOGIES PVT. LTD.
NIHVA TECHNOLOGIES PVT. LTD, PUNE
Tel : 020 66304033
Email:- info@nihva.com
Website:- www.nihva.com

CLIENT -
PROJECT-
SITE LOCATION -
If any queries contact : design@nihva.com
DWG. NO. : NIHVA/18-19/VDR/067
REV- 00
ALL DIMENSION ARE IN mm
SCALE: NTS
WT:
SHEET: 01 OF 01