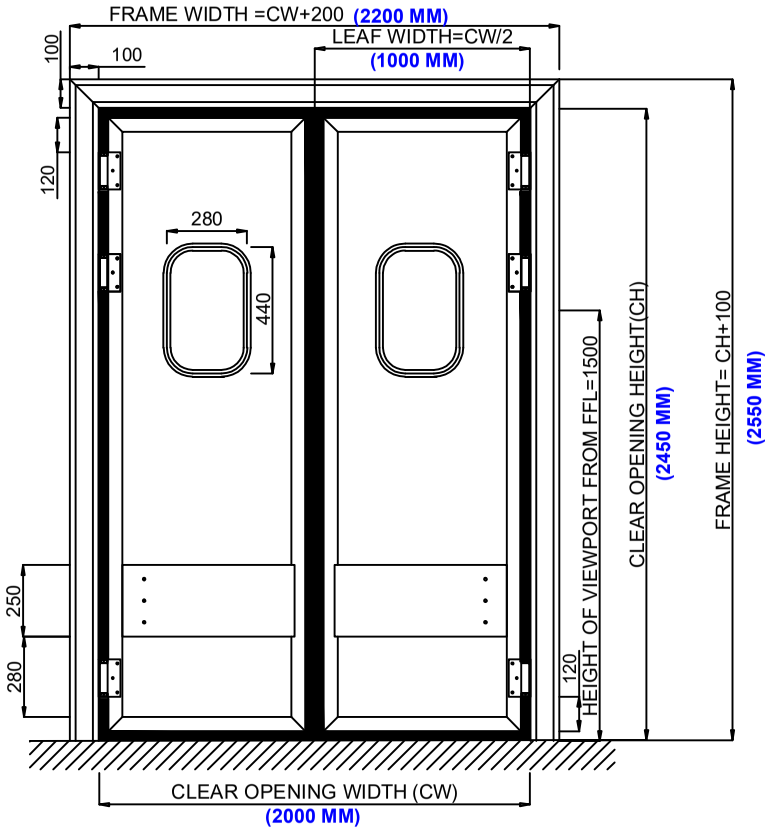
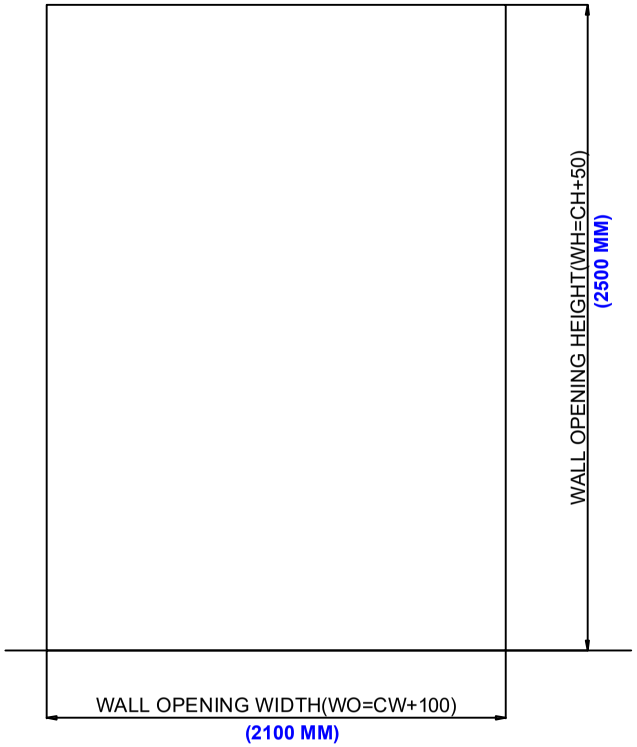
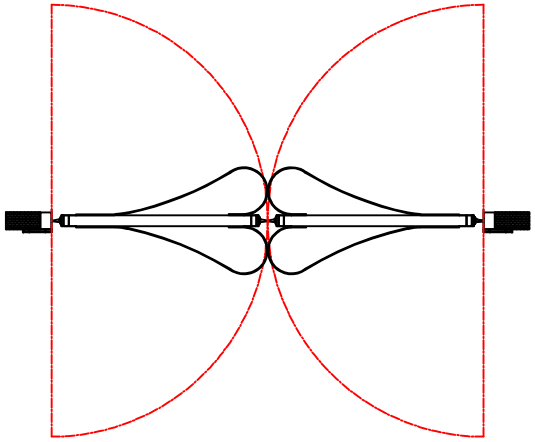


Note:
1.All dimension are in mm
2.All Civil work will be in client scope

| |
|---|
| LEAF FINISH : PE / PCGI |
| LEAF THICKNESS : 40 MM |
| HINGES MOC : DOUBLE ACTION STAINLESS STEEL |
| VIEW WINDOW : 1 UNIT ON EACH LEAF |
| VIEW WINDOW HEIGHT : 440 MM |
| VIEW WINDOW WIDTH : 280 MM |
| VIEW WINDOW POSITION FROM FFL : 1500 MM |

This drawing & design is the property of NIHVA TECHNOLOGIES. Not to be sold or copied to any other concern.

TITLE:- NIHVA Make NFF3 Flip Flap Door

NIHVA TECHNOLOGIES PVT. LTD.

NIHVA TECHNOLOGIES PVT. LTD. PUNE
Tel : 020 66304033
Email:- info@nihva.com
Website:- www.nihva.com

| | NAME | DATE | SIGN |
|---|---|---|---|
| DRAWN | SUJATA | 22-03-2022 | |
| CHECK | G.P | 22-03-2022 | |
| APPRD. | P.J | 22-03-2022 | |

If any queries contact : design@nihva.com

ALL DIMENSION ARE IN mm

CLIENT - RBCC
LOCATION - PUNE
PRODUCT - FLIP FLAP DOOR
DWG NO:-NIHVA/21-22/CLT/0372 | REV- 0
SCALE: NTS | SCALE:-- 1:1 | SHEET: 01 OF 01

| Rev No. | Revision | Date | Revised By |
|---|---|---|---|
| | | | |