
THIS PRINT IS THE PROPERTY OF NIHVA IT IS TO BE USED ONLY FOR THE PURPOSE FOR WHICH IT WAS LENT AND MUST NOT BE USED IN ANY WAY DERTIMENTAL TO THE INTEREST OF THIS COMPANY AND IS SUBJECT TO RETURN ON DEMAND.

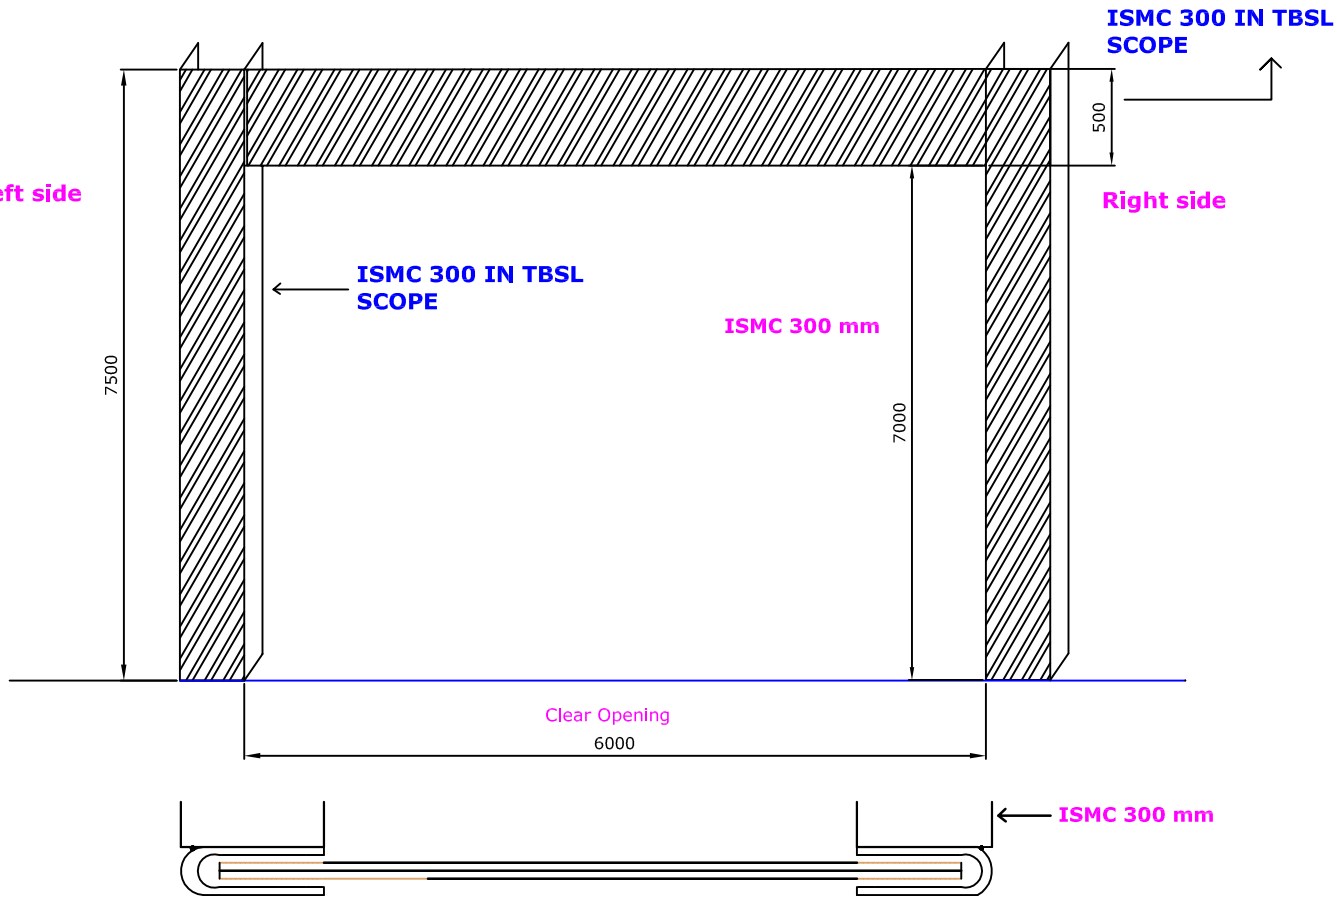

SIZE :- (W)6.0M X (H)7.0M

TITLE: MOUNTING STRUCTURE FOR MOTORISED ROLLING SHUTTER		NIHVA TECHNOLOGIES PVT. LTD. Pune-411044 Tel : 020 66304033 , Email:info@nihva.com
CLIENTS APPROVEL:–	DRAWN A.K	CLIENT: SHAPOOR JI PALLON JI
	CHECK V.T	PROJECT / SITE: GE / CHAKAN
	ENG	PRODUCT NAME: MOTORISED ROLLING SHUTTER
	APPRD.	
ALL DIMENSION ARE IN M.M.	PROD	
If any querles CONTACT: projects@nihva.com	MFG	DWG. NO.:– NVA/SP-GE/642/3-3
	Ref. No.	SCALE: NTS SHEET: 1 OF 1