

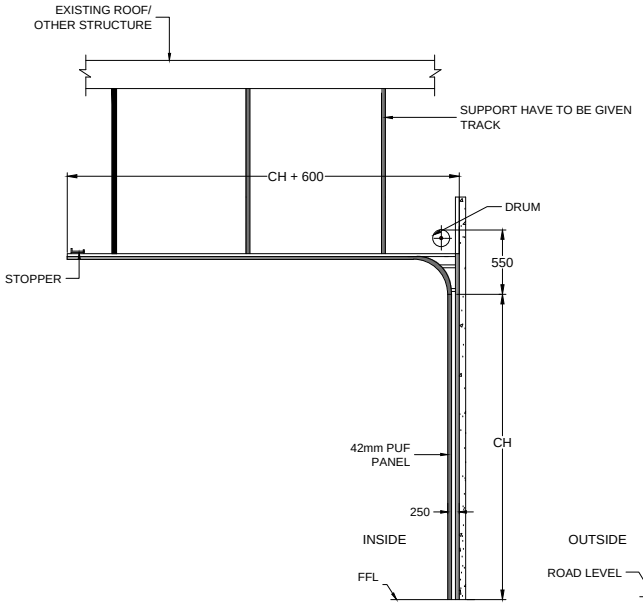



SIDE VIEW

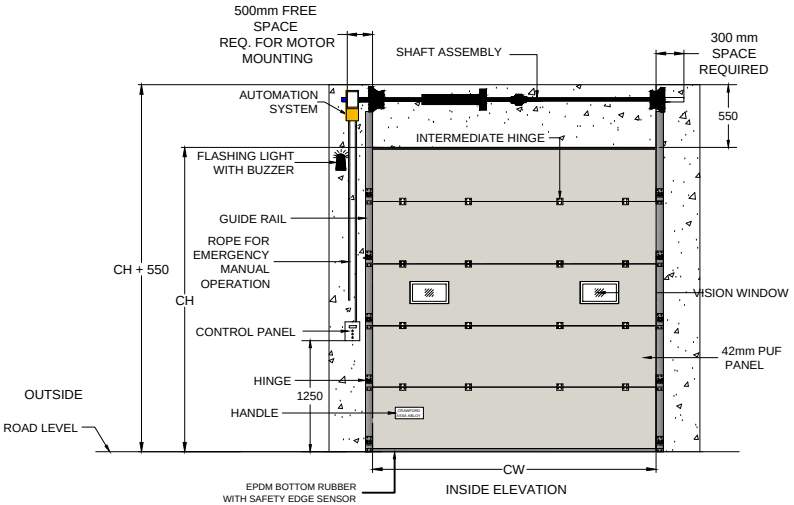

INSIDE ELEVATION

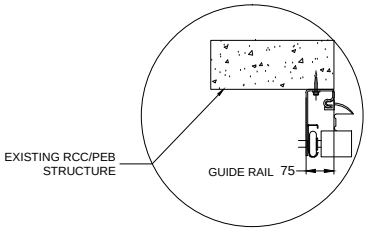

TRACK DETAILS

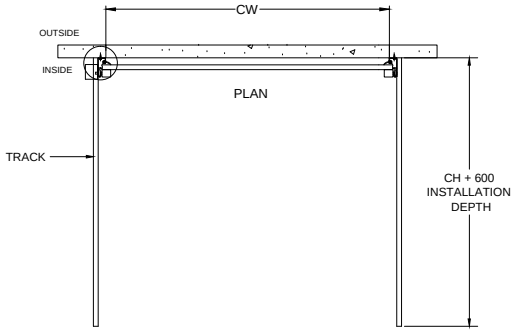

Power supply- Single phase 230V,50Hz
UPS capacity- 2KVA/Door

Color for Door panel will be RAL 7035 Light Grey.

CLEAR WIDTH (CW)	CLEAR HEIGHT (CH)	QUANTITY
2500 mm	4000 mm	01
4000 mm	4000 mm	08

TECHNICAL DATA :

COMPONENTS	MATERIALS	SPECIFICATIONS
DOOR PANELS	GI & PUF	42mm CFC- FREE POLYURETHANE WITH 0.5mm THK, GI PRECOATED PANELS.
DOOR HINGE	——	HEAVY DUTY HINGES FOR INTERLOCKING OF PANELS
SHAFT ASSEMBLY	STD.	TORSIONAL SPRING WITH SHAFT & BEARING PLATES
FINISH		PANELS WILL BE COLORED IN STANDARD RAL SHADE 9002 GRAY WHITE BY CLIENT

ACCESSORIES-
1. SAFETY EDGE SENSOR. 2. FLASHING LIGHT 3.SAFETY PHOTOCELL
4. MANUAL ROPE 5. EMERGENCY STOP FROM OUTSIDE
6. SPRING BREAK DEVICE(SPRING FAILURE PROTECTION)
7.TWO WINDOWS 8.ANY POINT STOP(DEADMAN CONTROL)

IMPORTANT NOTES:
1. REQUIRED STRUCTURE FOR DOOR SHALL BE IN CLIENT'S SCOPE.
2.SINGLE PHASE POWER SUPPLY REQUIRED AT DOOR LOCATION.
3.ALL CIVIL WORK SHALL BE CLIENT'S SCOPE.

NIHVA TECHNOLOGIES PVT. LTD. PUNE
Email:- info@nihva.com
Website:- www.nihva.com

TITLE:

SECTIONAL DOOR SL (MOTORIZED)

CLIENT'S APPROVAL :

CLIENT - Endress + Hauser Flowtec (India) Pvt. Ltd.

PROJECT - Endress + Hauser Flowtec (India) Pvt. Ltd.

SITE LOCATION - AURANGABAD

DWG. NO. : NIHVA/19-20/0223 | REV- 0

SCALE: NTS | WT: | SHEET:1 OF 1

	NAME	DATE	SIGN
DRAWN	P.A	27.02.2020	
CHECK	G.J	27.02.2020	
APPROVAL			

If any queries contact : design@nihva.com

NOTE: ALL DIMENSIONS ARE IN mm

THIS DRAWING & DESIGNING IS THE PROPERTY OF NIHVA TECHNOLOGIES. NOT TO BE SOLD OR COPIED TO ANY OTHER CONCERN.