

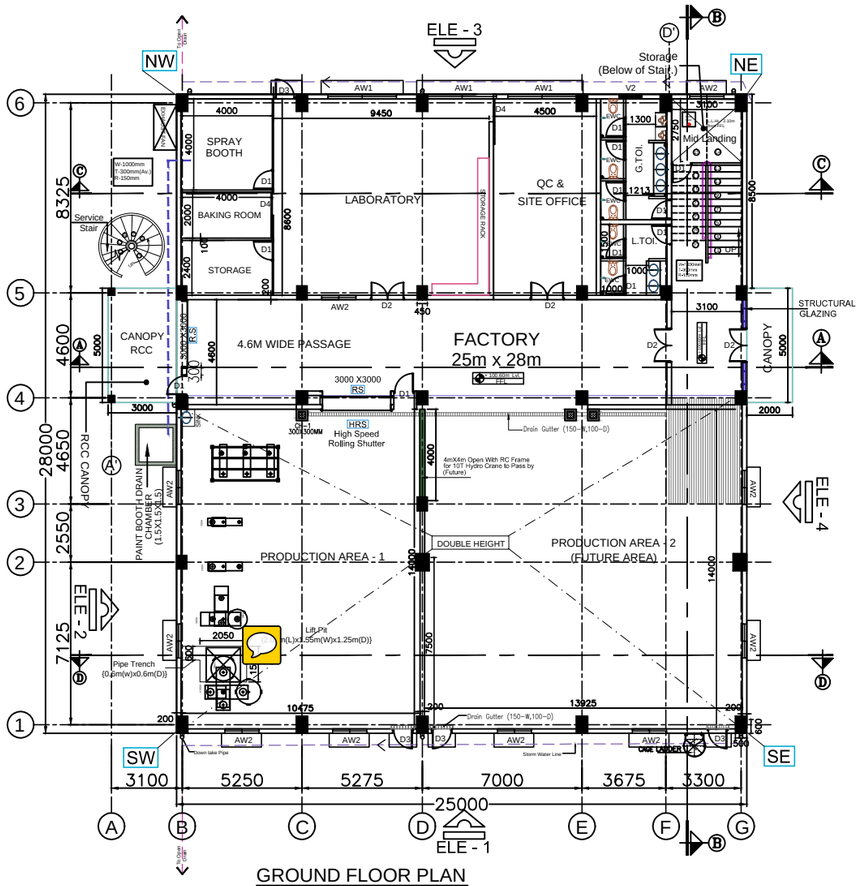


GROUND FLOOR PLAN

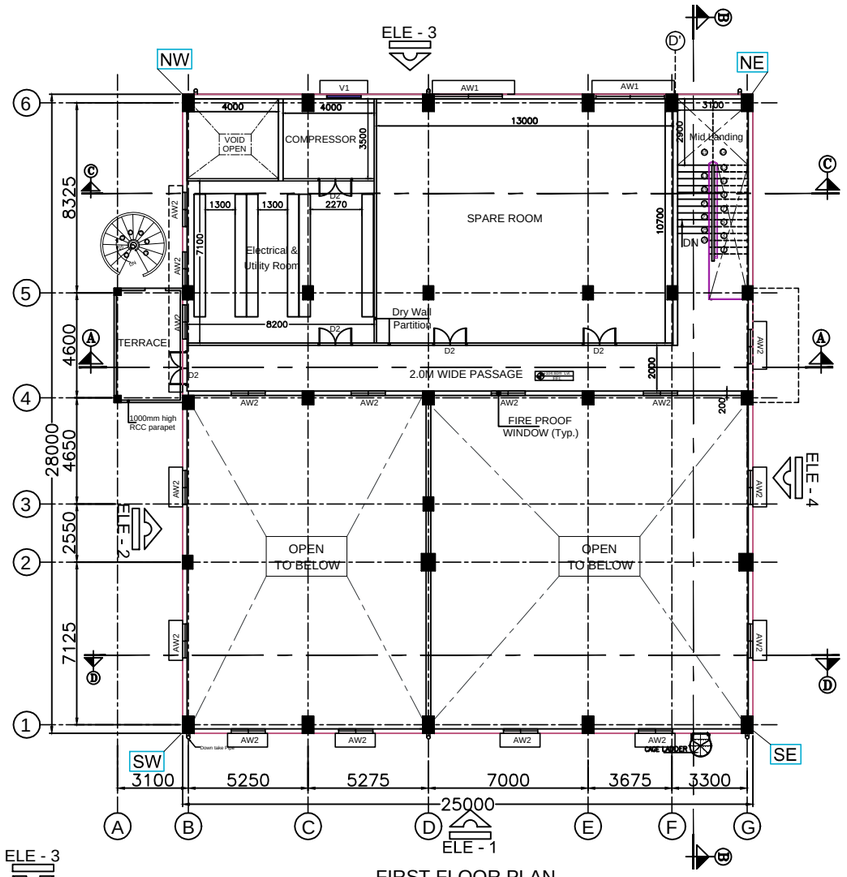


FIRST FLOOR PLAN

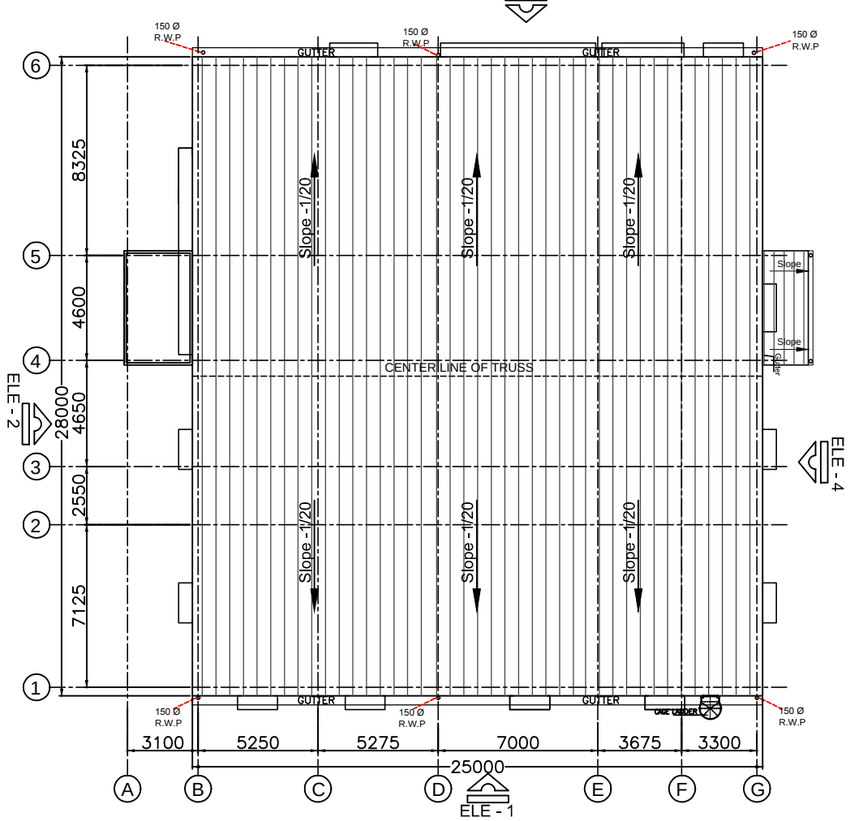

FACTORY ROOF PLAN

KEY PLAN :-

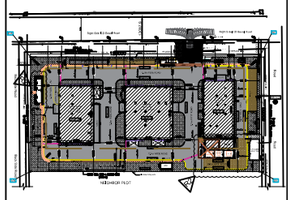

LEGEND :-

BLOCK WALL

COLUMN & R.C WALL

FFL+ 0.10m Lvl.

GENERAL NOTES :

* ALL DIMENSIONS ARE IN MILLIMETRES AND ARE UNFINISHED DIMENSIONS UNLESS OTHERWISE SPECIFIED.
* ALL LEVELS ARE IN METRES AND ARE UNFINISHED LEVELS UNLESS OTHERWISE SPECIFIED.
* DO NOT SCALE DRAWINGS. ONLY WRITTEN DIMENSIONS SHALL BE FOLLOWED. ANY DISCREPANCIES NOTED SHALL BE BROUGHT TO THE NOTICE OF THE ARCHITECT PRIOR TO EXECUTION.

SCHEDULE OF JOINERY

TYPE	DESCRIPTION	SIZE
RS	ROLLING SHUTTER	3000 x 3000
D1	DOOR	900 x 2400
D2	DOOR	1500 x 2400
D3	DOOR	1000 x 2400
D4	SLIDING DOOR	1000 x 2400
AW1	ALUMINUM WINDOW	3000 x 1500
AW2	ALUMINUM WINDOW	1500 x 1500
V1	ALUMINUM LOUVERED WINDOW	1500 x 1500
V2	ALUMINUM LOUVERED WINDOW	1000 x 400

REV.	DESCRIPTION	DATE	BY	CHD.
R1	ISSUED FOR APPROVAL / CONTRACT	20170601	B.G	F.IT

AMENDMENT

GRAPHIC SCALE: 0 0.5M 2M 4M / 0.5M 0 1M 3M 5M

CLIENT:

FUJIKURA KASEI COATING INDIA PVT. LTD.

PROJECT:

FUJIKURA KASEI COATING INDIA BAWAL NEW FACTORY
PHASE -3, SECTOR-9, PLOT NO. 201, 202, 225 & 226
IMT-BAWAL, SECTOR 9, HARYANA, INDIA.

DRAWING TITLE:

FACTORY - FLOOR & ROOF PLAN

DESIGN & BUILD BY:

FUJITA

M/S. FUJITA CORPORATION
(PROJECT OFFICE)
Door No.3, First Floor, 3rd Street, KAMARAJ NAGAR,
THIRUVANMIYUR, CHENNAI - 600 041.

SCALE : 1 : 100	DRAWN : B.G	REV	
DATE : 20170420	CHKD : F.IT		
DRAWING NO: A-006		R1	