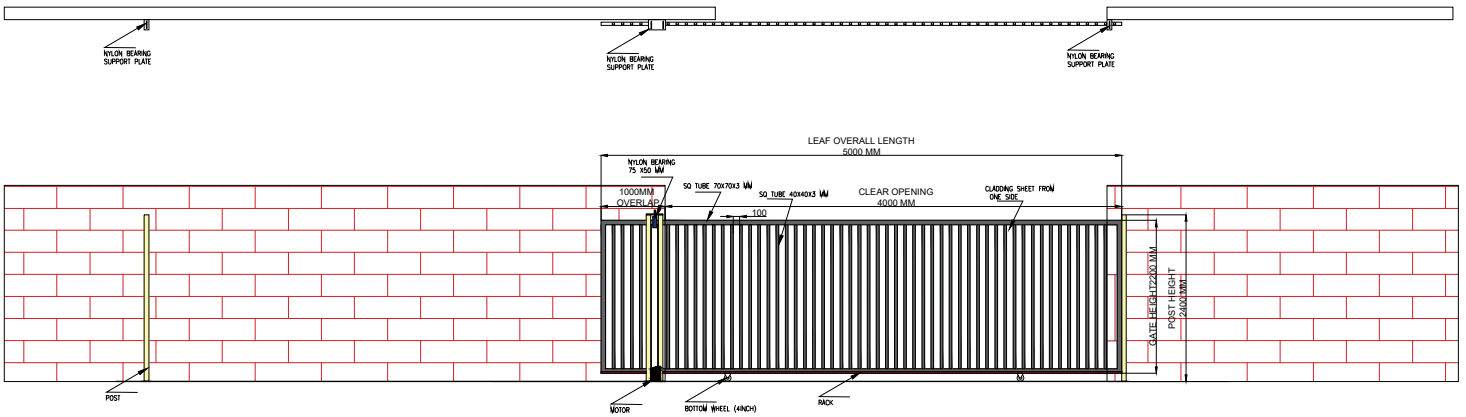


TECHNICAL SPECIFICATION:-

SR.	SPECIFICATION	DETAILS
1.	DOOR TYPE	MOTORIZED SINGLE LEAF SLIDING LEAF
2.	MOUNTING LOCATION AREA	INSIDE AREA
3.	OUTER FRAME & POST	SQ TUBE 70X70X3 MM
4.	INNEAR TUBE	SQ TUBE 40X40X3 MM
5.	BOTTOM RAIL ON GROUND	DIA 20 MM EN 8 BRIGHT BAR & ISMB -100X50 MM
6.	BOTTOM WHEEL	HEAVY DUTY WHEEL 4 INCH
7.	GUIDE ROLLER	NYLON ROLLERS-75X 50 MM
8.	COLOUR	
9.	OPERATING SWITCH	PUSH BUTTON FROM INSIDE

GATE SIZES :-

SR.	CLEAR OPENING	CLEAR HEIGHT	QTY.
01	4000 mm	2200 mm	01

This drawing & design is the property of NIHVA TECHNOLOGIES. Not to be sold or copied to any other concern.

TITLE: SLIDING GATES

	NAME	SIGN	DATE
DRAWN	B.S		15.04.2026
CHECK	V.T		15.04.2026
APPRD.	V.T		15.04.2026

If any queries contact : design2@nihva.com

ALL DIMENSION ARE IN mm

NIHVA TECHNOLOGIES PVT. LTD.
NIHVA TECHNOLOGIES PVT. LTD. PUNE
Tel : 020 66304033
Email:- info@nihva.com
Website:- www.nihva.com

CLIENT - CG POWER

PRODUCT - SLIDING GATES

FORMAT NO - NIHVA-DD-F-03

DWG. NO. : NIHVA/26-27 | REV- R00

SCALE: NTS | WT: | SHEET: