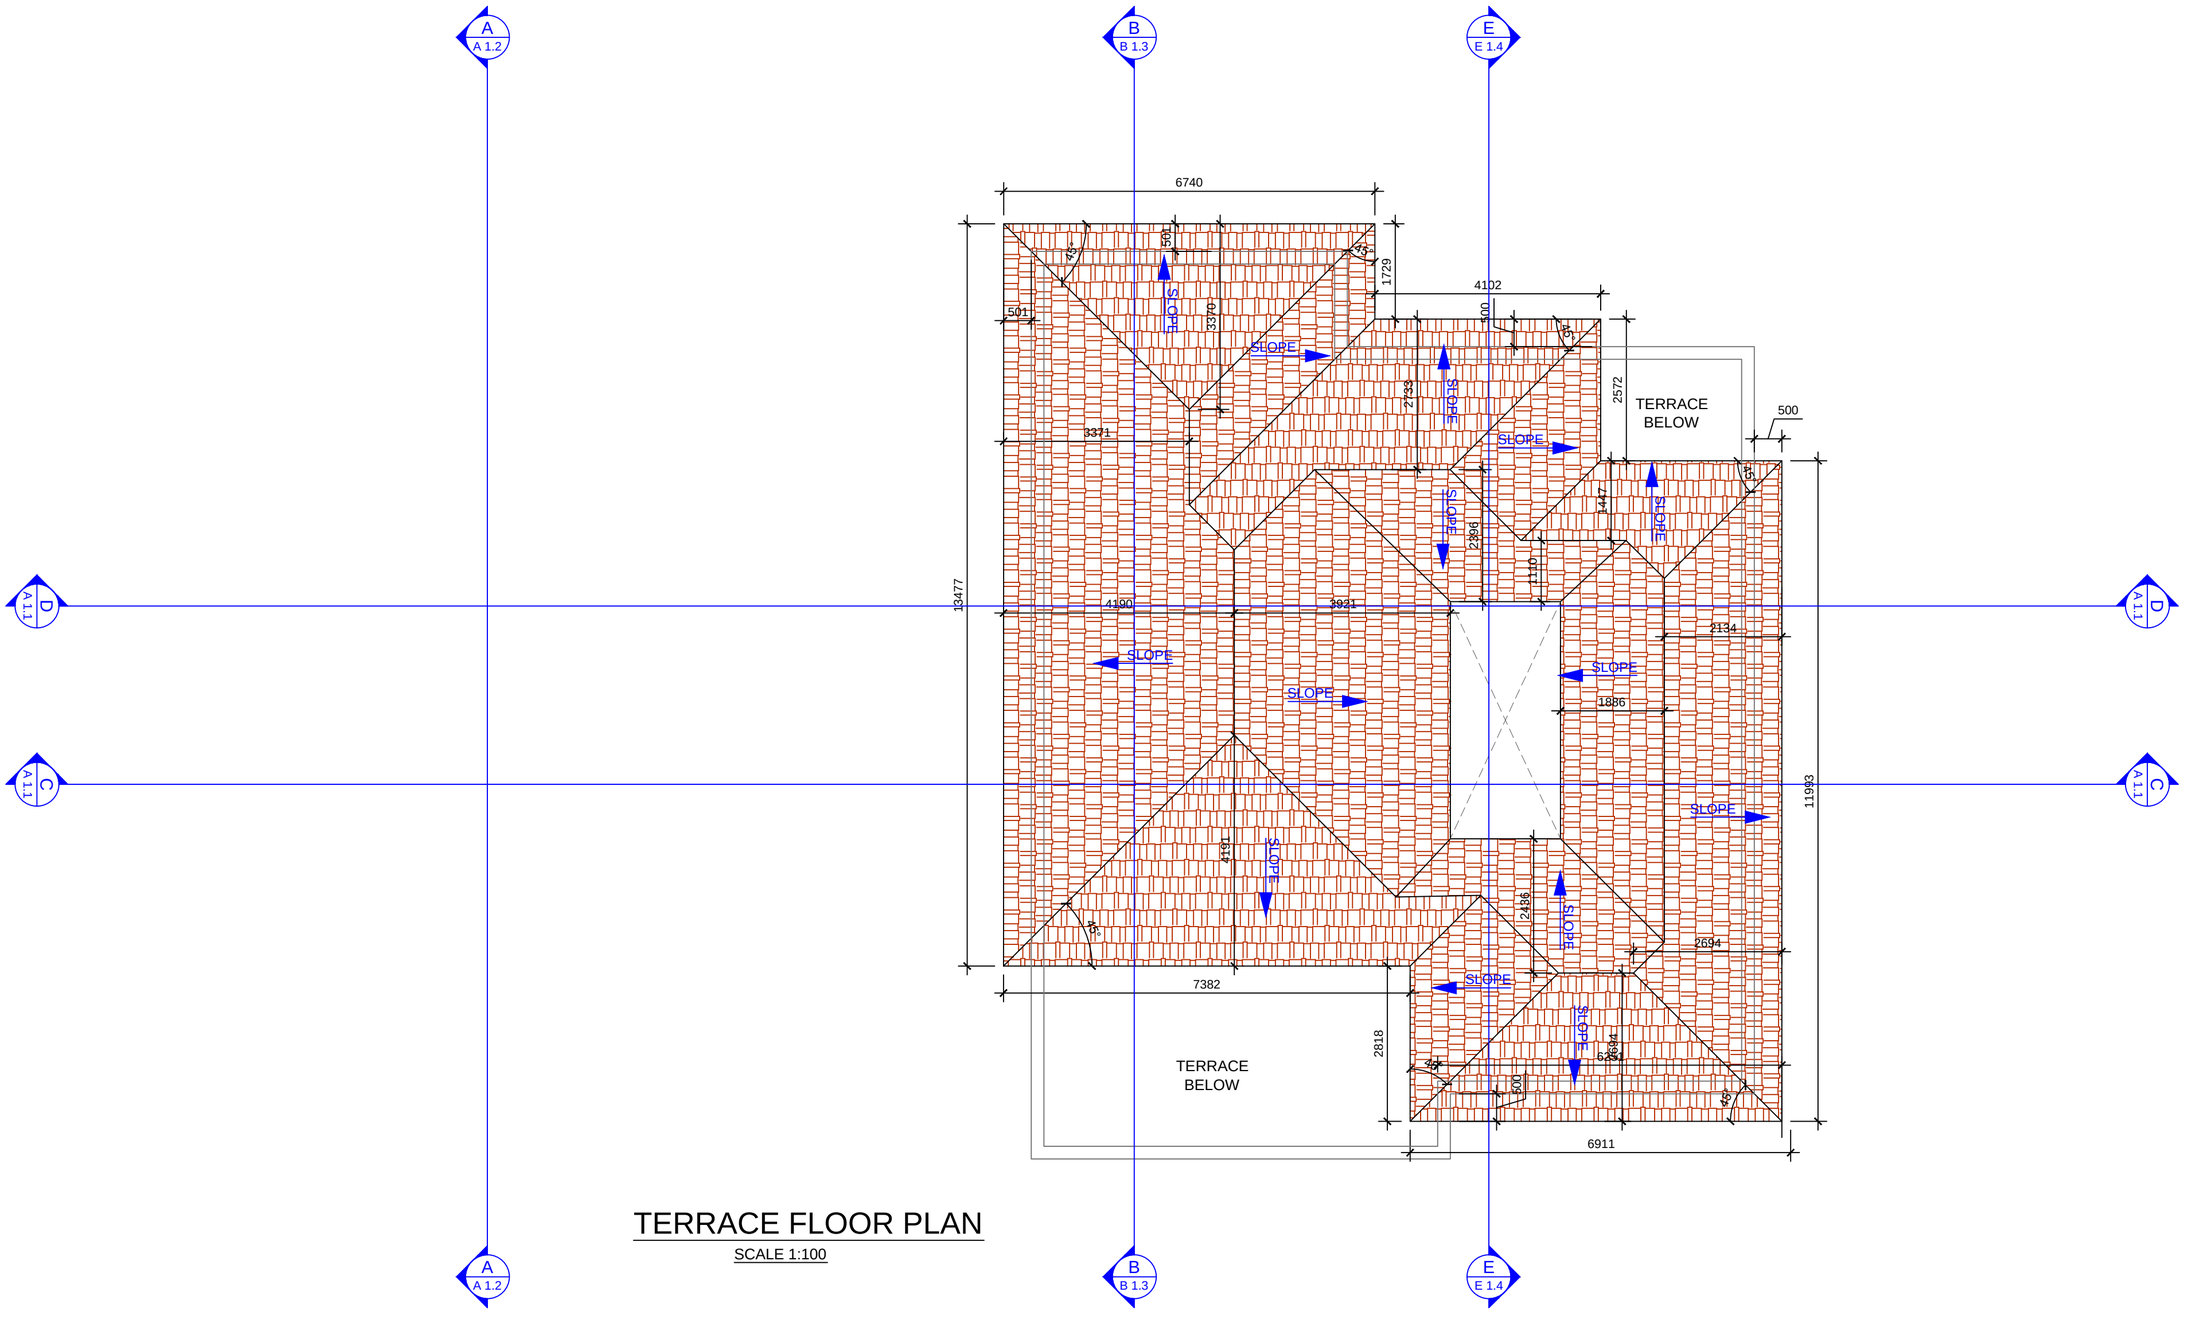


TERRACE FLOOR PLAN

SCALE 1:100

TITLE

NO.	REVISION	DATE	PRINTS	ISSUED TO	DATE
			-		
			-		
			-		
			-		
			-		
			-		

DWG. REMARK

GOOD FOR CONSTRUCTION

SCHEDULE OF CLEAR OPENING AFTER PLASTER

DOOR	CODE	SIZE	CILL	LINTEL	NO.
	D	1.50 X 2.26	-	2.26	
	D1	0.90 X 2.26	-	2.26	
	D2	0.80 X 2.26	-	2.26	
	D3	1.00 X 2.26	-	2.26	
	D4	1.94 X 2.26	-	2.26	
	D5	2.27 X 2.26	-	2.26	
	D6	2.72 X 2.26	-	2.26	
	D7	1.30 X 2.26	-	2.26	
	D8	2.00 X 2.26	-	2.26	

SCHEDULE OF CLEAR OPENING AFTER PLASTER

WINDOW	CODE	SIZE	SILL	LINTEL	NO.
	W	-	0.76	2.26	
	W1	2.40 X 1.80	0.46	2.26	
	W2A	1.80 X 1.80	0.46	2.26	
	W3	1.50 X 1.50	0.76	2.26	
	W4	1.20 X 1.50	0.76	2.26	
	W4A	1.20 X 1.96	0.30	BEAM	
	W5	0.90 X 0.90	1.36	2.26	
	V	0.60 X 0.75	1.51	2.26	

NOTES -

- ALL DESIGNS ARE PROPERTY OF THE ARCHITECTS PIYUSH KHADKE AND CANNOT BE USED WITHOUT THEIR PERMISSION.
- DO NOT SCALE THE DRAWINGS
- ALL MEASUREMENTS TO BE CHECKED AND VERIFIED ON SITE.
- ANY DISCREPANCIES IN DIMENSION BETWEEN DRAWING AND SITE MUST BE CLARIFIED WITH THE ARCHITECTS PRIOR TO EXECUTION.
- THIS DRAWINGS, DETAILS, SPECIFICATIONS, QUANITIES ETC. ARE BASED ON THE INFORMATION SUPPLIED BY THE OWNER / POWER OF ATTORNEY HOLDER, BUILDER, PROMOTER ETC.
- ALL PLANS ARE SUBJECT TO SANCTION OF CONCERED AUTHORITIES.
- THE ARCHITECT WILL NOT BE RESPONSIBLE FOR INCORRECT, BAD OR DEFECTIVE WORK.
- RESPONSSIBLE PARTY FOR CONSTRUCTION OWNER / CONTRACTOR .

NORTH

SIGN & STAMP

PROJECT

PROPOSED BUNGALOW

AT FOREST TRAIL, BHUGAON PUNE

MR.VIKAS BHILARE

SECTOR R10A_BHILARE BUNGALOW
S2 -213 + K2 - 214_

piyush khadke

architects & interior design consultants

4th floor , kavyanjali building opp. vishawas samrudhi society
vadgaon,pune-411041 (MAH.) INDIA
mob no : +91 - 9595558119
email id : piyushdkhadke@gmail.com

DATE	DRG.NO.	DWG BY	CHECKED BY	REVISION
29.08.22	R-2/19.08	piyush		R-2