



PRODUCED BY AN AUTODESK EDUCATIONAL PRODUCT

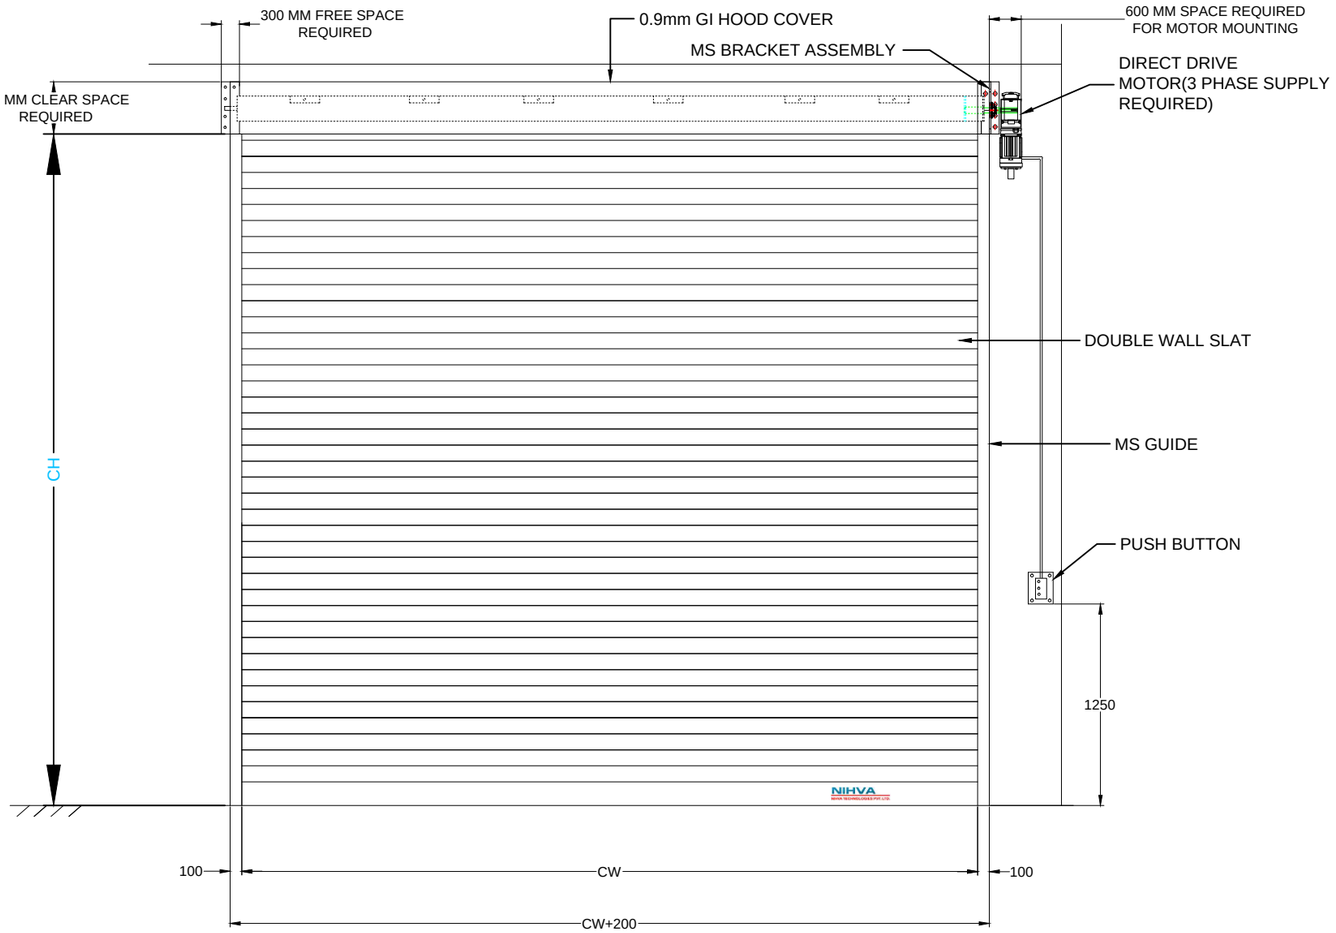

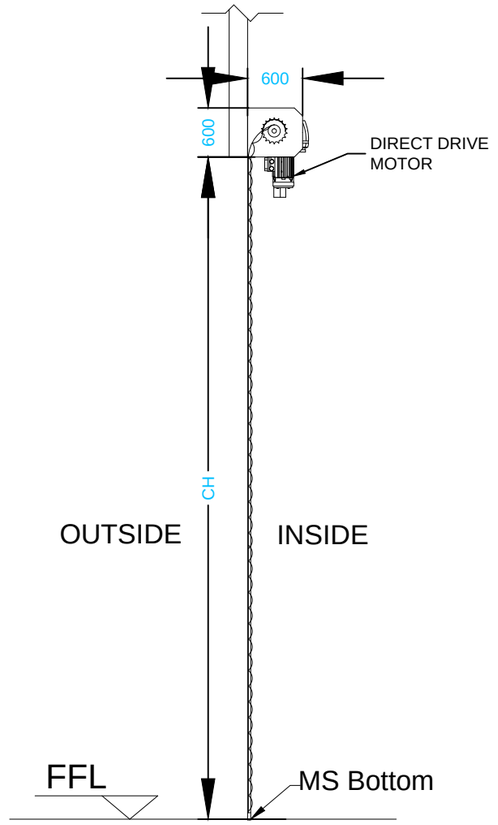


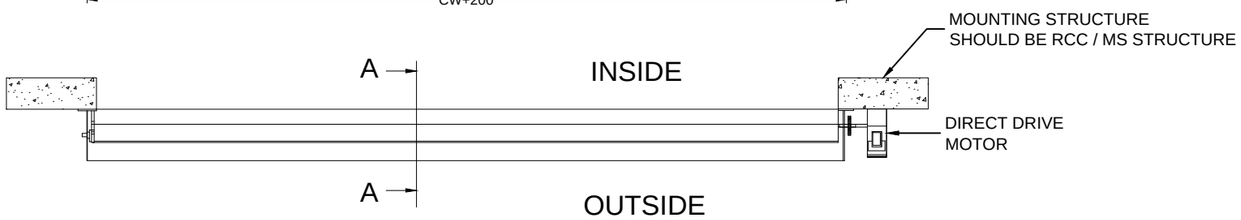

Section A-A

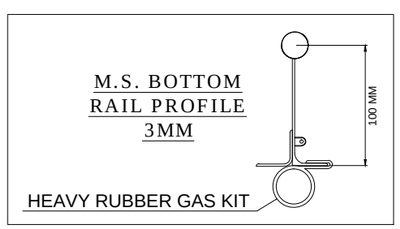


Main Slats
Double Wall Puff Rolling Shutter

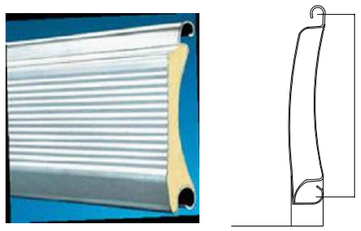

| Rev.no | Revision | Revised BY | Date |
|---|---|---|---|
| 1. | clear width changed 4600 to 4800mm | Sujata | 28/12/2021 |
| 2. | Mentioned title name RS01 & RS02 | Sujata | 28/12/2021 |
| 3. | Mentioned puff rolling shutter | Sujata | 28/12/2021 |
| 4. | Changed view of the rolling shutter | Sujata | 28/12/2021 |

COLOR OF SLATS & SHUTTER -RAL9002 (GRAY WHITE)

DIMENSION :

| CLEAR WIDTH | CLEAR HEIGHT | QUANTITY |
|---|---|---|
| 4800 mm | 3900 mm | 2 NOS |
| | | |
| | | |

NOTE:-

1.STRUCTURE FOR SHUTTER WILL BE IN CLIENT'S SCOPE.
2. 3 PHASE SUPPLY SHOULD BE PROVIDED.

NIHVA TECHNOLOGIES PVT. LTD.
NIHVA TECHNOLOGIES PVT. LTD. PUNE
Email:- info@nihva.com
Website:- www.nihva.com

TITLE:

DOUBLE WALL ROLLING SHUTTER
RS01. LGF south side
RS02. LGF south side

CLIENT'S APPROVAL :

CLIENT - AJAY KALE AND ASSOSIATE

PROJECT -

SITE LOCATION - PIRANGUT

DWG. NO. : NIHVA/21-22/CLT/280

| SCALE: NTS | WT: | SHEET:01 OF 02 |
|---|---|---|

| DRAWN BY: G.P. | DATE: 23-12-2021 |
|---|---|
| CHECKED BY: A.K. | DATE: 23-12-2021 |
| APPROVED BY : | |

If any queries contact : design@nihva.com

NOTE: ALL DIMENSIONS ARE IN mm

THIS DRAWING & DESIGN IS THE PROPERTY OF NIHVA TECHNOLOGIES, NOT TO BE SOLD OR COPIED TO ANY OTHER CONCERN.
PRODUCED BY AN AUTODESK EDUCATIONAL PRODUCT

PRODUCED BY AN AUTODESK EDUCATIONAL PRODUCT