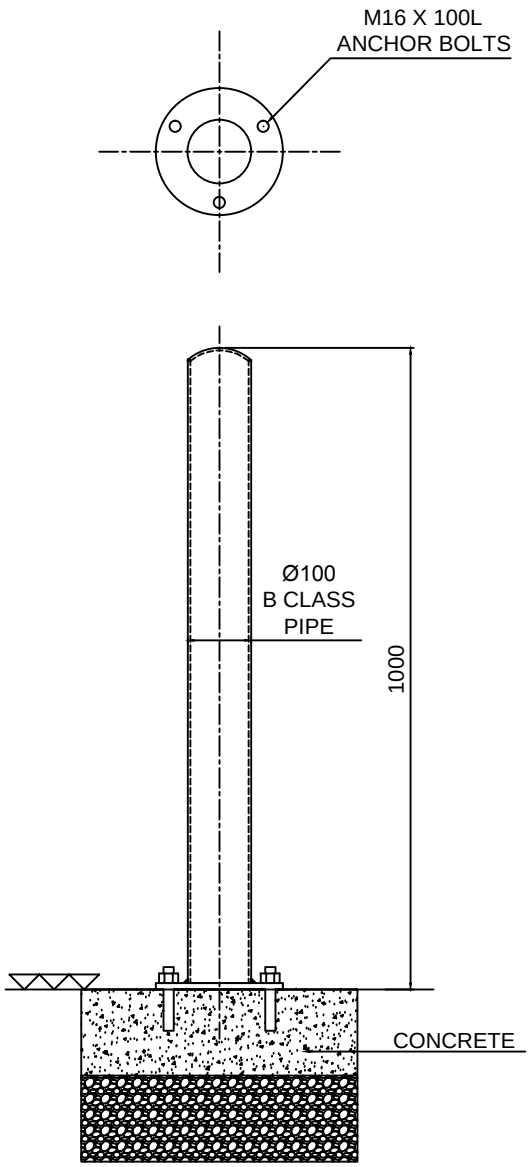


SPECIFICATION:

HEIGHT : 1000 MM (ABOVE FLOOR LEVEL)
BASE DIA : 200 MM
WEIGHT : 15 KGS(WITH BASE PLATE)
MATERIAL : M.S (IS 1161-1968)

FINISH :
POWDER COATED

HARDWARE:
ANCHOR BOLT : M16 X 100L = 3 NOS
WASHER : FOR M16

TOLERANCE- ±5mm

This drawing & design is the property of NIHVA TECHNOLOGIES. Not to be sold or copied to any other concern.

TITLE: BOLLARD POST				NIHVA TECHNOLOGIES PVT. LTD. PUNE Tel : 020 66304033 Email:- info@nihva.com Website:- www.nihva.com	
	NAME	SIGN	DATE		
DRAWN	P.A		07.02.2020	CLIENT -	
CHECK	G.J		07.02.2020	PROJECT -	
APPRD.				SITE LOCATION -	
If any queries contact : design@nihva.com				DWG. NO. : NIHVA/19-20/VDR/309	REV- R00
ALL DIMENSION ARE IN mm				SCALE: NTS	WT: SHEET: