




NOTE : ~ PLEASE MAINTAIN 8 MM GAP BETWEEN TWO LIP BUSHES.

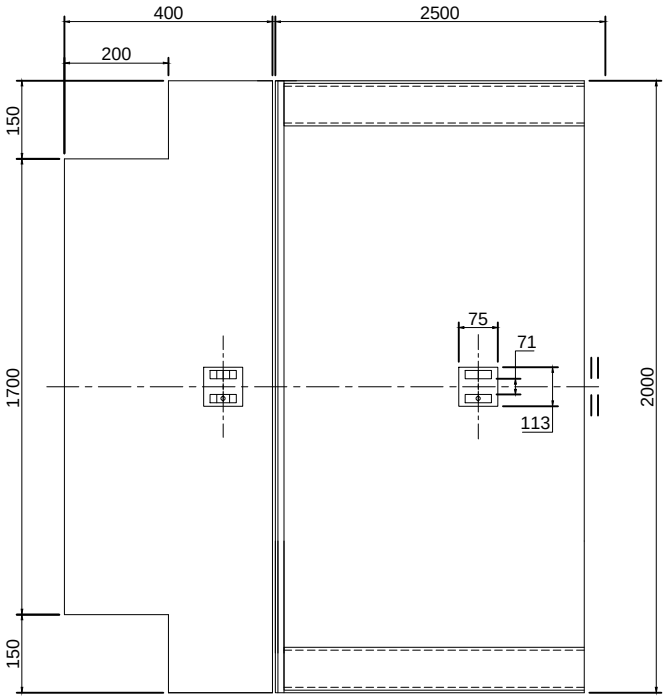

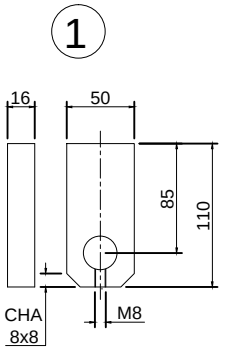

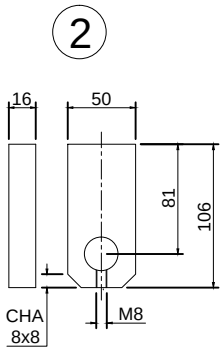

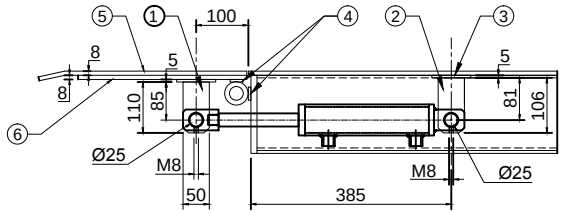

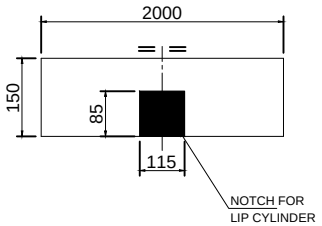

NOTE:~ MTL : MS

PART NO.	PART NAME	DESCRIPTION	QTY
1.	FLAT	50 X 16 X 113L	2 NOS
2.	FLAT	50 X 16 X 110L	2 NOS
3.	FLAT	75 X 5 X 113L	2 NOS
4.	FLAT	25 X 5 X 80L	19 NOS
5.	CHEQ. SHEET	400 X 8 X 2000L	1 NO
6.	PLAIN. SHEET	350 X 8 X 2000L	1 NO

TOLERANCE - ±5mm

This drawing & design is the property of NIHVA TECHNOLOGIES. Not to be sold or copied to any other concern.

TITLE

LIP CYL MOUNTING

NIHVA TECHNOLOGIES PVT. LTD.
NIHVA TECHNOLOGIES PVT. LTD. PUNE
Tel : 020 66304033
Email:- info@nihva.com
Website:- www.nihva.com

	NAME	SIGN	DATE
DRAWN	PRADEEP		23.04.2018
CHECK	PRADEEP		23.04.2018
APPRD.	PRADEEP		23.04.2018

CLIENT -

PROJECT - NSDL2025

SITE LOCATION -

If any queries contact : design@nihva.com

DWG. NO. : NIHVA/18-19/NSDL2025_006

ALL DIMENSION ARE IN mm

SCALE: NTS | WT: | REV- 0