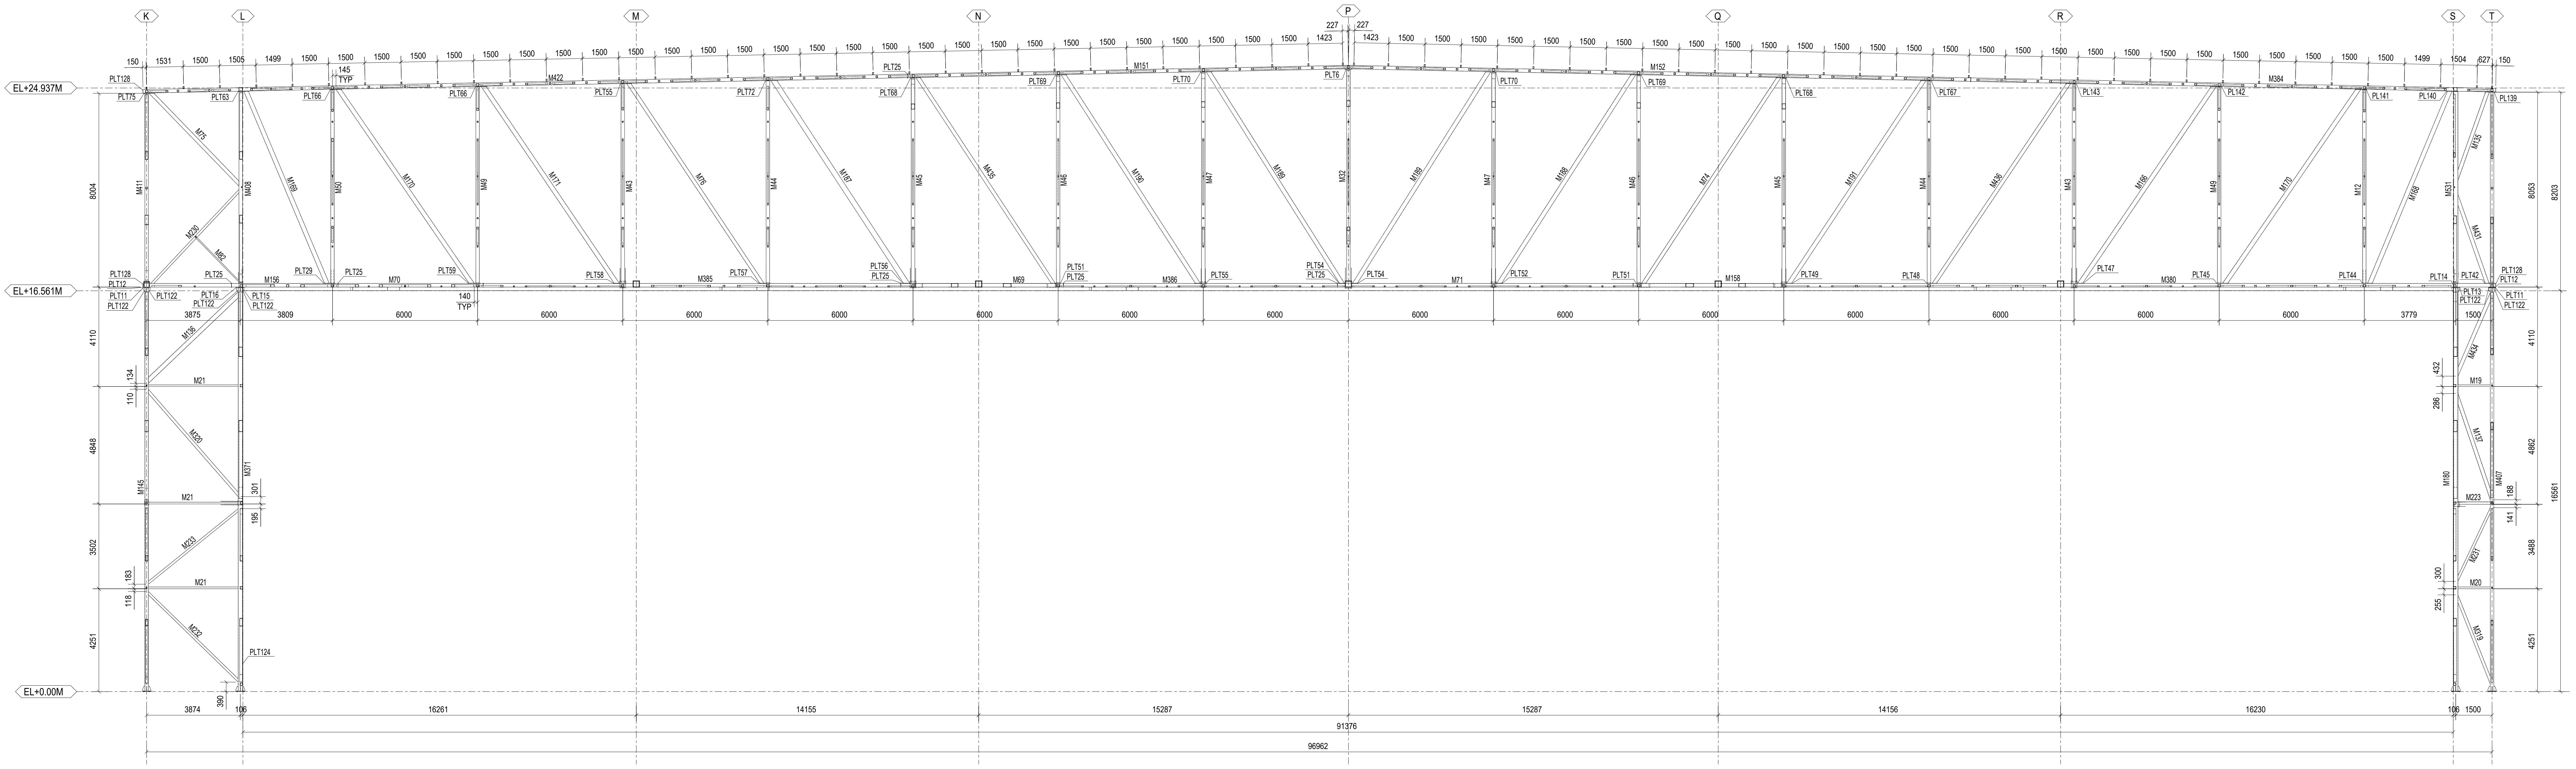
K
L
M
N
P
Q
R
S
T
EL+24.937M
EL+16.561M
EL+0.00M
150
1531
1500
1505
1499
1423
227
145 TYP
140 TYP
3875
3809
6000
3779
1500
8004
8203
8553
4110
4848
3502
4251
4862
3488
16561
3874
106
16261
14155
15287
14156
16230
91376
96962
300
PLT25
M21
M151
M152
M384
M422
M485

GRID @ 2
1:100

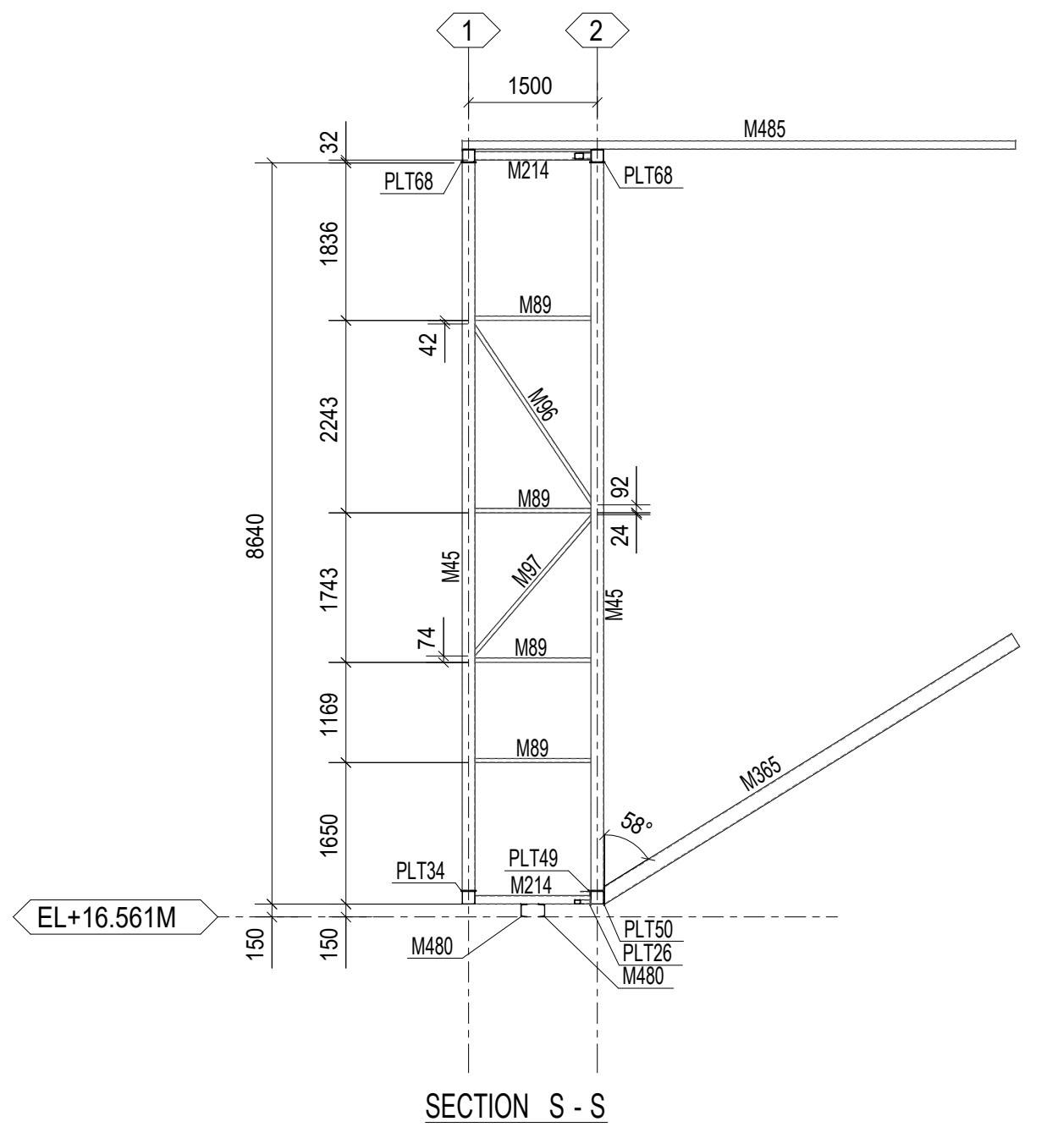
1
2
1500
M485
M214
M89
PLT68
PLT34
PLT49
EL+16.561M
M480
8640
1836
2243
1743
1169
1650
150
32

SECTION S - S
1:80

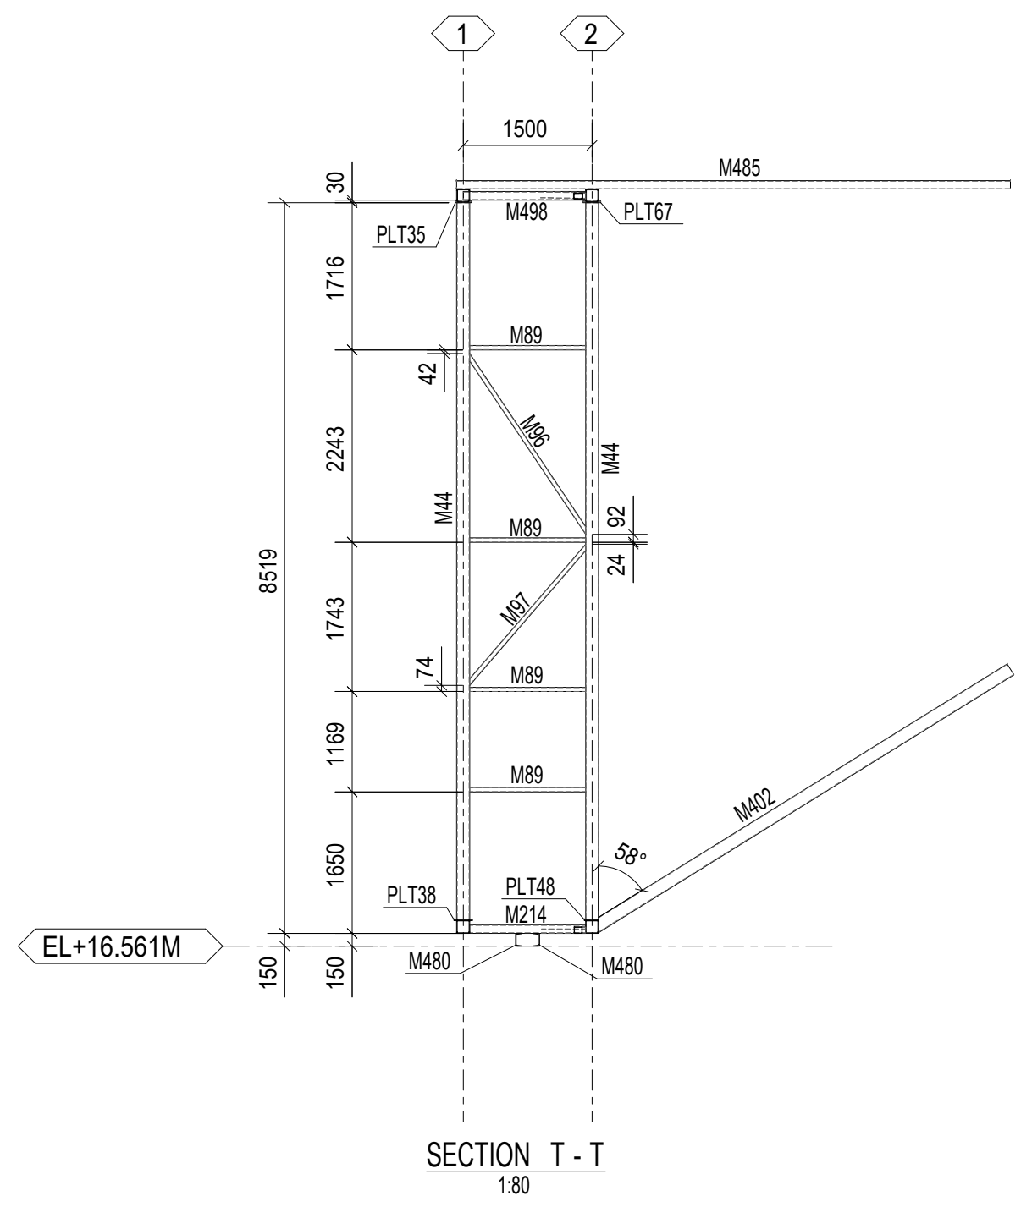
1
2
1500
M485
M498
M89
PLT35
PLT67
PLT38
PLT48
EL+16.561M
M480
8519
1716
2243
1743
1169
1650
150
30

SECTION T - T
1:80

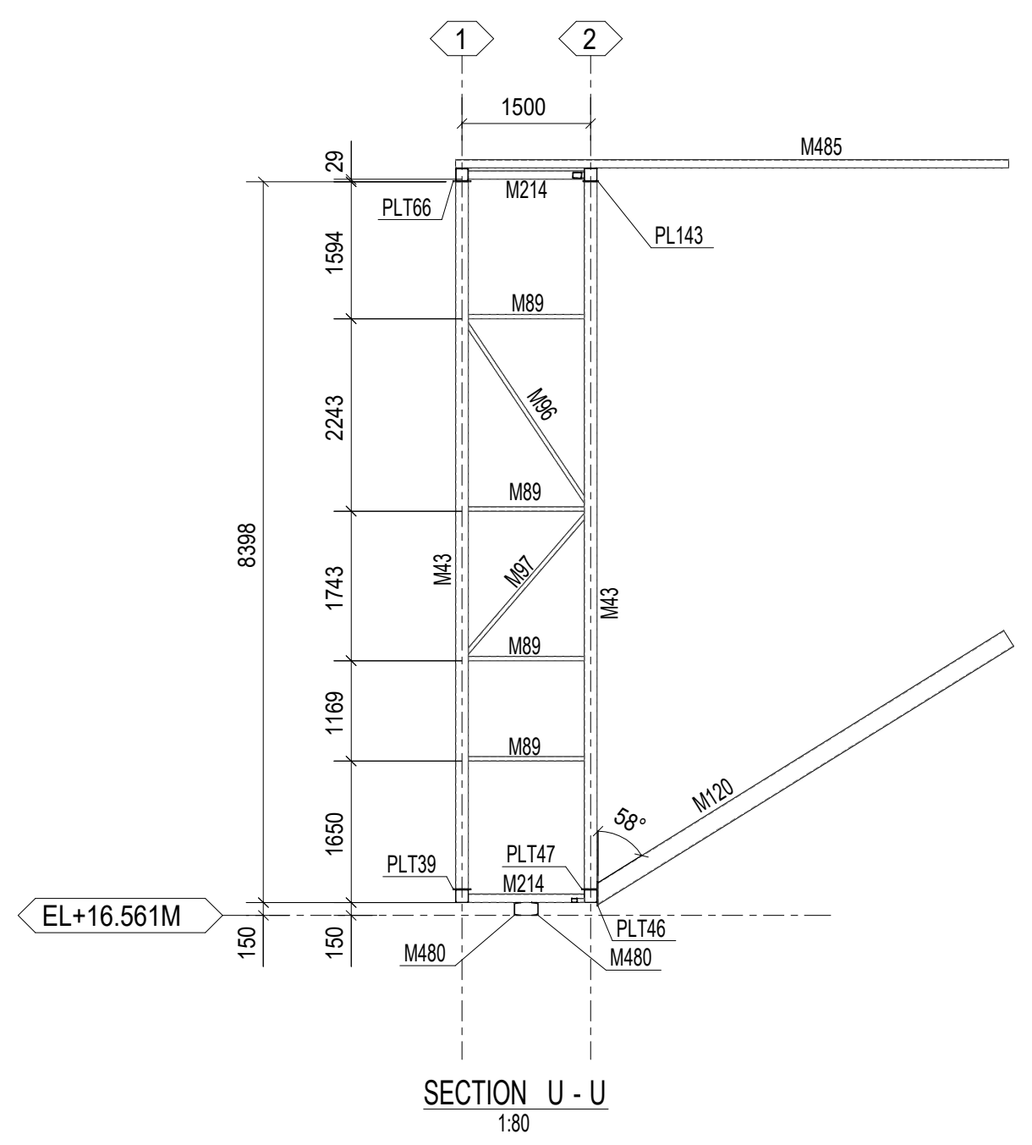
1
2
1500
M485
M214
M89
PLT66
PLT143
PLT39
PLT47
PLT46
EL+16.561M
M480
8398
1594
2243
1743
1169
1650
150
29

SECTION U - U
1:80

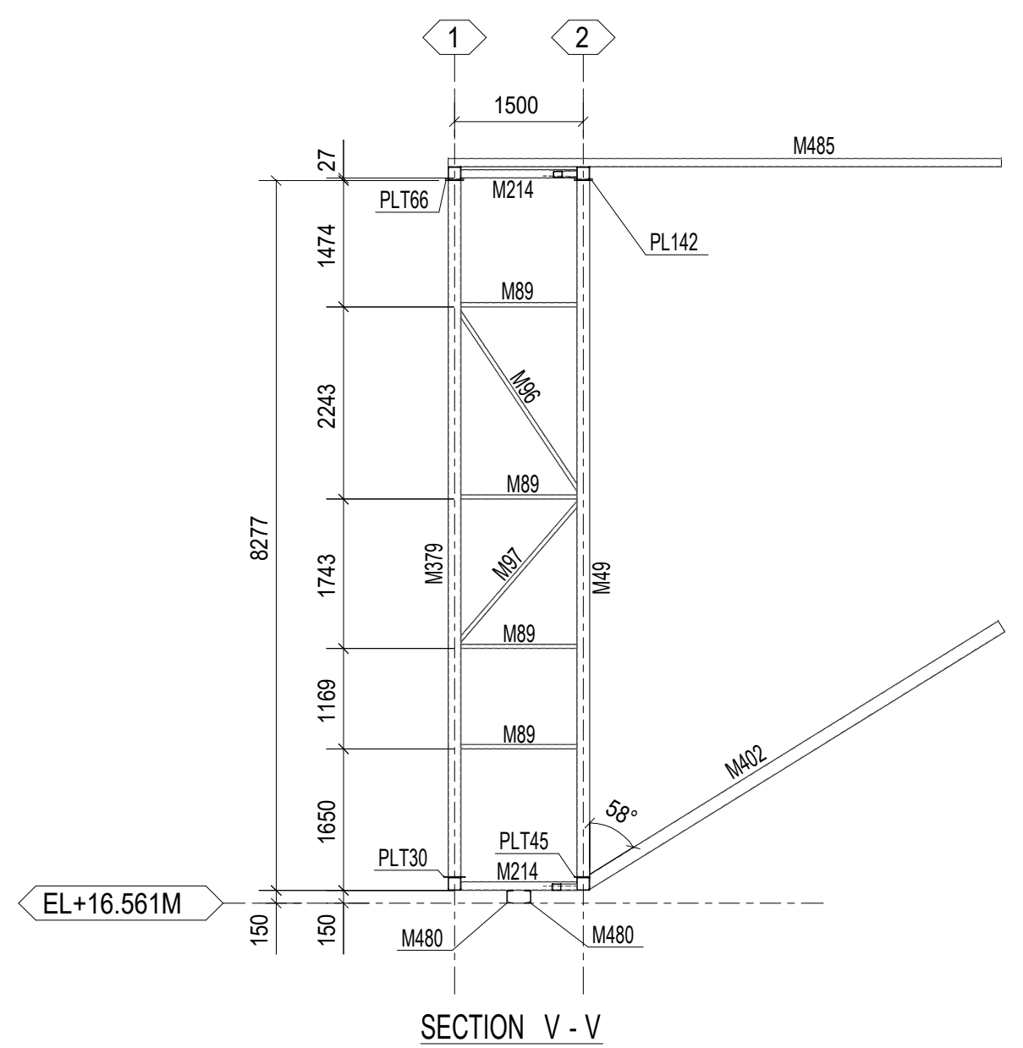
1
2
1500
M485
M214
M89
PLT56
PLT142
PLT30
PLT45
EL+16.561M
M480
8277
1474
2243
1743
1169
1650
150
27

SECTION V - V
1:80

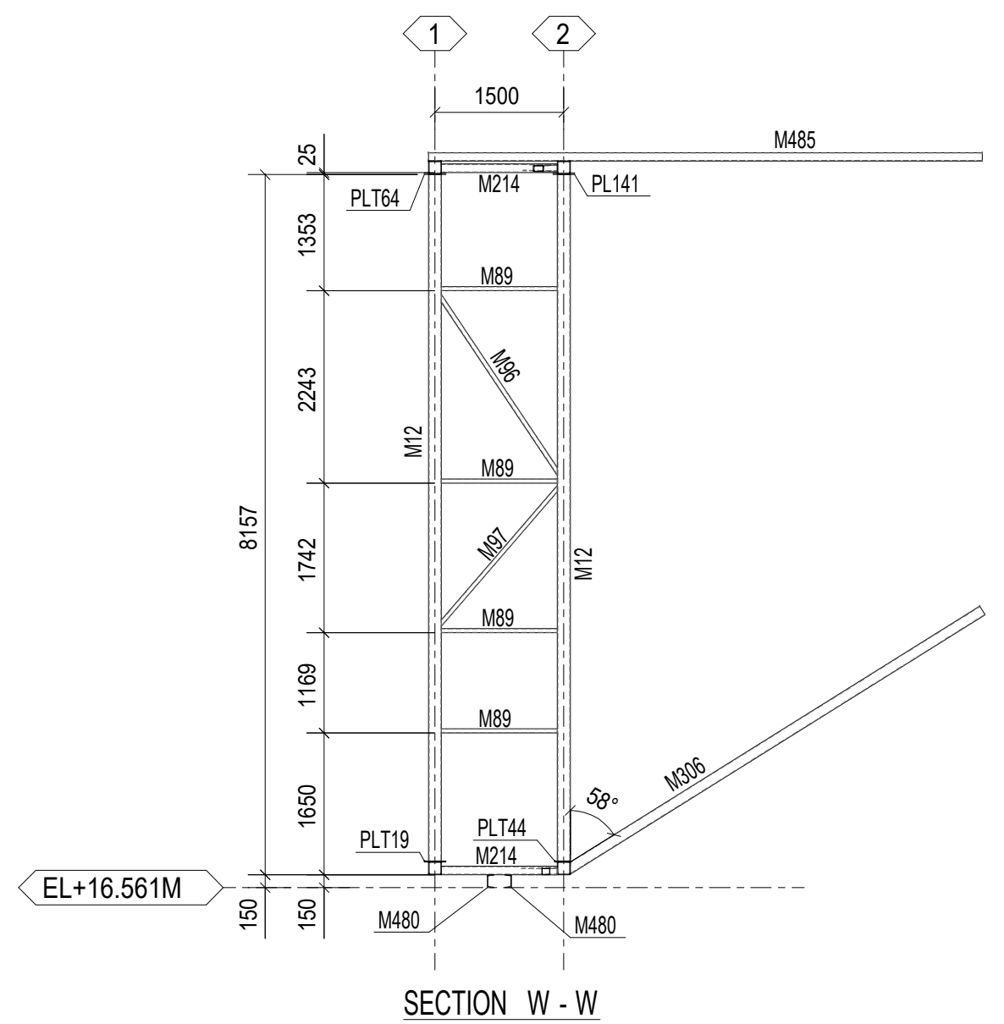
1
2
1500
M485
M214
M89
PLT64
PLT141
PLT19
PLT44
EL+16.561M
M480
8157
1353
2243
1742
1169
1650
150
25

SECTION W - W
1:80

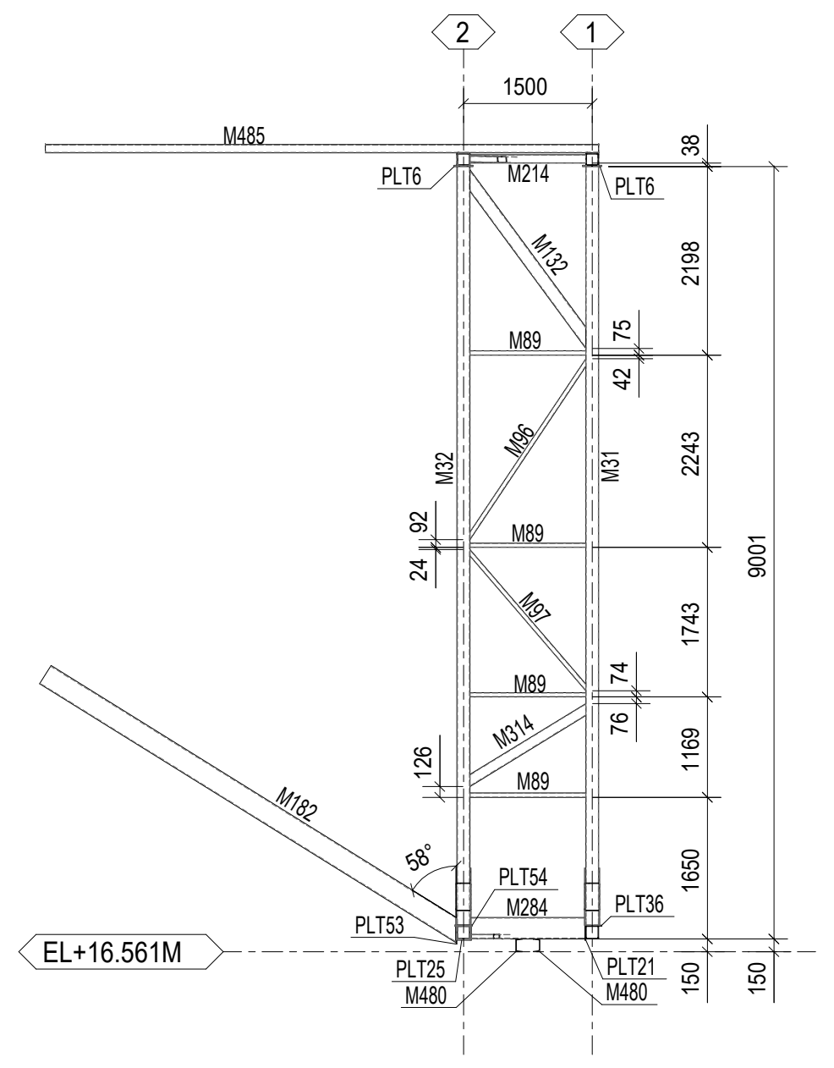
2
1
1500
M485
M214
M89
PLT6
PLT53
PLT34
PLT36
EL+16.561M
M480
9001
2198
2243
1743
1169
1650
150
38

SECTION H - H
1:80

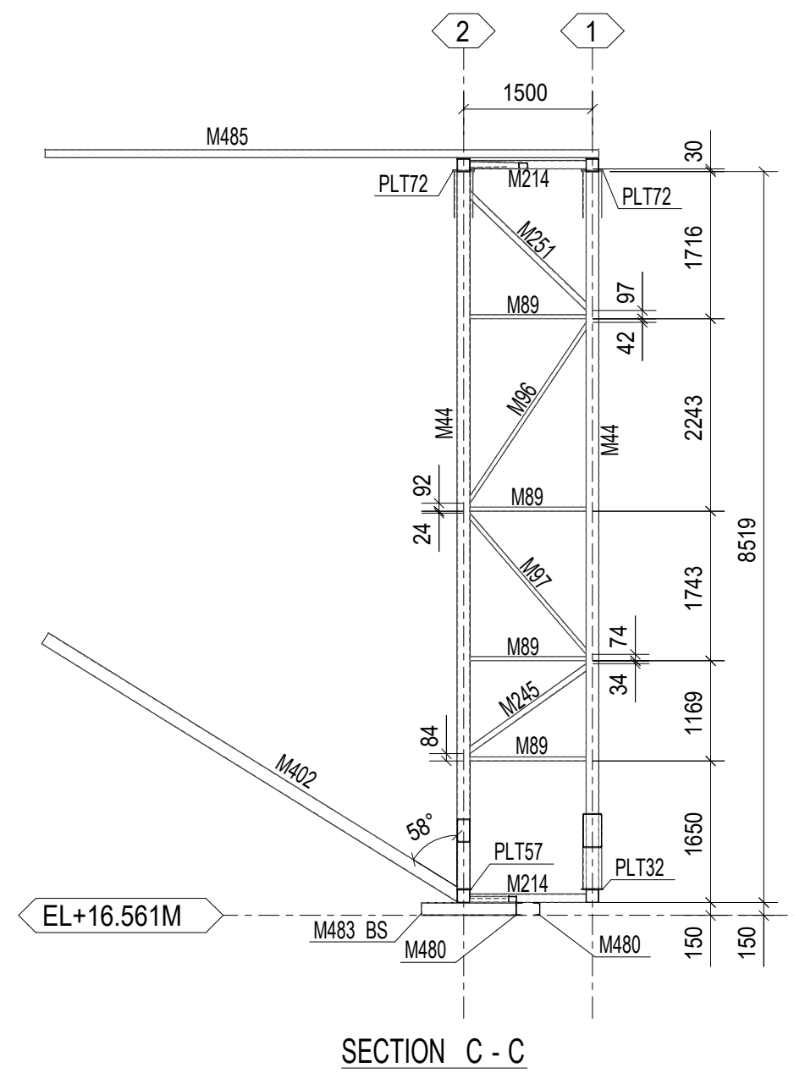
2
1
1500
M485
M214
M89
PLT72
PLT57
PLT32
EL+16.561M
M480
8519
1716
2243
1743
1169
1650
150
30

SECTION C - C
1:80

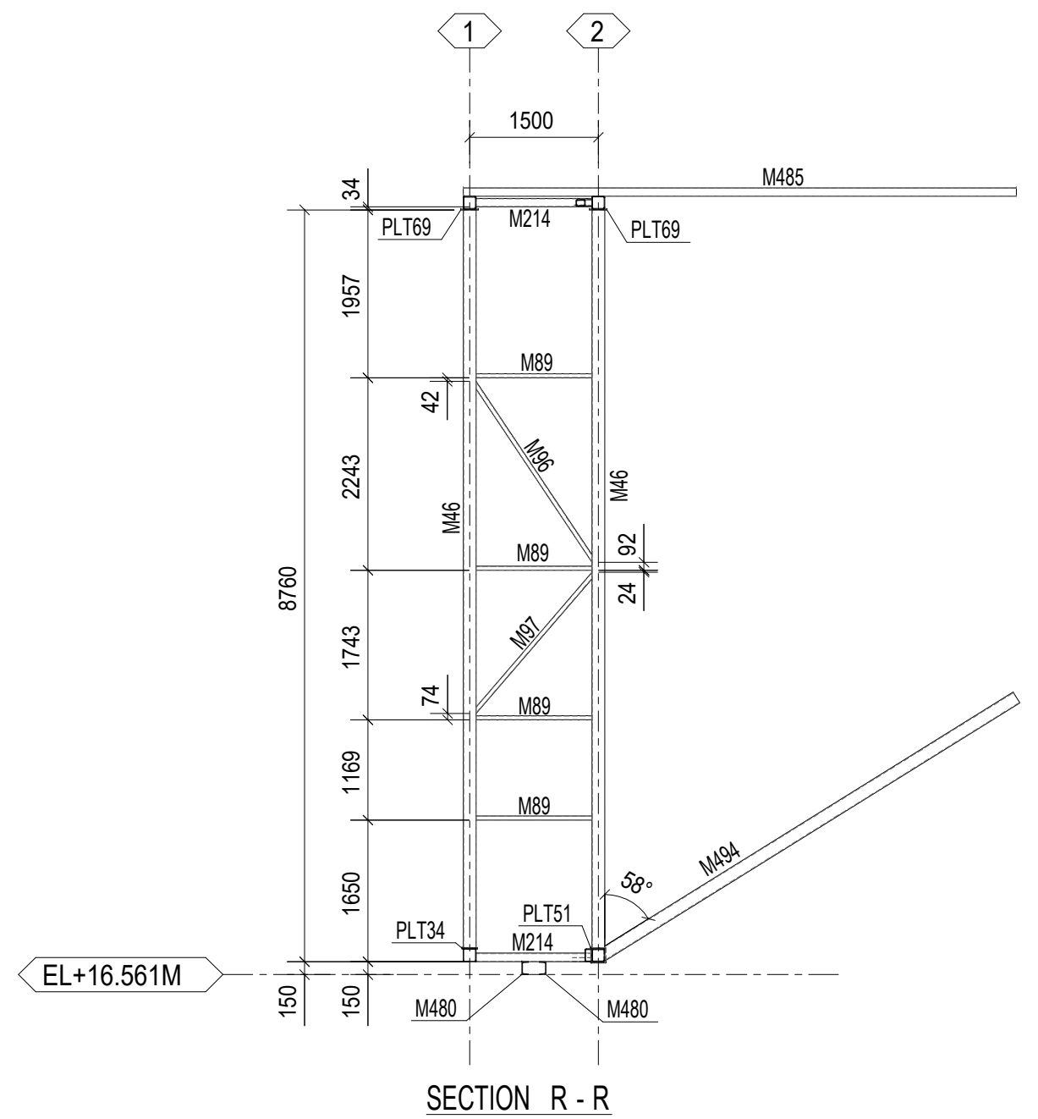
1
2
1500
M485
M214
M89
PLT69
PLT34
PLT51
EL+16.561M
M480
8760
1957
2243
1743
1169
1650
150
34

SECTION R - R
1:80

K
L
M
N
P
Q
R
S
T
2
1
3874
4560
13244
1437
34554
2607
1500
91588
1989
1885
1957
1852
1814
2713
3287
1837
1942
M387
M156
M480
M70
M385
M386
M71
M158
M380
M69
M89
M214
PLT25
PLT124
2x M483
3x M483

SECTION A - A
1:80

K
L
M
N
P
Q
R
S
T
2
1
M485
M484
M422
M151
M152
M384
M381
M382
M214
M217
PLT25
PLT27
PLT73
PLT138
1297
1296
1173
1264
1266
1500
1511
1499
1492
1143
106
96963

SECTION B - B
1:80

K
L
M
N
P
Q
R
S
T
2
1
1500
3874
106
91376
M145
M180
M371
M407
PLT121
PLT17
PLT18
PLT19

SECTION W - W
1:80