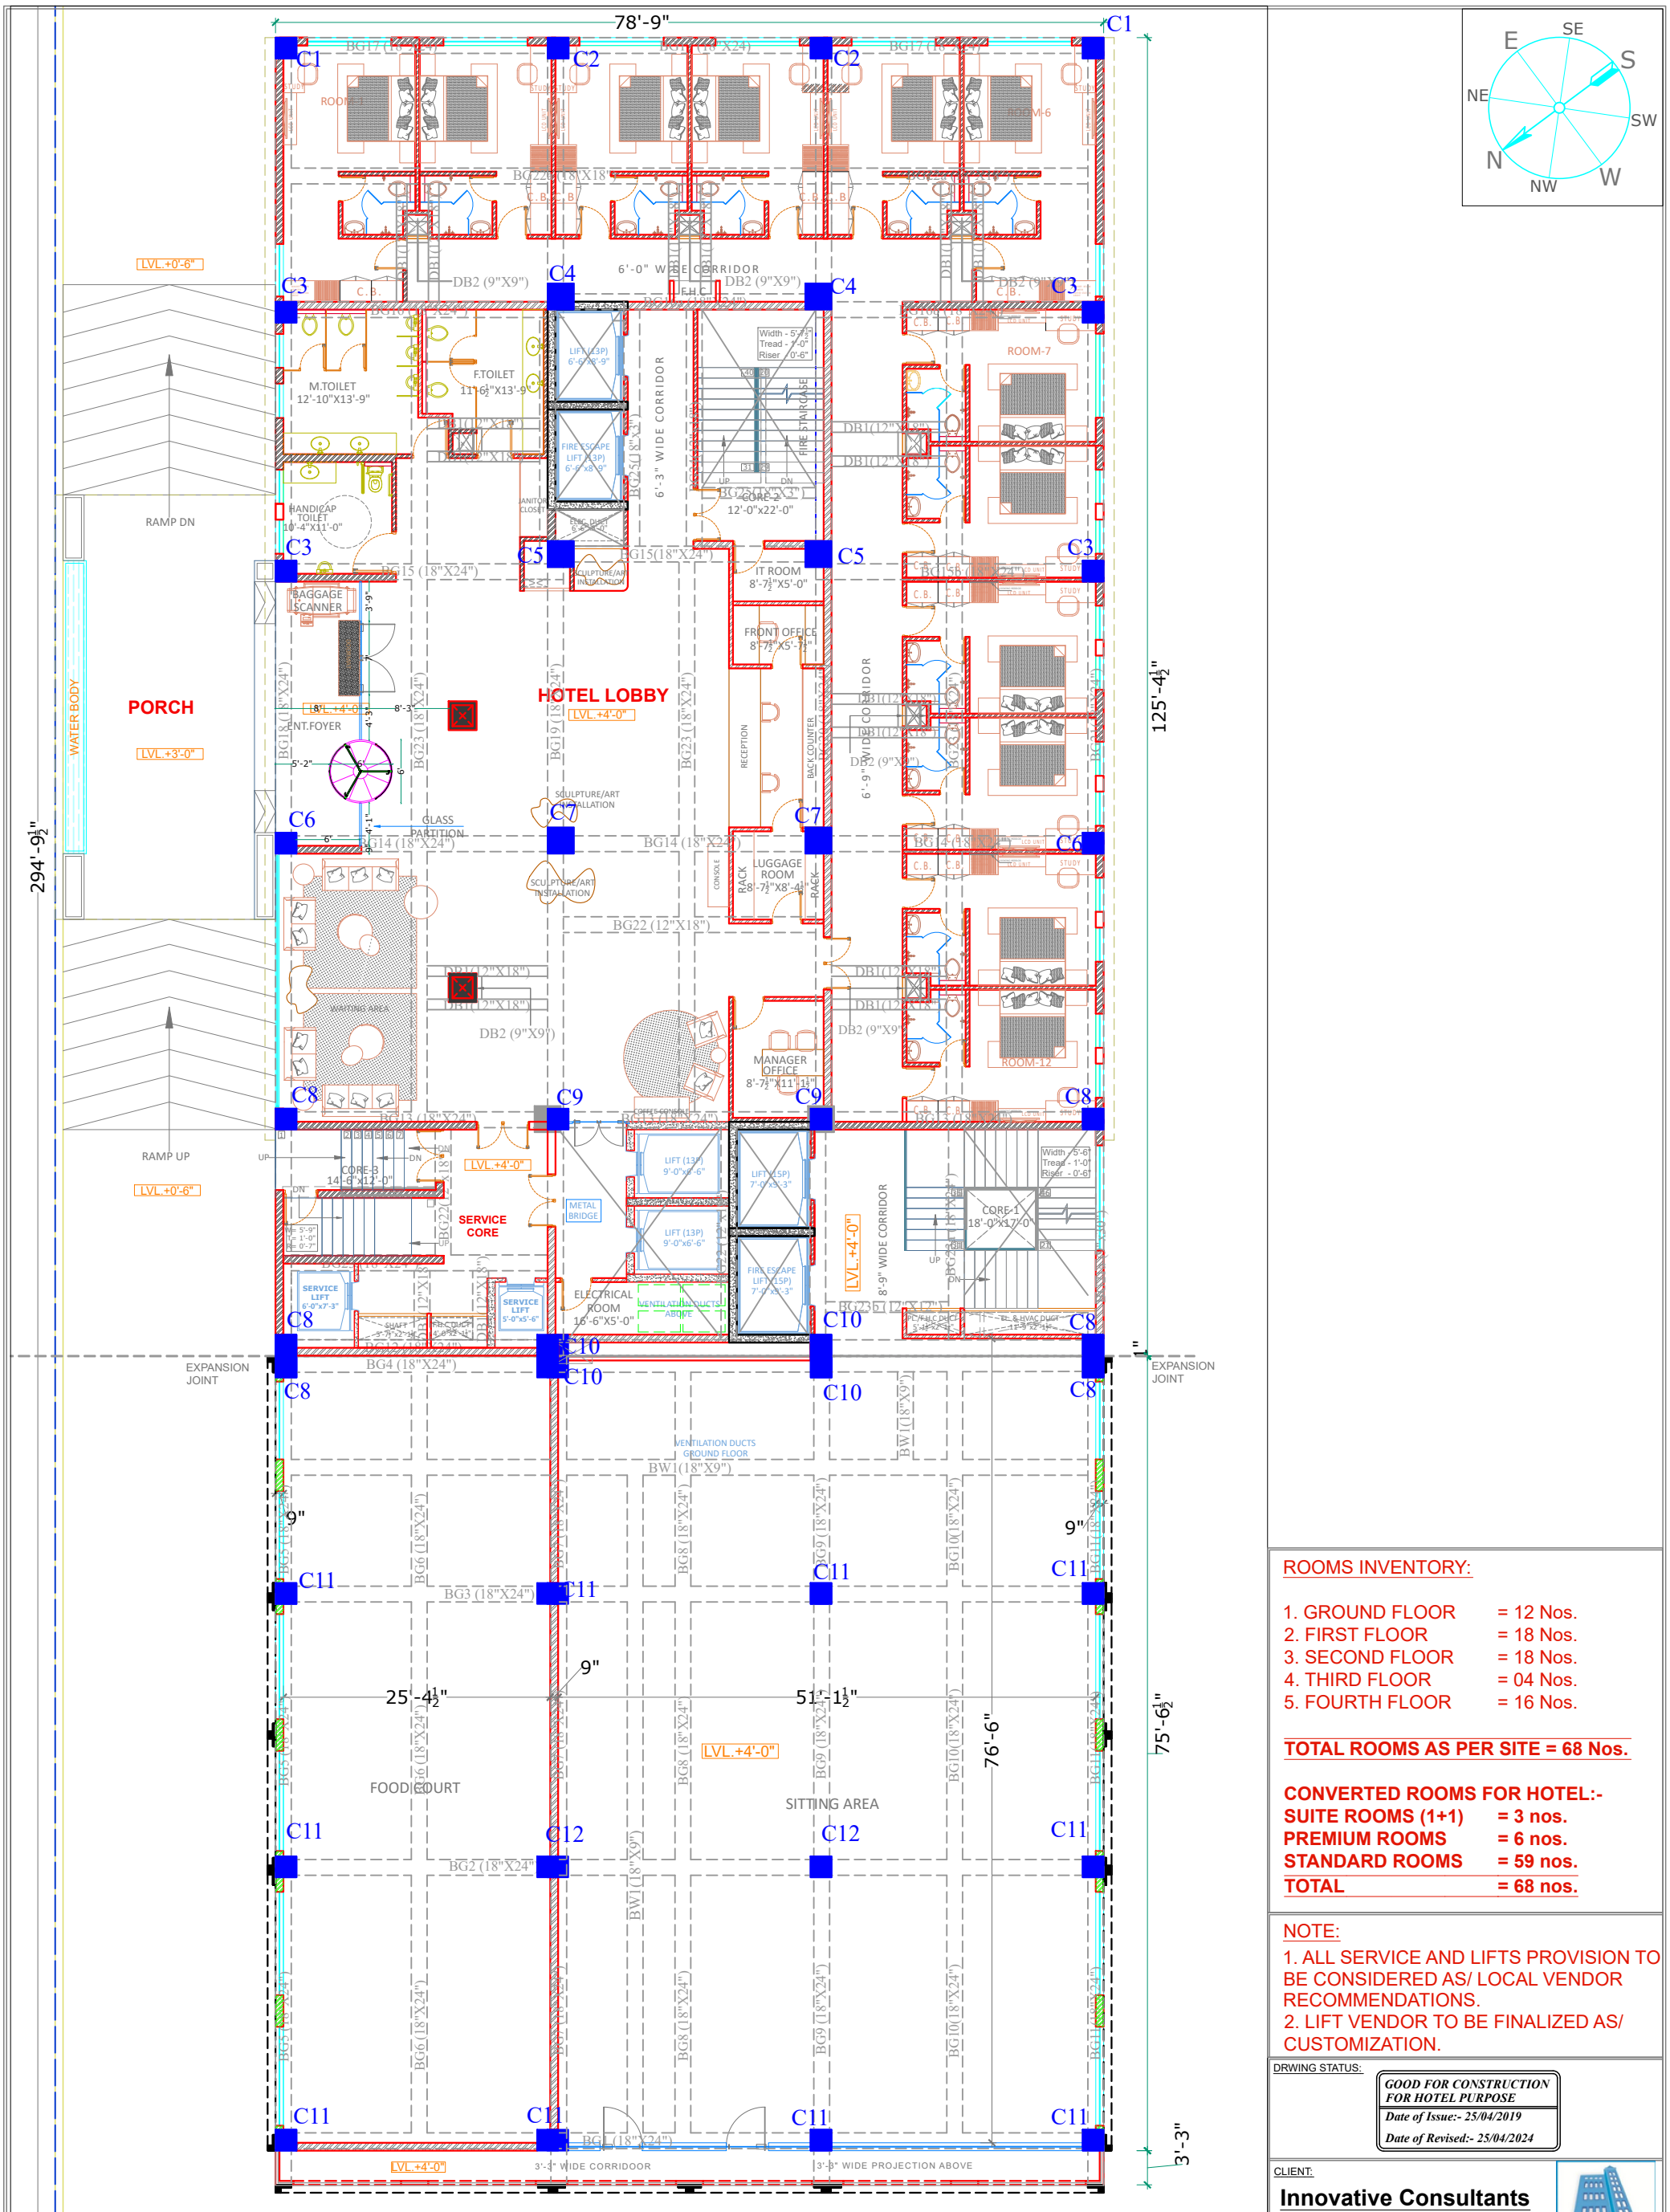


FINAL GROUND FLOOR PLAN

ROOMS INVENTORY:

1. GROUND FLOOR	= 12 Nos.
2. FIRST FLOOR	= 18 Nos.
3. SECOND FLOOR	= 18 Nos.
4. THIRD FLOOR	= 04 Nos.
5. FOURTH FLOOR	= 16 Nos.
TOTAL ROOMS AS PER SITE	**= 68 Nos.**

CONVERTED ROOMS FOR HOTEL:-

SUITE ROOMS (1+1)	= 3 nos.
PREMIUM ROOMS	= 6 nos.
STANDARD ROOMS	= 59 nos.
TOTAL	= 68 nos.

NOTE:

1. ALL SERVICE AND LIFTS PROVISION TO BE CONSIDERED AS/ LOCAL VENDOR RECOMMENDATIONS.
2. LIFT VENDOR TO BE FINALIZED AS/ CUSTOMIZATION.

DRWING STATUS:

GOOD FOR CONSTRUCTION FOR HOTEL PURPOSE
Date of Issue:- 25/04/2019
Date of Revised:- 25/04/2024

CLIENT:

Innovative Consultants
(A PMC COMPANY)
www.innovativeconsulting.in

PROJECT:


HOTEL AT JALANDHAR (PUNJAB)

NOTE:- 1. This drawing is a COPYRIGHT & PROPERTY of STUDIO ARDETE, and is NOT TO BE REPRODUCED, COPIED, HANDED OVER to third party or used for any other purpose other than for which its intended.
2. While every attempt has been made in the preparation of this drawing and to avoid mistakes the maker cannot guarantee against human error. The contractor on job must check all dimensions and other details and be responsible for the same.


PROJECT TITLE: HOTEL PLANING			
PROJECT NO : HS0010			
DRAWING TITLE : FINAL GROUND FLOOR PLAN			
PURPOSE : TEN ☐ GFC ■ ASB ☐ REV ■			
SCALE:- N.T.S	DRAWN BY:-	CHECKED BY:-	
DATE:- 10/01/2025	SANJAY	SANCHIT DHIMAN	
DWG NO-		REVISION:	

ARCHITECTS:

Studio Ardete Pvt. Ltd.
SCO - 43, First Floor, Swastik Vihar, MDC, Panchkula - 134109, Chandigarh (Tricity)
TEL: 0172-4020185
EMAIL: info@studioardete.com

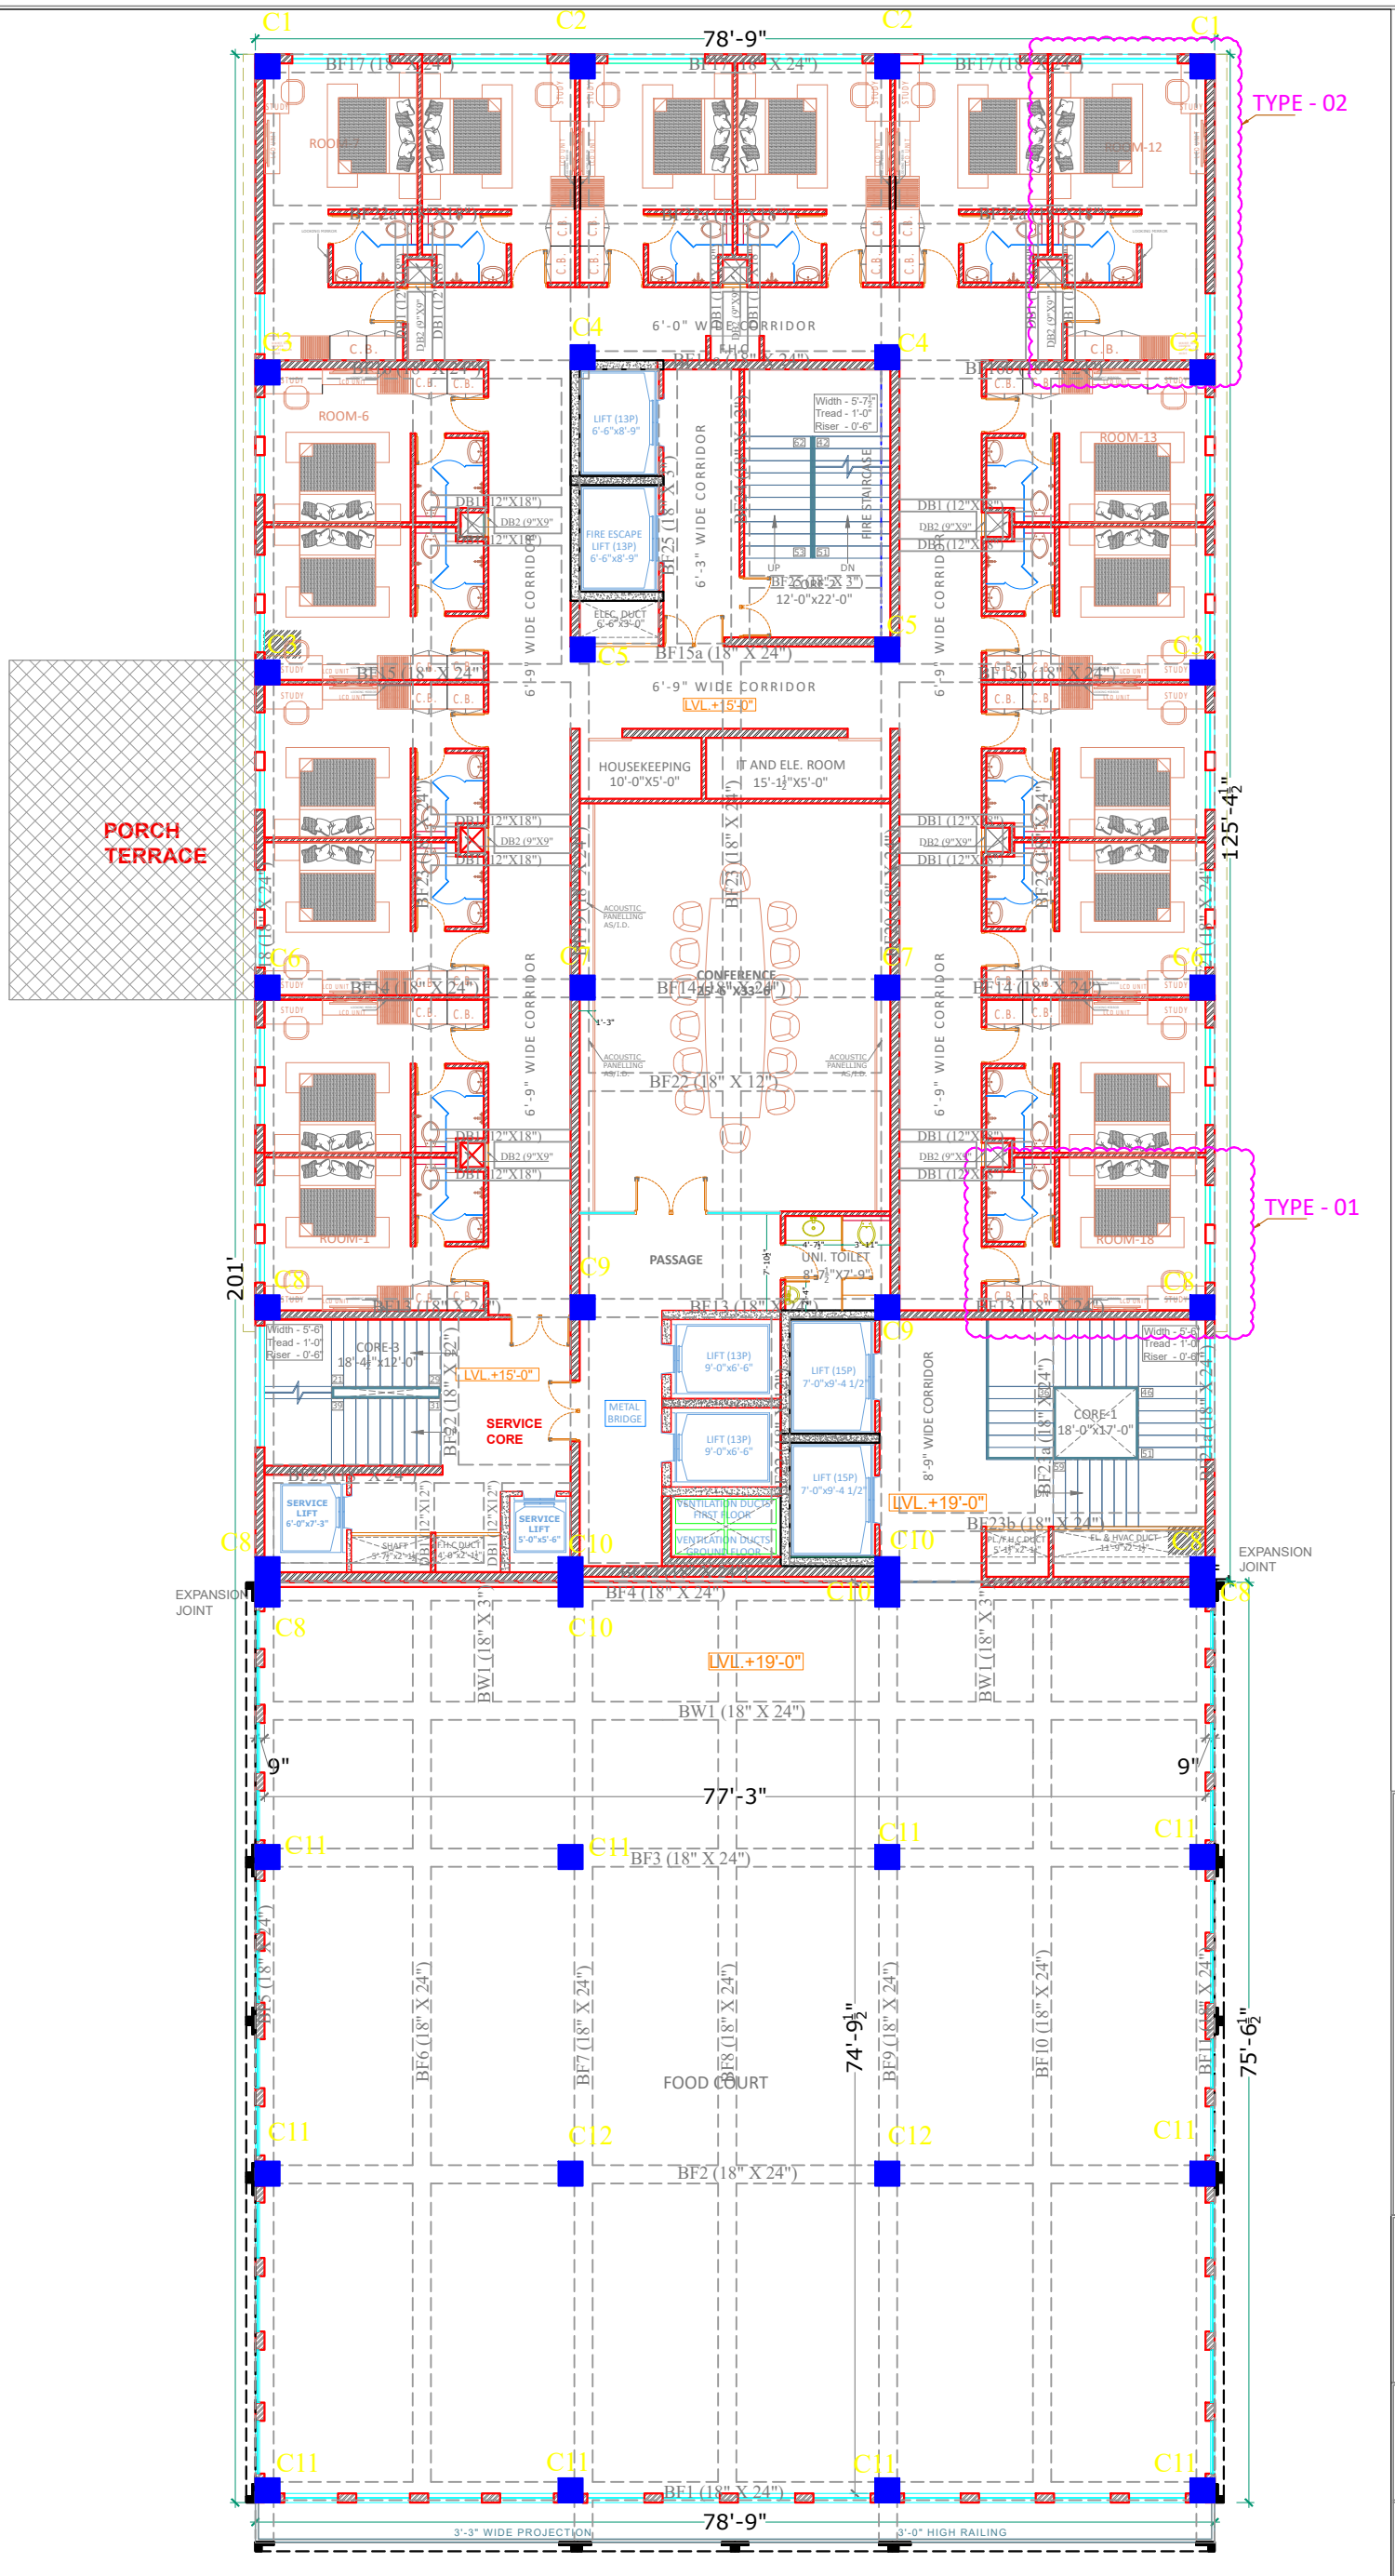

FINAL FIRST FLOOR PLAN

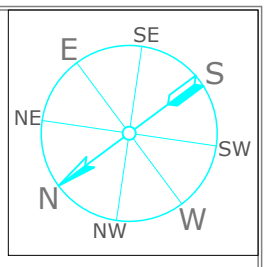

ROOMS INVENTORY:

1. GROUND FLOOR	= 12 Nos.
2. FIRST FLOOR	= 18 Nos.
3. SECOND FLOOR	= 18 Nos.
4. THIRD FLOOR	= 04 Nos.
5. FOURTH FLOOR	= 16 Nos.

TOTAL ROOMS AS PER SITE = 68 Nos.

CONVERTED ROOMS FOR HOTEL:-

SUITE ROOMS (1+1)	= 3 nos.
PREMIUM ROOMS	= 6 nos.
STANDARD ROOMS	= 59 nos.
TOTAL	= 68 nos.

NOTE:

1. ALL SERVICE AND LIFTS PROVISION TO BE CONSIDERED AS/ LOCAL VENDOR RECOMMENDATIONS.
2. LIFT VENDOR TO BE FINALIZED AS/ CUSTOMIZATION.

DRWING STATUS:

GOOD FOR CONSTRUCTION FOR HOTEL PURPOSE
Date of Issue:- 25/04/2019
Date of Revised:- 25/04/2024

CLIENT:

Innovative Consultants
(A PMC COMPANY)
www.innovativeconsulting.in

PROJECT:


HOTEL AT JALANDHAR (PUNJAB)

NOTE:-
1. This drawing is a COPYRIGHT & PROPERTY of STUDIO ARDETE, and is NOT TO BE REPRODUCED, COPIED, HANDED OVER to third party or used for any other purpose other than for which its intended.
2. While every attempt has been made in the preparation of this drawing and to avoid mistakes the maker cannot guarantee against human error. The contractor on job must check all dimensions and other details and be responsible for the same.

PROJECT TITLE: HOTEL PLANING			
PROJECT NO : HS0010			
DRAWING TITLE : FINAL FIRST FLOOR PLAN			
PURPOSE : TEN ☐ GFC ■ ASB ☐ REV ■			
SCALE:- N.T.S	DRAWN BY:-	CHECKED BY:-	
DATE:- 10/01/2025	ANUKRITI	ANUSHA	
DWG NO-		REVISION:	

ARCHITECTS:

Studio Ardete Pvt. Ltd.
SCO - 43, First Floor, Swastik Vihar, MDC, Panchkula - 134109, Chandigarh (Tricity)
TEL: 0172-4020185
EMAIL: info@studioardete.com

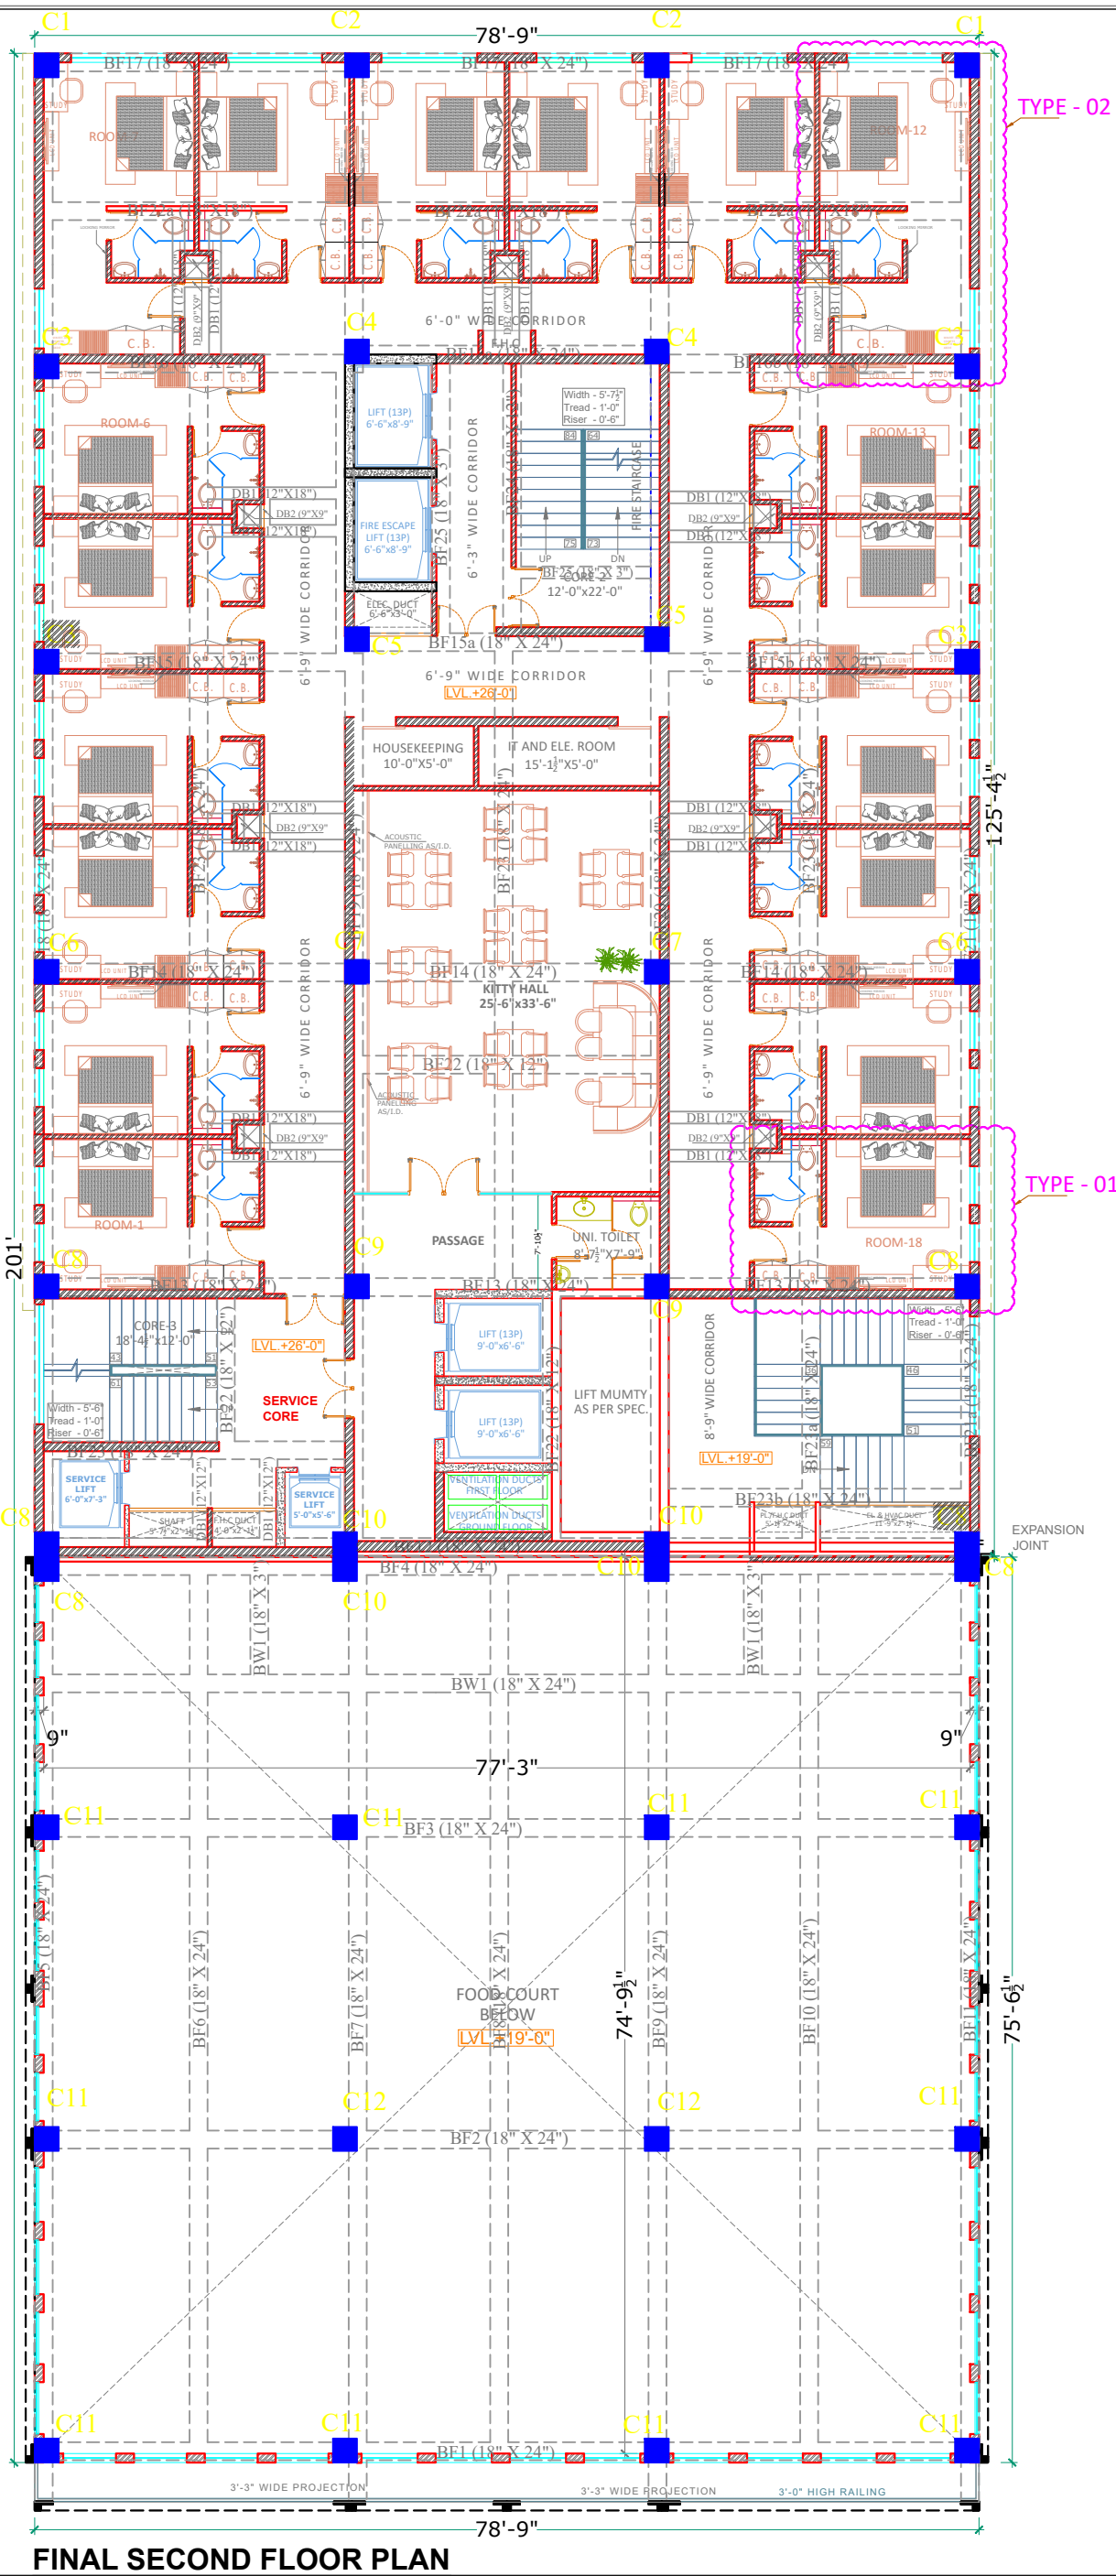

FINAL SECOND FLOOR PLAN

ROOMS INVENTORY:

1. GROUND FLOOR	= 12 Nos.
2. FIRST FLOOR	= 18 Nos.
3. SECOND FLOOR	= 18 Nos.
4. THIRD FLOOR	= 04 Nos.
5. FOURTH FLOOR	= 16 Nos.

TOTAL ROOMS AS PER SITE = 68 Nos.

CONVERTED ROOMS FOR HOTEL:-

SUITE ROOMS (1+1)	**= 3 nos.**
PREMIUM ROOMS	**= 6 nos.**
STANDARD ROOMS	**= 59 nos.**
TOTAL	**= 68 nos.**

NOTE:

1. ALL SERVICE AND LIFTS PROVISION TO BE CONSIDERED AS/ LOCAL VENDOR RECOMMENDATIONS.
2. LIFT VENDOR TO BE FINALIZED AS/ CUSTOMIZATION.

DRWING STATUS:

GOOD FOR CONSTRUCTION FOR HOTEL PURPOSE
Date of Issue:- 25/04/2019
Date of Revised:- 25/04/2024

CLIENT:

Innovative Consultants
(A PMC COMPANY)
www.innovativeconsulting.in


PROJECT:

HOTEL AT JALANDHAR (PUNJAB)

NOTE:- 1. This drawing is a COPYRIGHT & PROPERTY of STUDIO ARDETE, and is NOT TO BE REPRODUCED, COPIED, HANDED OVER to third party or used for any other purpose other than for which its intended.
2. While every attempt has been made in the preparation of this drawing and to avoid mistakes the maker cannot guarantee against human error. The contractor on job must check all dimensions and other details and be responsible for the same.

PROJECT TITLE: HOTEL PLANING		SCALE:- N.T.S	DRAWN BY:- / CHECKED BY:-
PROJECT NO : HS0010		DATE:- 10/01/2025	ANUKRITI / ANUSHA
DRAWING TITLE : SECOND FLOOR PLAN		DWG NO-	REVISION:
PURPOSE :	TEN ☐ GFC ■ ASB ☐ REV ■		

ARCHITECTS:
Studio Ardete Pvt. Ltd.
SCO - 43, First Floor, Swastik Vihar, MDC, Panchkula - 134109, Chandigarh (Tricity)
TEL: 0172-4020185
EMAIL: info@studioardete.com

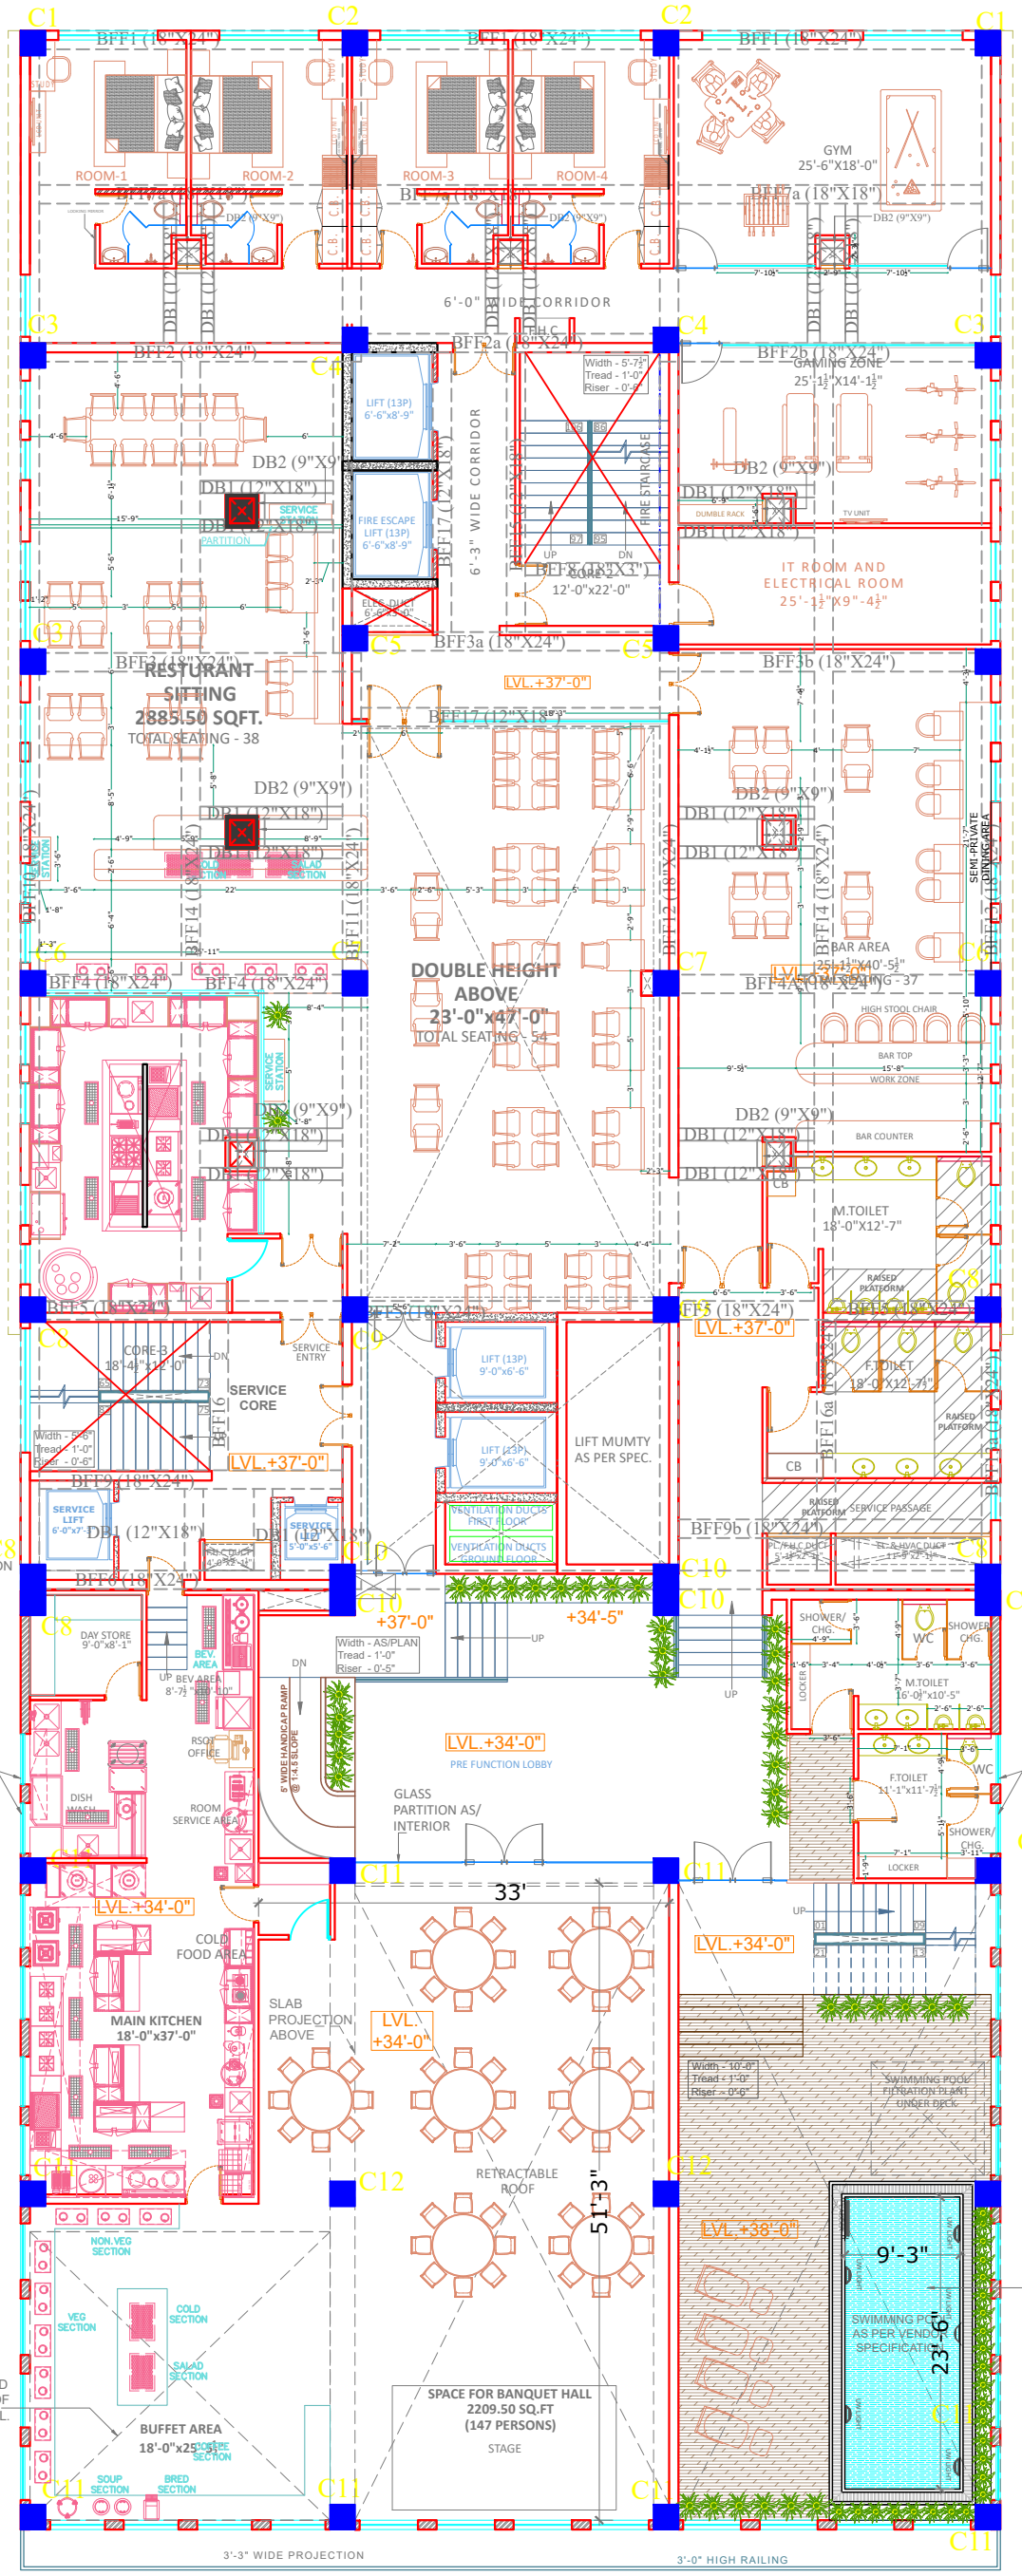

FINAL THIRD FLOOR PLAN

ROOMS INVENTORY:

1. GROUND FLOOR = 12 Nos.
2. FIRST FLOOR = 18 Nos.
3. SECOND FLOOR = 18 Nos.
4. THIRD FLOOR = 04 Nos.
5. FOURTH FLOOR = 16 Nos.

TOTAL ROOMS AS PER SITE = 68 Nos.

CONVERTED ROOMS FOR HOTEL:-
SUITE ROOMS (1+1) = 3 nos.
PREMIUM ROOMS = 6 nos.
STANDARD ROOMS = 59 nos.
TOTAL = 68 nos.


NOTE:
1. ALL SERVICE AND LIFTS PROVISION TO BE CONSIDERED AS/ LOCAL VENDOR RECOMMENDATIONS.
2. LIFT VENDOR TO BE FINALIZED AS/ CUSTOMIZATION.

DRWING STATUS:
GOOD FOR CONSTRUCTION FOR HOTEL PURPOSE
Date of Issue:- 25/04/2019
Date of Revised:- 25/04/2024

CLIENT:
Innovative Consultants
(A PMC COMPANY)
www.innovativeconsulting.in

PROJECT: **HOTEL AT JALANDHAR (PUNJAB)**	NOTE:- 1. This drawing is a COPYRIGHT & PROPERTY of STUDIO ARDETE, and is NOT TO BE REPRODUCED, COPIED, HANDED OVER to third party or used for any other purpose other than for which its intended. 2. While every attempt has been made in the preparation of this drawing and to avoid mistakes the maker cannot guarantee against human error. The contractor on job must check all dimensions and other details and be responsible for the same.	PROJECT TITLE: HOTEL PLANING	SCALE:- N.T.S	DRAWN BY:-	CHECKED BY:-
		PROJECT NO : HS0010	DATE:- 10/01/2025	SANJAY	SANCHIT DHIMAN
		DRAWING TITLE : THIRD FLOOR PLAN	DWG NO-		REVISION:
		PURPOSE : TEN ☐ GFC ■ ASB ☐ REV ■			

ARCHITECTS:
Studio Ardete Pvt. Ltd.
SCO - 43, First Floor, Swastik Vihar, MDC, Panchkula - 134109, Chandigarh (Tricity)
TEL: 0172-4020185
EMAIL: info@studioardete.com

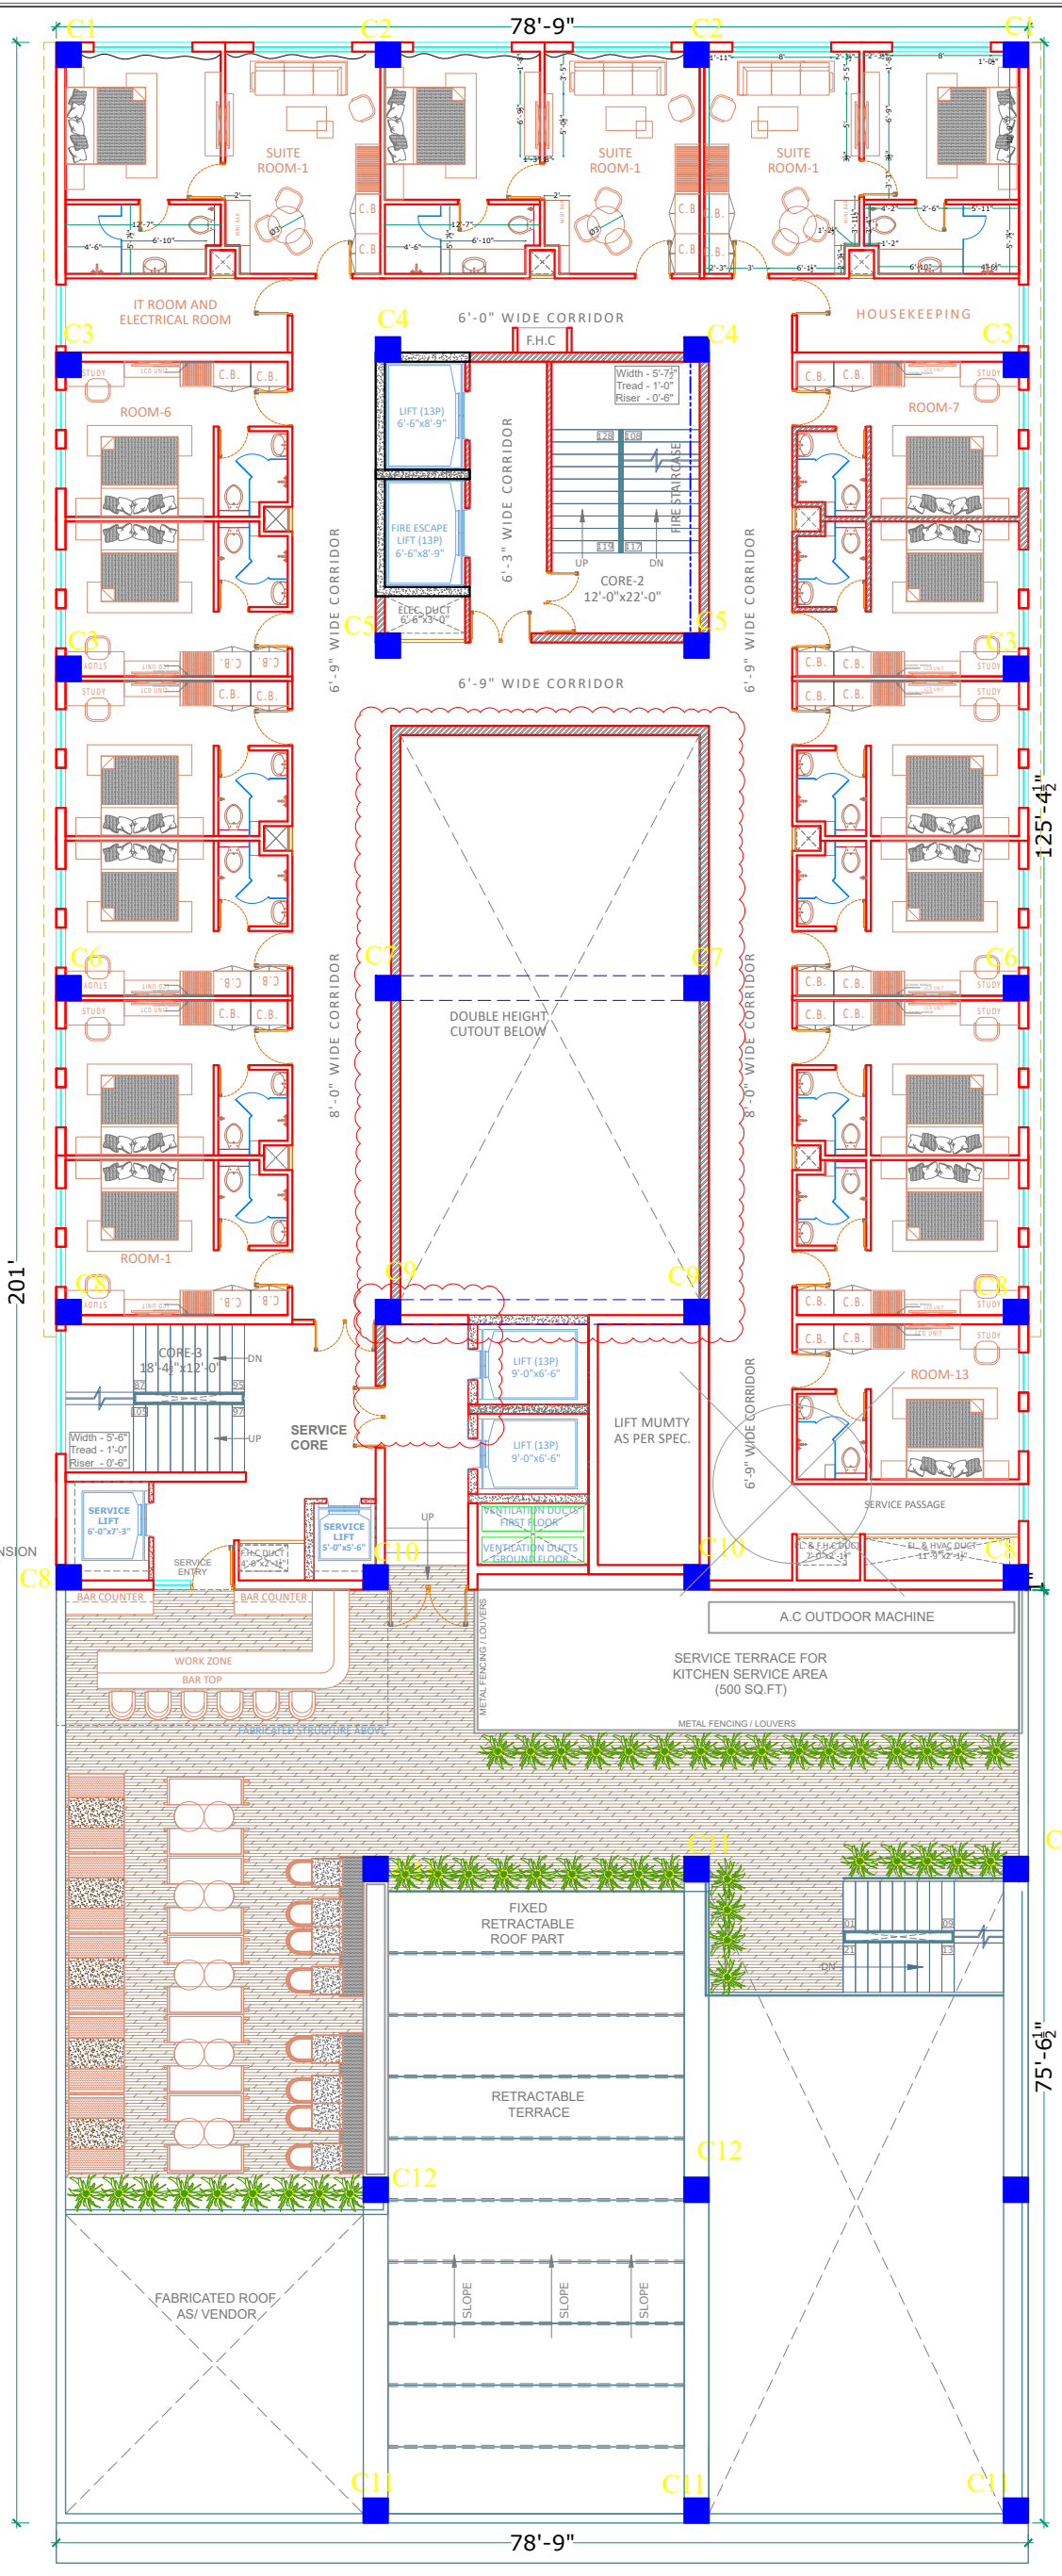

FINAL FOURTH FLOOR PLAN

ROOMS INVENTORY:

1. GROUND FLOOR	= 12 Nos.
2. FIRST FLOOR	= 18 Nos.
3. SECOND FLOOR	= 18 Nos.
4. THIRD FLOOR	= 04 Nos.
5. FOURTH FLOOR	= 16 Nos.

TOTAL ROOMS AS PER SITE = 68 Nos.

CONVERTED ROOMS FOR HOTEL:-

SUITE ROOMS (1+1)	**= 3 nos.**
PREMIUM ROOMS	**= 6 nos.**
STANDARD ROOMS	**= 59 nos.**
TOTAL	**= 68 nos.**

NOTE:

1. ALL SERVICE AND LIFTS PROVISION TO BE CONSIDERED AS/ LOCAL VENDOR RECOMMENDATIONS.
2. LIFT VENDOR TO BE FINALIZED AS/ CUSTOMIZATION.

DRWING STATUS:

GOOD FOR CONSTRUCTION FOR HOTEL PURPOSE
Date of Issue:- 25/04/2019
Date of Revised:- 25/04/2024

CLIENT:

Innovative Consultants
(A PMC COMPANY)
www.innovativeconsulting.in


PROJECT:

HOTEL AT JALANDHAR (PUNJAB)

NOTE:- 1. This drawing is a COPYRIGHT & PROPERTY of STUDIO ARDETE, and is NOT TO BE REPRODUCED, COPIED, HANDED OVER to third party or used for any other purpose other than for which its intended.
2. While every attempt has been made in the preparation of this drawing and to avoid mistakes the maker cannot guarantee against human error. The contractor on job must check all dimensions and other details and be responsible for the same.

PROJECT TITLE: HOTEL PLANING		SCALE:- N.T.S	DRAWN BY:- / CHECKED BY:-
PROJECT NO : HS0010		DATE:- 10/01/2025	ANUKRITI / ANUSHA
DRAWING TITLE : FOURTH FLOOR PLAN		DWG NO-	REVISION:
PURPOSE :	TEN ☐ GFC ■ ASB ☐ REV ■		

ARCHITECTS:
Studio Ardete Pvt. Ltd.
SCO - 43, First Floor, Swastik Vihar, MDC, Panchkula - 134109, Chandigarh (Tricity)
TEL: 0172-4020185
EMAIL: info@studioardete.com

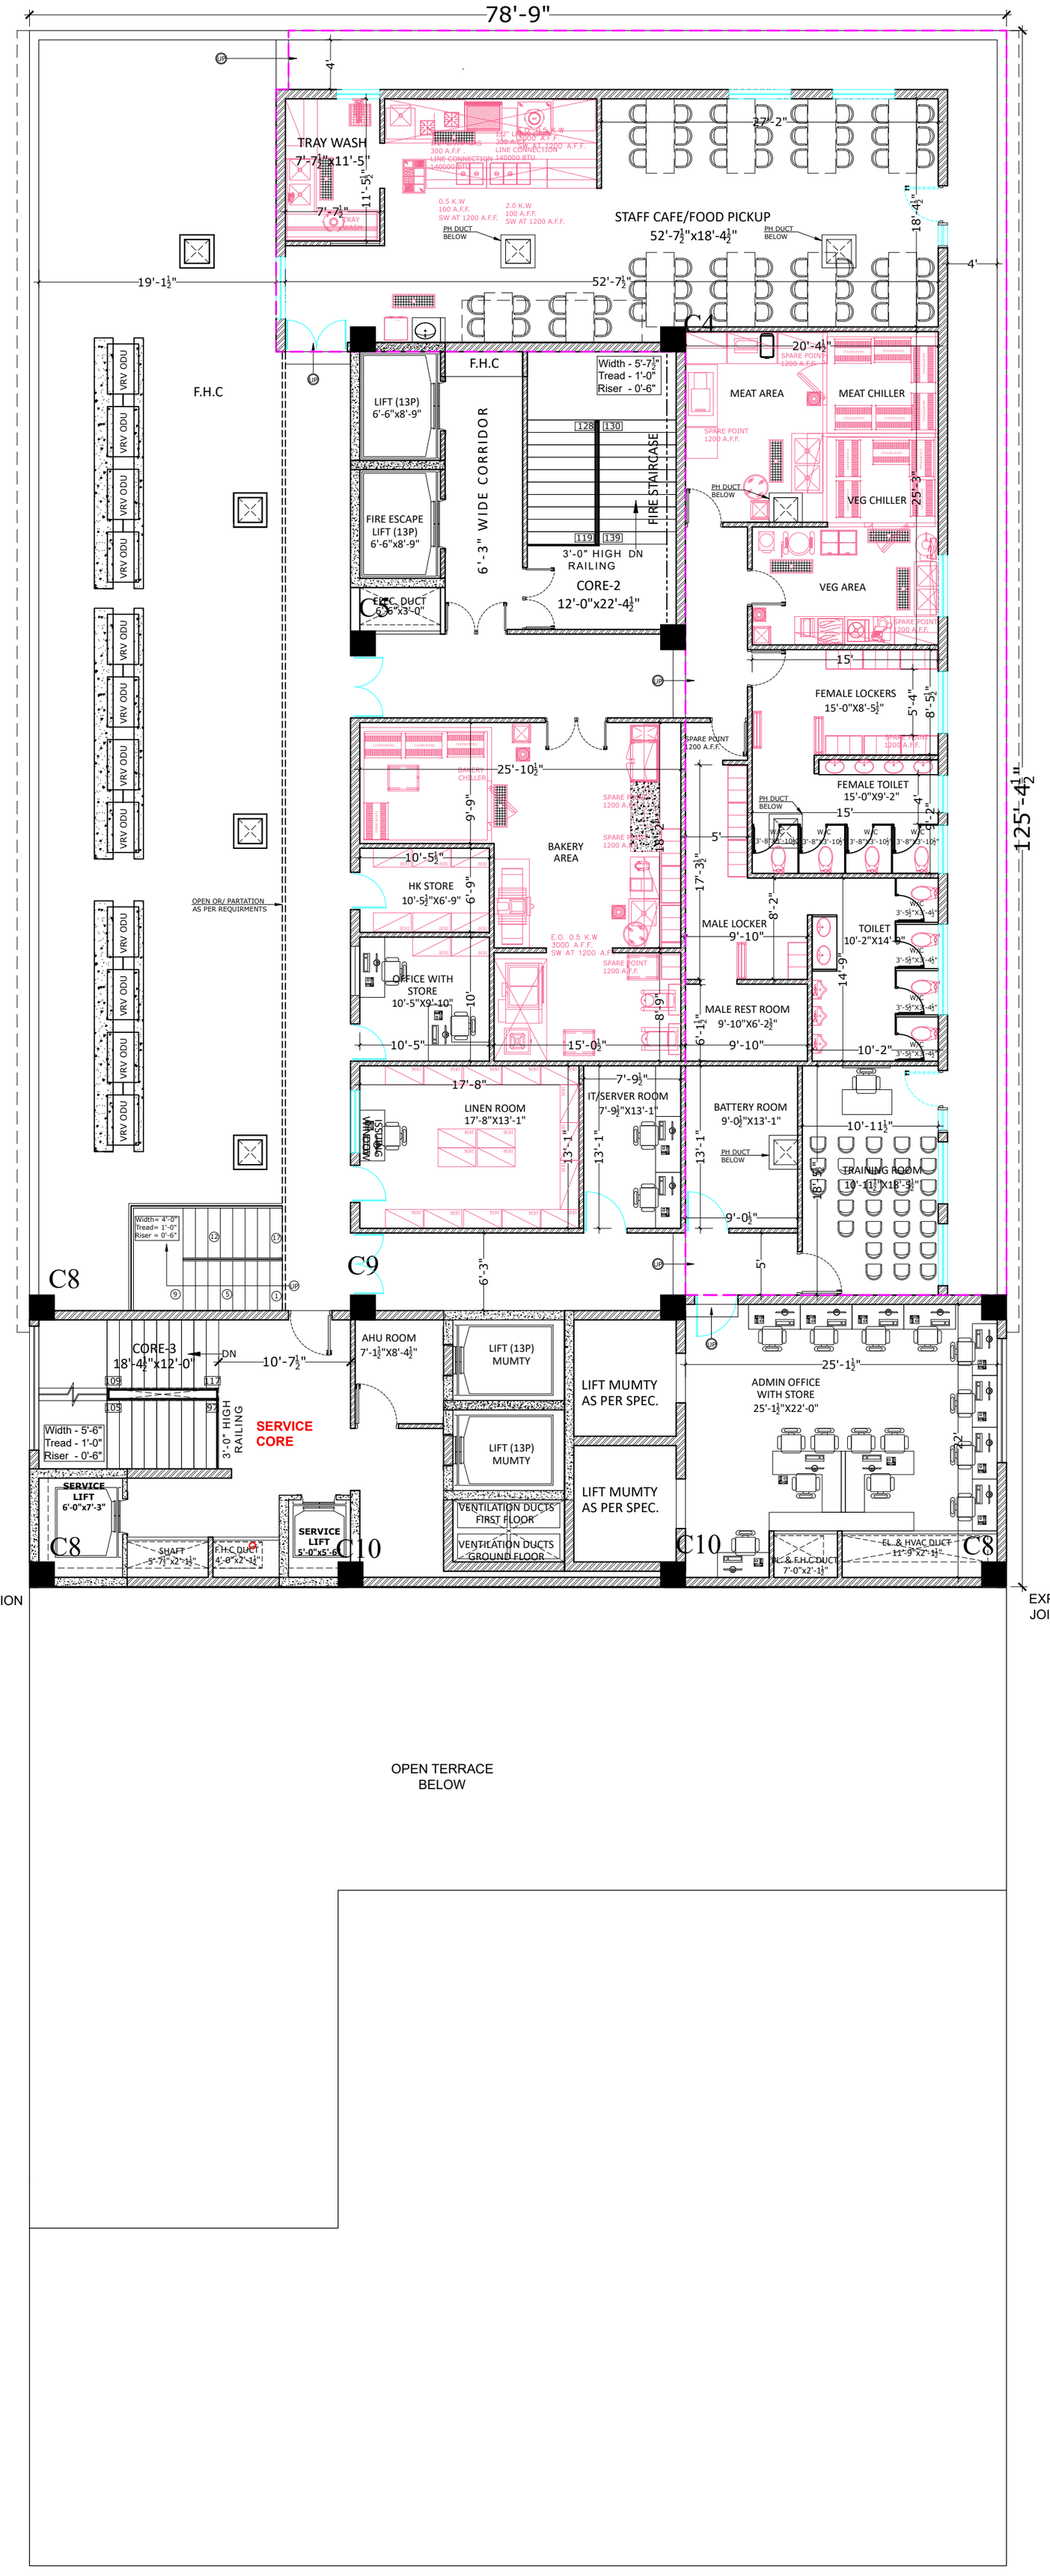

NOTE:

1. ALL SERVICE AND LIFTS PROVISION TO BE CONSIDERED AS/ LOCAL VENDOR RECOMMENDATIONS.
2. LIFT VENDOR TO BE FINALIZED AS/ CUSTOMIZATION.

DRWING STATUS:

GOOD FOR CONSTRUCTION FOR HOTEL PURPOSE

Date of Issue:- 25/04/2019

Date of Revised:- 25/04/2024

CLIENT:

Innovative Consultants
(A PMC COMPANY)
www.innovativeconsulting.in

PROJECT:

HOTEL AT JALANDHAR (PUNJAB)

NOTE:- 1. This drawing is a COPYRIGHT & PROPERTY of STUDIO ARDETE, and is NOT TO BE REPRODUCED, COPIED, HANDED OVER to third party or used for any other purpose other than for which its intended.
2. While every attempt has been made in the preparation of this drawing and to avoid mistakes the maker cannot guarantee against human error. The contractor on job must check all dimensions and other details and be responsible for the same.

PROJECT TITLE: HOTEL PLANING
PROJECT NO : HS0010
DRAWING TITLE : TERRACE PLAN
PURPOSE : TEN ☐ GFC ■ ASB ☐ REV ■

SCALE:- N.T.S | DRAWN BY:- MAYURESH SHELKE | CHECKED BY:- SANCHIT DHIMAN
DATE:- 09/12/2024 | DWG NO- | REVISION:

ARCHITECTS:
Studio Ardete Pvt. Ltd.
SCO - 43, First Floor, Swastik Vihar, MDC, Panchkula - 134109, Chandigarh (Tricity)
TEL: 0172-4020185
EMAIL: info@studioardete.com

CE FOR
RKING
-6"

SPACE FOR
HOTEL GAS
BANK STORAGE
(CYLINDERS PLACED
IN DOUBLE STACK
20 NO.)

SPACE FOR FOOD
COURT GAS BANK
STORAGE
(CYLINDERS PLACED
IN DOUBLE STACK
20 NO.)

FENCING
40'-11"
5'

PLATFORM FOR
TRANSFORMERS
LVL.+1'-5"

HT ROOM
LVL.+1'-5"

MUMTY

49'-4" [15.03]
49'-2½" [15.00]
LVL.+0'-6"

STP BELOW

PLATFORM FOR
D.G SETS
LVL.+1'-5"

60'
4'-0" HIGH CONC.
PARAPET WALL
19'-8" WIDE RAMP UP TO
GROUND LEVEL @ SLOPE - 1:10
UP
20' [6.09]
19'-8" [6.00]
LVL.-6'-0"

78'-9"
C1 C2 C2 C1

20'-9" [6.32]
20'-7" [6.27]
ROOM-3
ROOM-6
STUDY
LCD UNIT
C.B.

10'
10'-9"
LVL.+0'-6"

C3 C4 6'-0" WIDE CORRIDOR C4 C3

M.TOILET
12'-10"X13'-9"
F.TOILET
11'6½"X13'-9"
LIFT (13P)
6'-6"x8'-9"
FIRE ESCAPE
LIFT (13P)
6'-6"x8'-9"
Width - 5'-7"
Tread - 1'-0"
Riser - 0'-6"
FIRE STAIRCASE
UP DN
CORE-2
12'-0"x22'-0"
6'-3" WIDE CORRIDOR
ROOM-7
HANDICAP
TOILET
10'-4"X11'-0"
ANITORY CLOSET
ESC. DUCT
6'-4"x3'-0"
SCULPTURE/ART
INSTALLATION
C3 C5 C5 C3
BAGGAGE
SCANNER
FRONT OFFICE
8'-7½"X11'-0"
RAMP DN
BASEMENT LINE
WATER BODY
PORCH
LVL.+3'-0"
ENT.FOYER
HOTEL LOBBY
LVL.+4'-0"
RECEPTION
BACK COUNTER
6'-9" WIDE CORRIDOR
C6 GLASS PARTITION C7 C7 C6
SCULPTURE/ART
INSTALLATION
LUGGAGE
ROOM
8'-7½"X8'-4½"
RACK
CONSOLE
20'-7" WIDE RAMP UP TO
GROUND LEVEL @ SLOPE - 1:10
UP
125'-4½"
LVL.-11'-0"
330'-4"
294'-6½"
WAITING AREA
C8 C9 C9 C8
COFFEE CONSOLE
MANAGER
OFFICE
8'-7½"X11'-11"
ROOM-12
RAMP UP
LVL.+0'-6"
UP DN
CORE-3
14'-6"X12'-0"
LVL.+4'-0"
SERVICE
CORE
METAL
BRIDGE
LIFT (13P)
9'-0"x6'-6"
LIFT (15P)
7'-0"x9'-3"
LIFT (13P)
9'-0"x6'-6"
FIRE ESCAPE
LIFT (15P)
7'-0"x9'-3"
VENTILATION DUCTS
FIRST FLOOR
VENTILATION DUCTS
GROUND FLOOR
8'-9" WIDE CORRIDOR
Width - 5'-6"
Tread - 1'-0"
Riser - 0'-6"
CORE-1
18'-0"x17'-0"
SERVICE
LIFT
6'-0"x7'-3"
SERVICE
LIFT
5'-0"x5'-6"
SHAFT
2'-3½"x2'-9½"
SHAFT
6'-6"x2'-4½"
C8 C10 C10 C10 C10 C8
EXPANSION
JOINT
EXPANSION
JOINT
VENTILATION DUCTS
GROUND FLOOR
9"
C11 C11 C11 C11
25'-4½"
51'-1½"
9"
76'-6"
75'-6½"
LVL.+4'-0"
FOOD COURT
SITTING AREA
C11 C12 C12 C11
LVL.+0'-6"
C11 C11 C11 C11
BOOM BARRIER
(FOR HOTEL ENTRY)
LVL.+4'-0"
3'-3" WIDE CORRIDOR
LVL.+4'-0"
3'-3" WIDE PROJECTION ABOVE
20'-6½" [6.26]
3'-3"
20'-6½" WIDE RAMP DN TO
BASEMENT @SLOPE - 1:10
107'
6'-0" HIGH BOUNDARY
WALL
20'-9" WIDE FIRE TENDER MOVEMENT
BASEMENT LINE
6'-0" HIGH BOUNDARY
WALL
329'-11½"
365'-5½" [111.39]

5'-0" WIDE VERANDAH
Width - 24'-9"
Tread - 1'-0"
Riser - 0'-6"
28'-9"
25'
5'
5'

FINAL GROUND FLOOR PLAN

UP
5'-0" WIDE DISABLED
RAMP @ SLOPE - 1:5.70
20'-8½"
5'-0½"
6'
PLANTER
PLANTER
16'
2'
24'-9"
2'
30'-5½"
5'-3"
GUARD BOOK
TOE WALL
4'-4½"
10'-2½"
8'
8'
8'
6MT SETBACK LINE
LVL.+0'-6"
42'-7"
38'-11½"
34'
ENTRY
EXIT
LVL.+0'-6"
LVL.+0'-6"
BASEMENT LINE
PLOT LINE
82'-2"
22'-9 1/2" WIDE STRIP FOR ROAD WIDENING
11'-9½"
8'-9½"
METER
ROOM
BOX
EXHAUST FAN
5'-3"
20'-6½"
31'-11"
2'-7½"
24'-10"
LVL.±0'-0"

FINAL SITE LAYOUT PLAN

NOTE:
1. ALL SERVICE AND LIFTS PROVISION TO BE CONSIDERED AS/ LOCAL VENDOR RECOMMENDATIONS.
2. LIFT VENDOR TO BE FINALIZED AS/ CUSTOMIZATION.

DRWING STATUS:

GOOD FOR CONSTRUCTION FOR HOTEL PURPOSE
Date of Issue:- 25/04/2019
Date of Revised:- 25/04/2024

CLIENT:

Innovative Consultants
(A PMC COMPANY)
www.innovativeconsulting.in


PROJECT:

HOTEL AT JALANDHAR (PUNJAB)

NOTE:- 1. This drawing is a COPYRIGHT & PROPERTY of STUDIO ARDETE, and is NOT TO BE REPRODUCED, COPIED, HANDED OVER to third party or used for any other purpose other than for which its intended.
2. While every attempt has been made in the preparation of this drawing and to avoid mistakes the maker cannot guarantee against human error. The contractor on job must check all dimensions and other details and be responsible for the same.

PROJECT TITLE: HOTEL PLANING			
PROJECT NO : HS0010			
DRAWING TITLE : FINAL SITE LAYOUT PLAN			
PURPOSE : TEN ☐ GFC ■ ASB ☐ REV ■	SCALE:- N.T.S	DRAWN BY:-	CHECKED BY:-
	DATE:- 13/06/2024	NITIN SHARMA	SANCHIT DHIMAN
	DWG NO-		REVISION:

ARCHITECTS:
Studio Ardete Pvt. Ltd.
SCO - 43, First Floor, Swastik Vihar, MDC, Panchkula - 134109, Chandigarh (Tricity)
TEL: 0172-4020185
EMAIL: info@studioardete.com

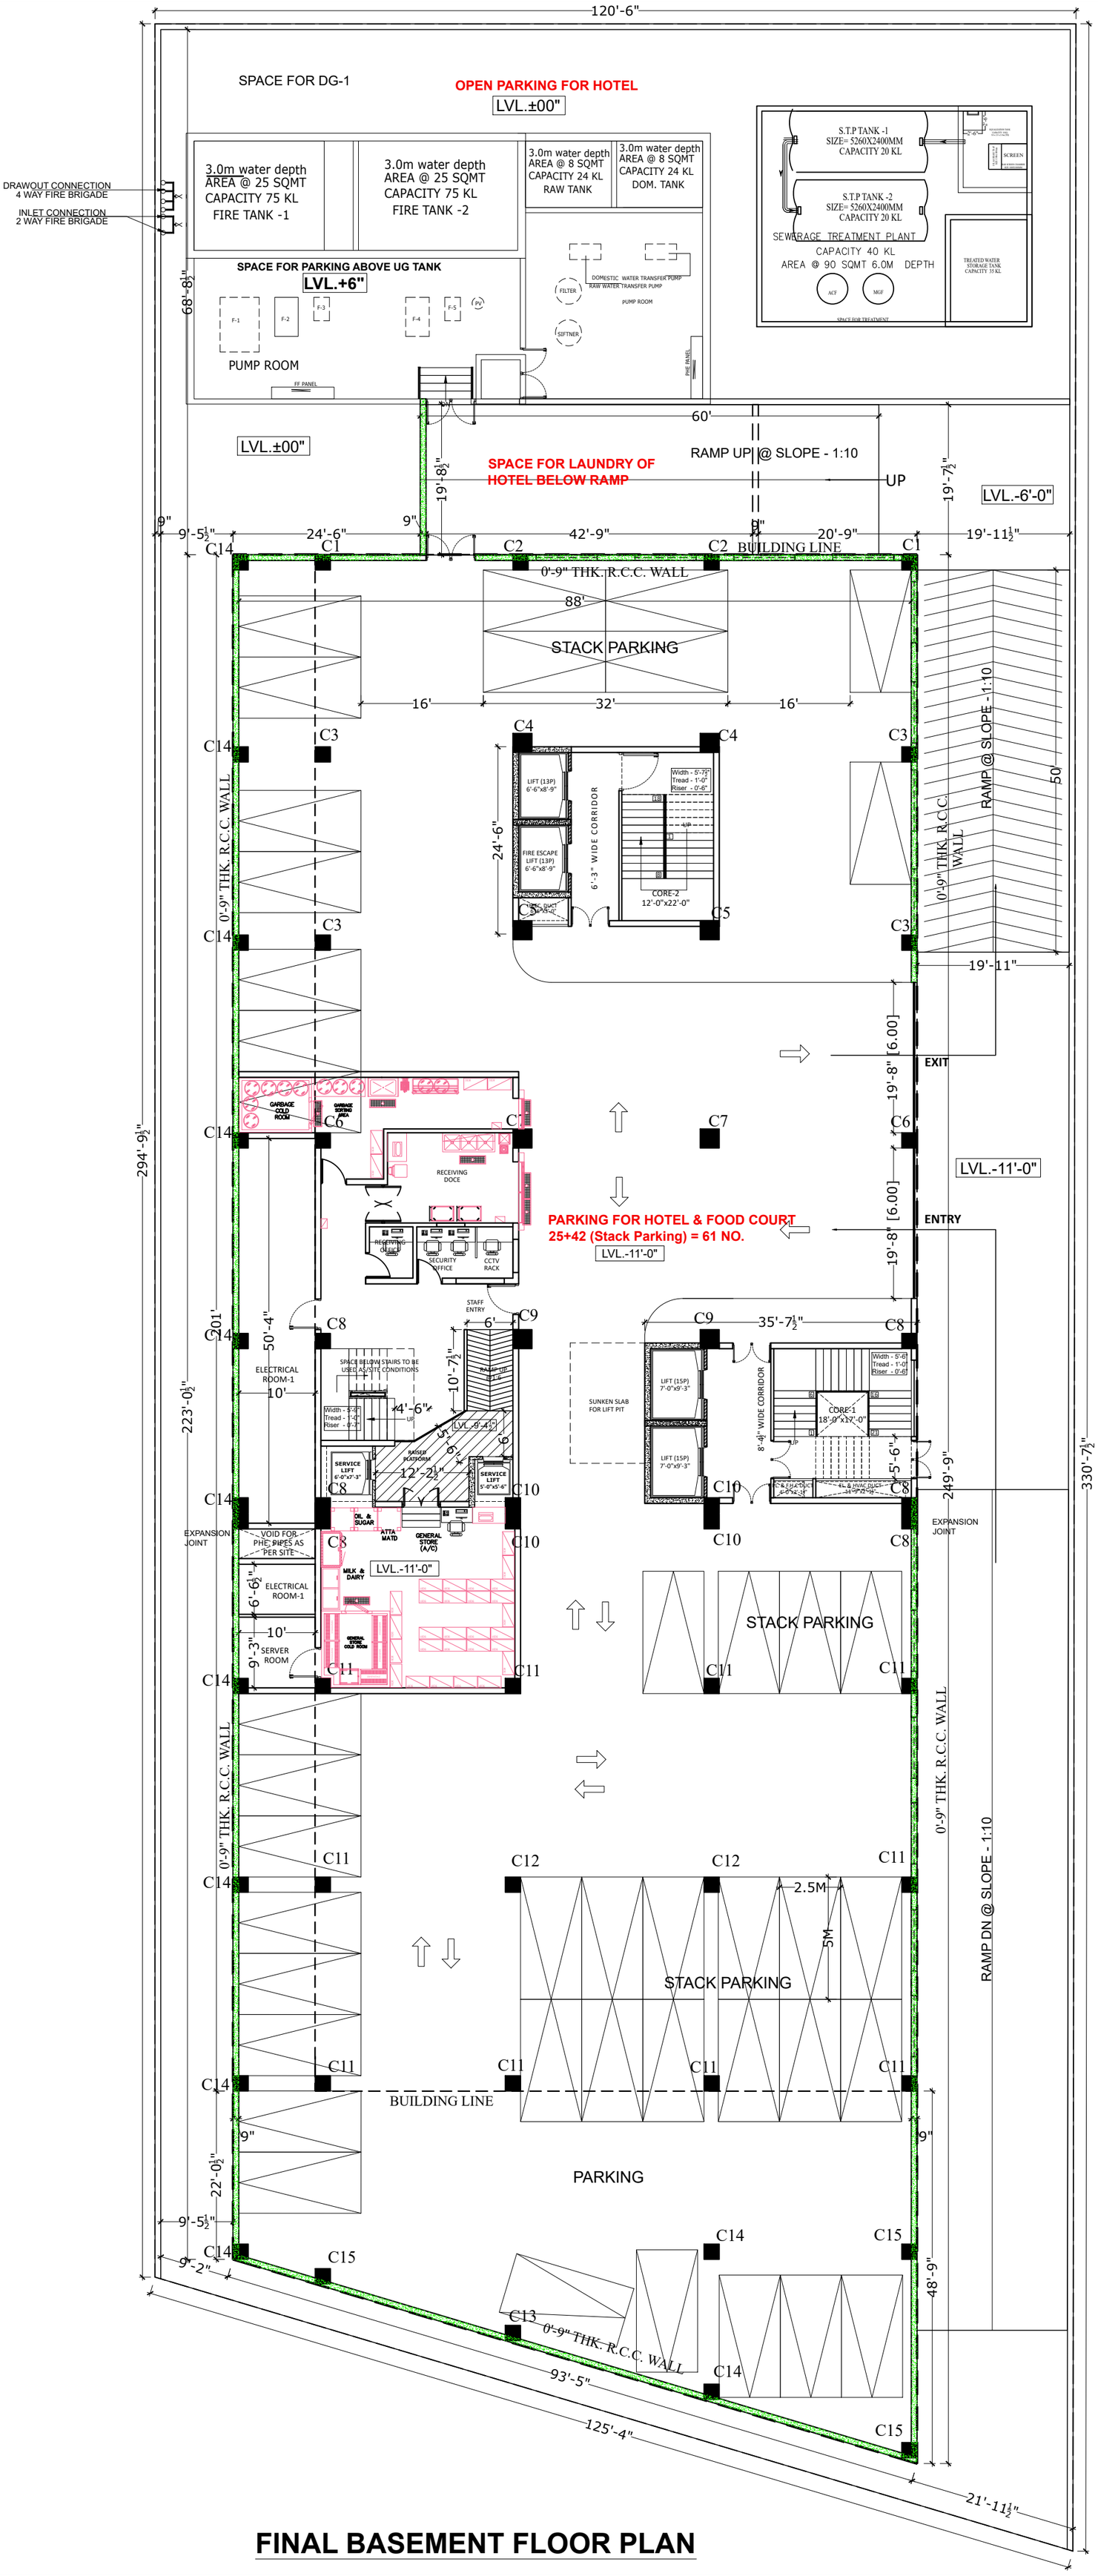

FINAL BASEMENT FLOOR PLAN

NOTE:

1. ALL SERVICE AND LIFTS PROVISION TO BE CONSIDERED AS/ LOCAL VENDOR RECOMMENDATIONS.
2. LIFT VENDOR TO BE FINALIZED AS/ CUSTOMIZATION.

DRWING STATUS:

GOOD FOR CONSTRUCTION FOR HOTEL PURPOSE

Date of Issue:- 25/04/2019

Date of Revised:- 25/04/2024

CLIENT:

Innovative Consultants
(A PMC COMPANY)
www.innovativeconsulting.in

PROJECT:

HOTEL AT JALANDHAR (PUNJAB)

NOTE:- 1. This drawing is a COPYRIGHT & PROPERTY of STUDIO ARDETE, and is NOT TO BE REPRODUCED, COPIED, HANDED OVER to third party or used for any other purpose other than for which its intended.
2. While every attempt has been made in the preparation of this drawing and to avoid mistakes the maker cannot guarantee against human error. The contractor on job must check all dimensions and other details and be responsible for the same.

PROJECT TITLE: HOTEL PLANING
PROJECT NO : HS0010
DRAWING TITLE : FINAL BASEMENT FLOOR PLAN
PURPOSE : TEN ☐ GFC ■ ASB ☐ REV ■

SCALE:- N.T.S | DRAWN BY:- | CHECKED BY:-
DATE:- 16/09/2024 | SANJAY DHIMAN | SANCHIT DHIMAN
DWG NO- | REVISION:

ARCHITECTS:
Studio Ardete Pvt. Ltd.
SCO - 43, First Floor, Swastik Vihar, MDC, Panchkula - 134109, Chandigarh (Tricity)
TEL: 0172-4020185
EMAIL: info@studioardete.com