


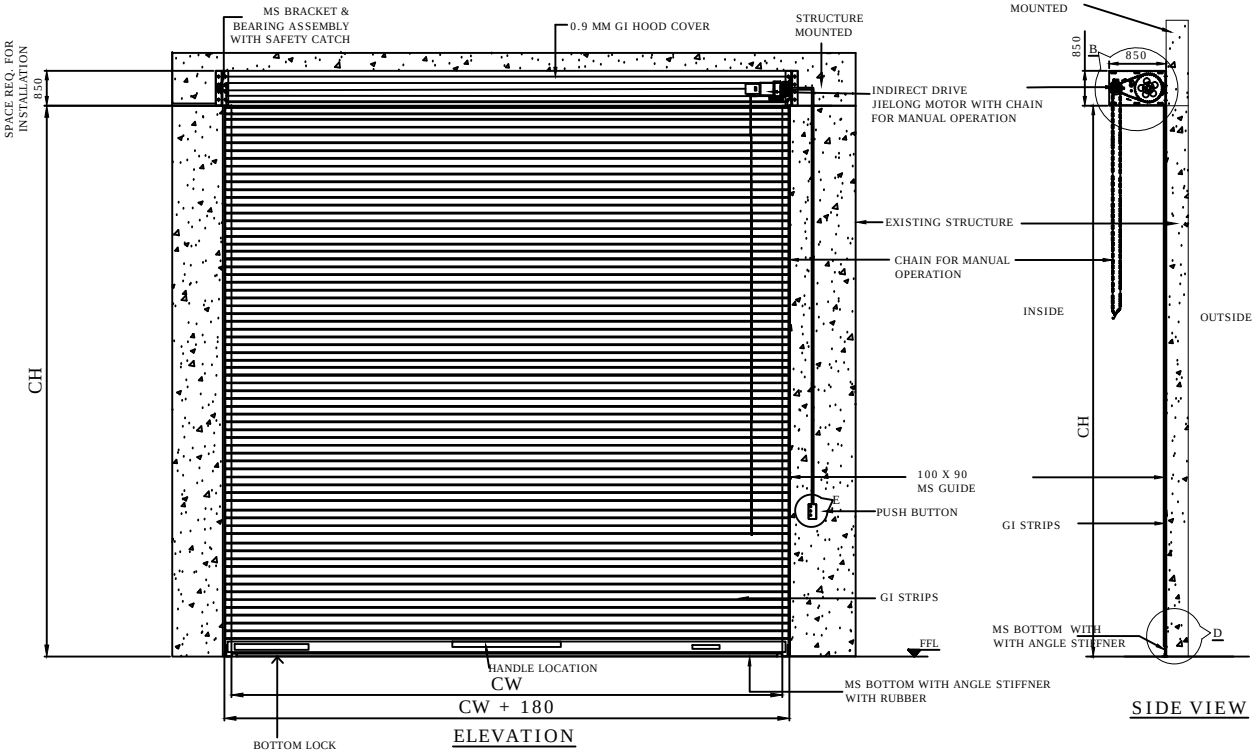


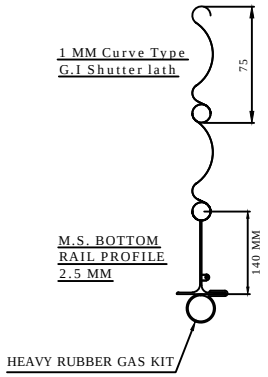


DETAILS : D

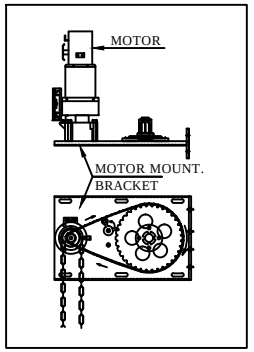


DETAILS : A & B

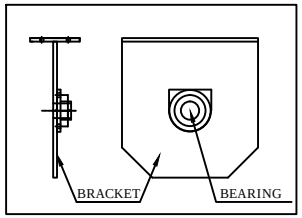

DETAILS : C

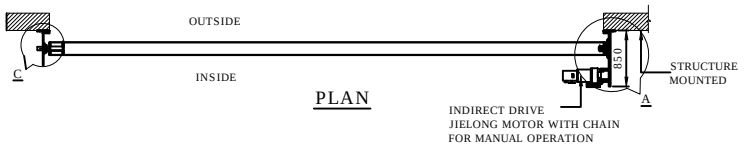

PLAN

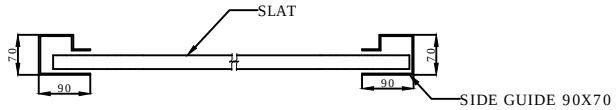

6000	6200	2	RAL -
6000	8200	4	RAL -
CLEAR WIDTH (CW)	CLEAR HEIGHT (CH)	QUANTITY	RAL COLOR POWDER COATING

This drawing & design is the property of NIHVA TECHNOLOGIES. Not to be sold or copied to any other concern.

TITLE: MOTORIZED ROLLING SHUTTER

NIHVA TECHNOLOGIES PVT. LTD.

NIHVA TECHNOLOGIES PVT. LTD. PUNE
Tel : 020 66304033
Email:- info@nihva.com
Website:- www.nihva.com

	NAME	SIGN	DATE
DRAWN	S.M.S.		28.10.2020
CHECK	P.V.A.		28.10.2020
APPRD.			

CLIENT -

PROJECT -

SITE LOCATION -

If any queries contact : projectsupport@nihva.com

DWG. NO. : NIHVA/20-21/0069 REV- R00

ALL DIMENSION ARE IN mm

SCALE: NTS WT: SHEET: