

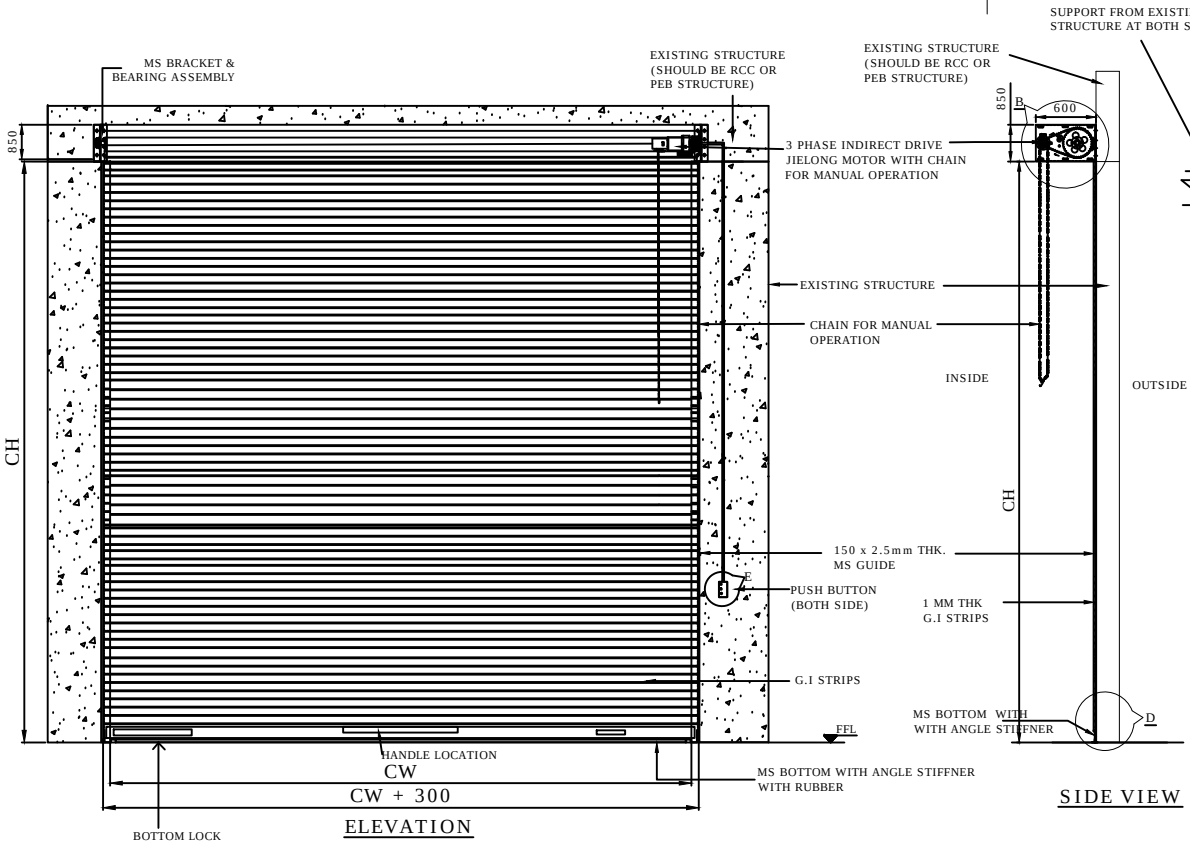


ELEVATION


SIDE VIEW

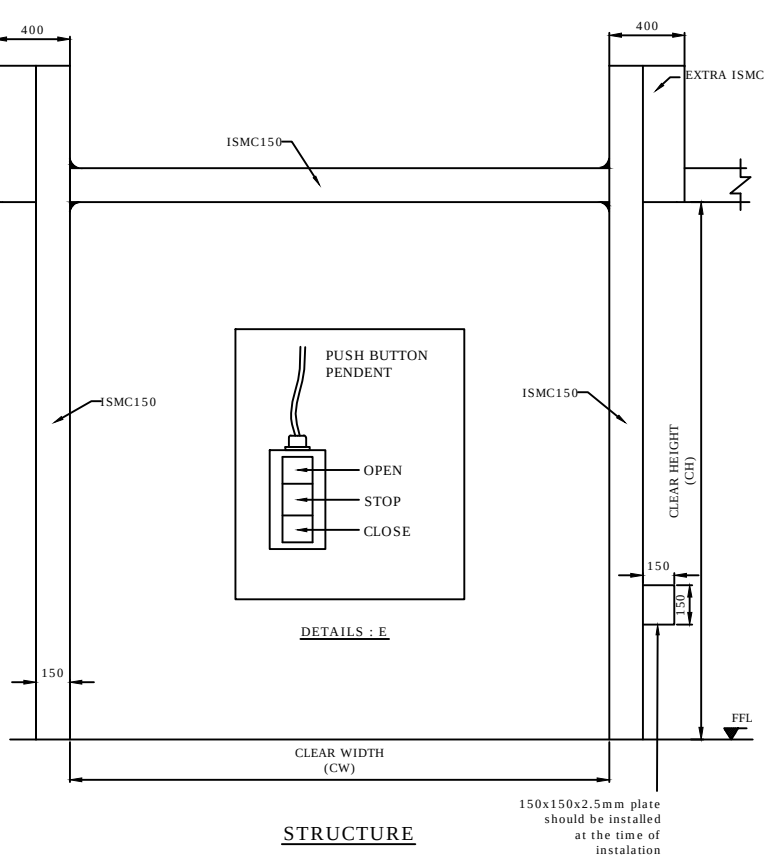


STRUCTURE

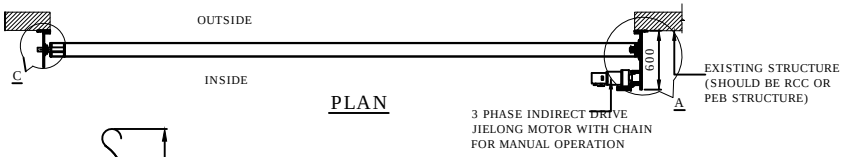


PLAN

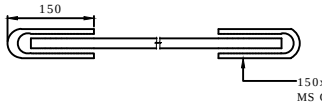


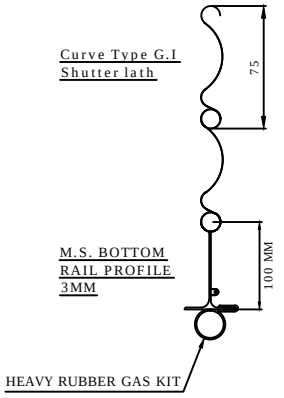

DETAILS : D

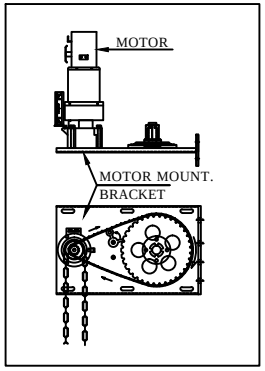

DETAILS : A & B

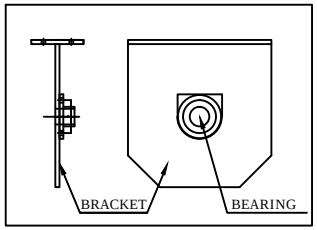

DETAILS : C

(NOTE: REQUIRED TECHANICAL STRUCTURE FOR SHUTTER IN CLIENT SCOPE)

CLEAR WIDTH (CW)	CLEAR HEIGHT (CH)	QUANTITY	RAL COLOR	LOCATION
4000	5000	4	RAL - 9006	TCL - 3
3000	5000	7	RAL - 9006	TCL - 3

This drawing & design is the property of NIHVA TECHNOLOGIES. Not to be sold or copied to any other concern.

TITLE: MOTORIZED ROLLING SHUTTER

	NAME	SIGN	DATE
DRAWN	P.V.A		23.10.2019
CHECK	V.M.T		23.10.2019
APPRD.			

NIHVA TECHNOLOGIES PVT. LTD.
NIHVA TECHNOLOGIES PVT. LTD. PUNE
Tel : 020 66304033
Email:- info@nihva.com
Website:- www.nihva.com

CLIENT -

PROJECT -

SITE LOCATION -

If any queries contact : design@nihva.com

DWG. NO. : NIHVA/19-20/VDR/191

REV- R01

ALL DIMENSION ARE IN mm

SCALE: NTS

WT:

SHEET: