Revision		Date	By
A	Corrected mullion hoist positions, floor pits altered	2022-09-02	EB
B	New measurements, doors redrawn	2022-10-11	EB

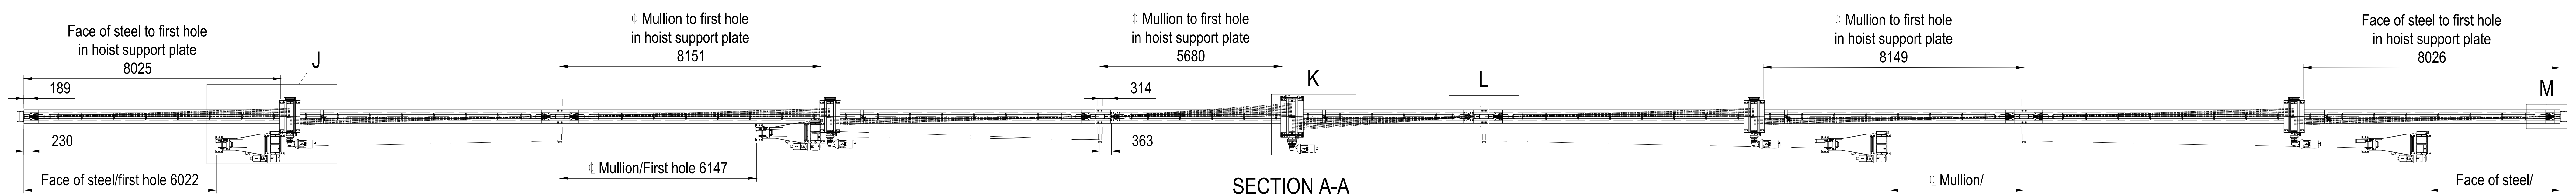

SECTION A-A

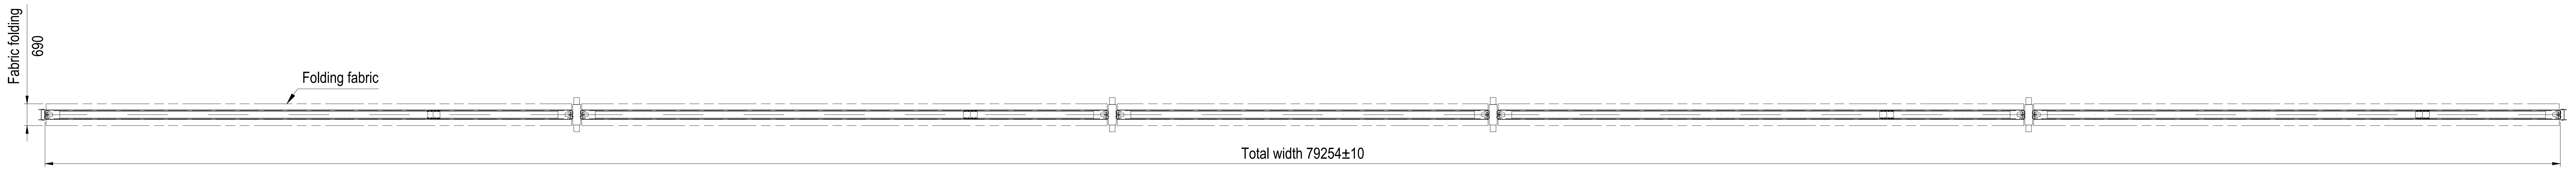

SECTION B-B

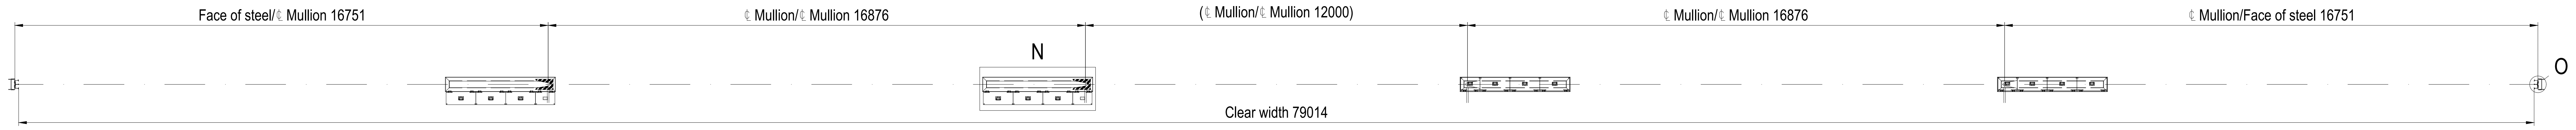
Face of steel/℄ Mullion 16751
℄ Mullion/℄ Mullion 16876
(℄ Mullion/℄ Mullion 12000)
℄ Mullion/℄ Mullion 16876
℄ Mullion/Face of steel 16751
N
O
Clear width 79014

SECTION C-C

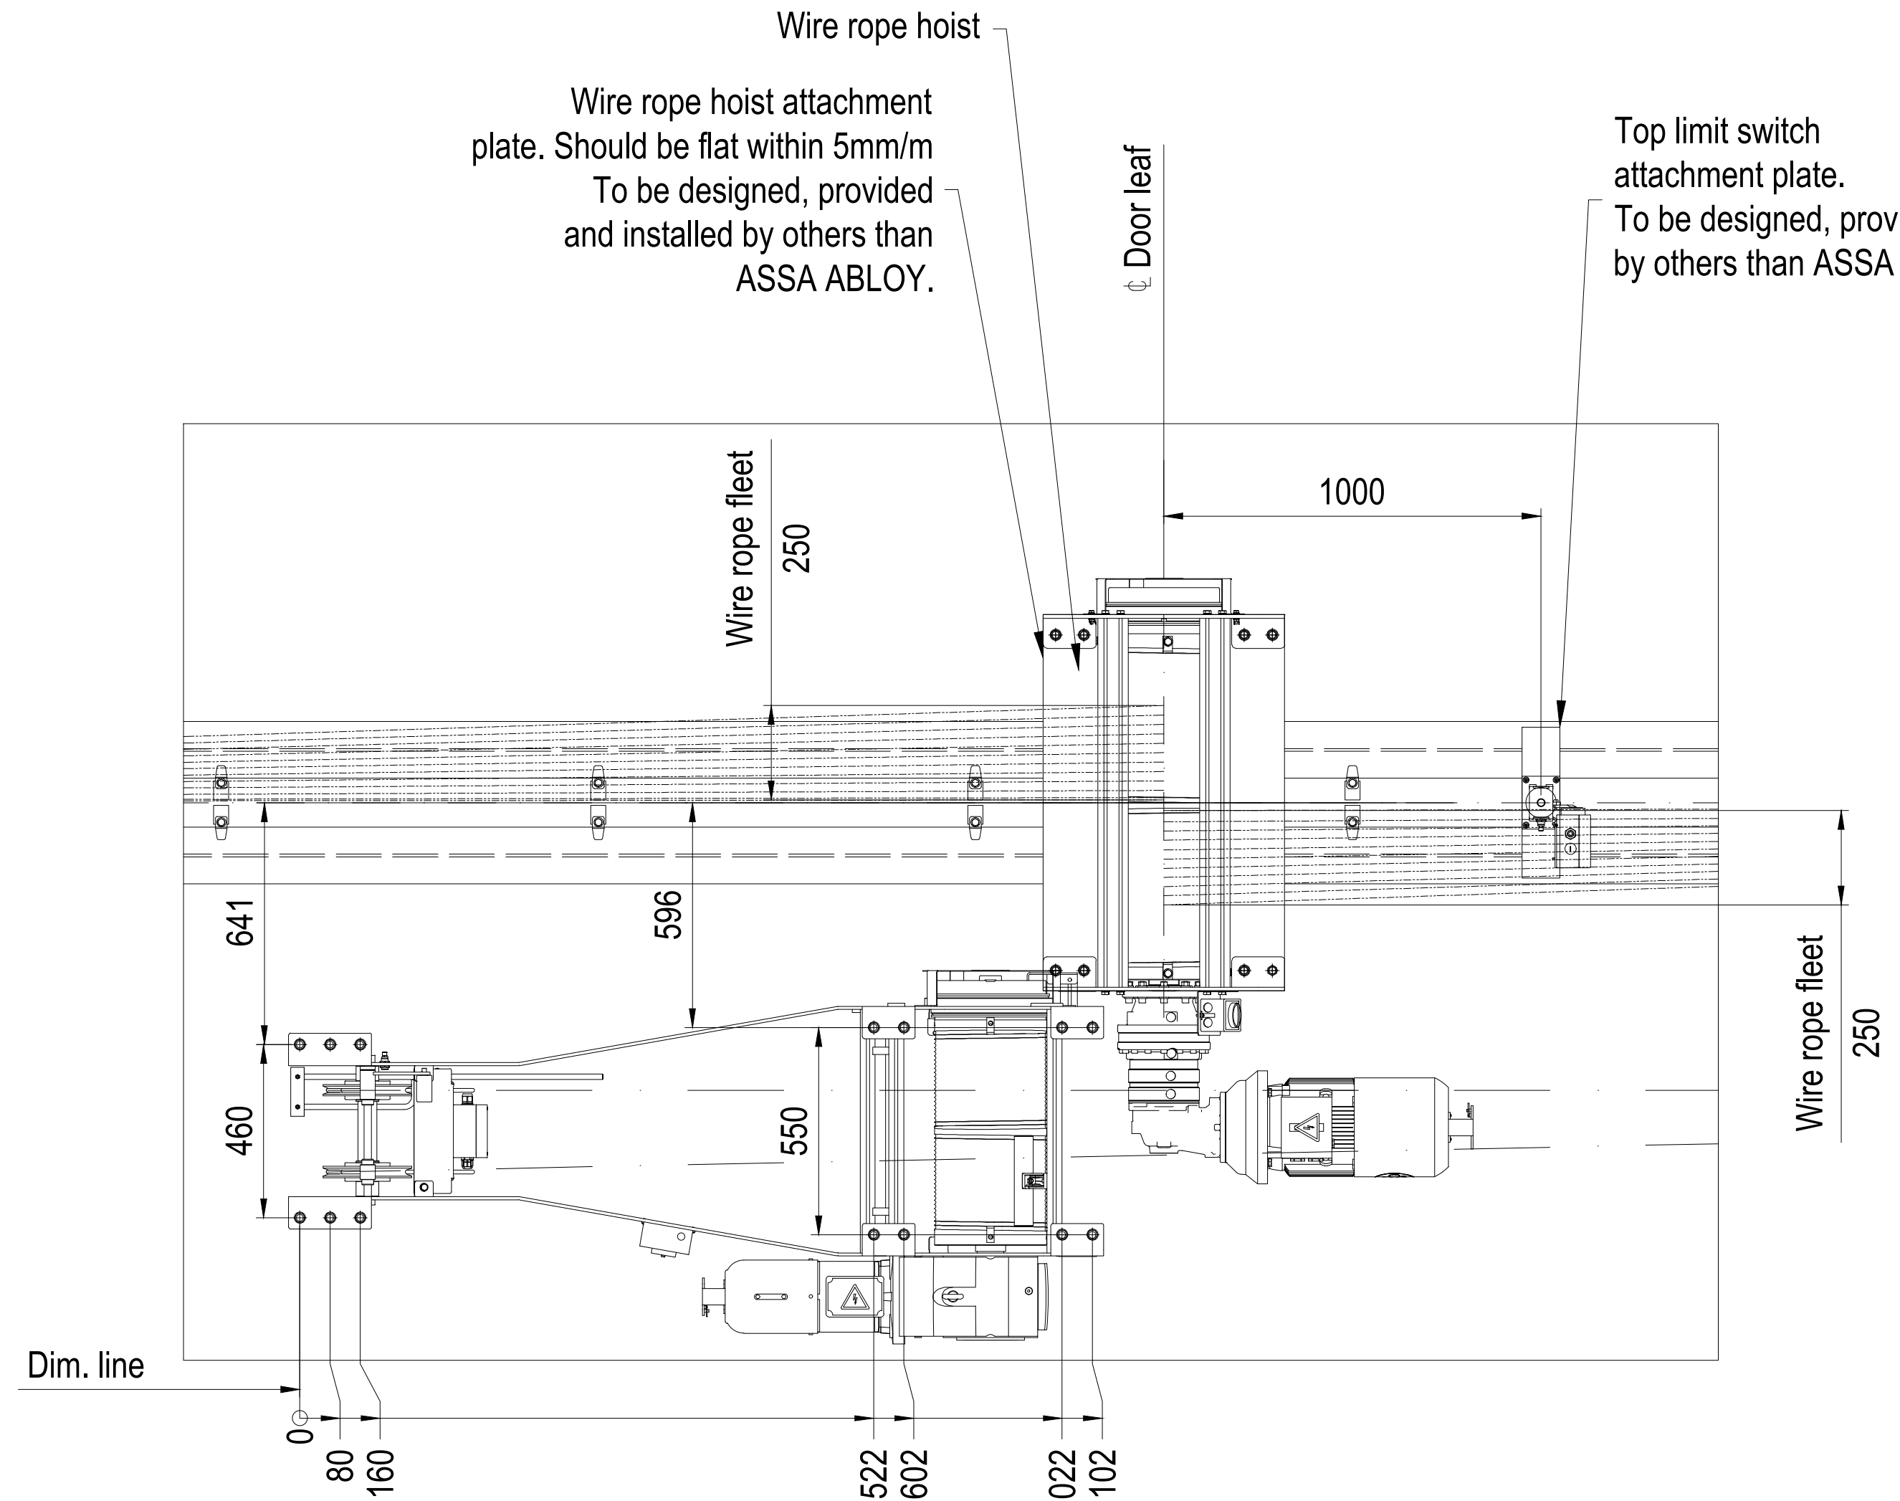

DETAIL J, SCALE (1:20)

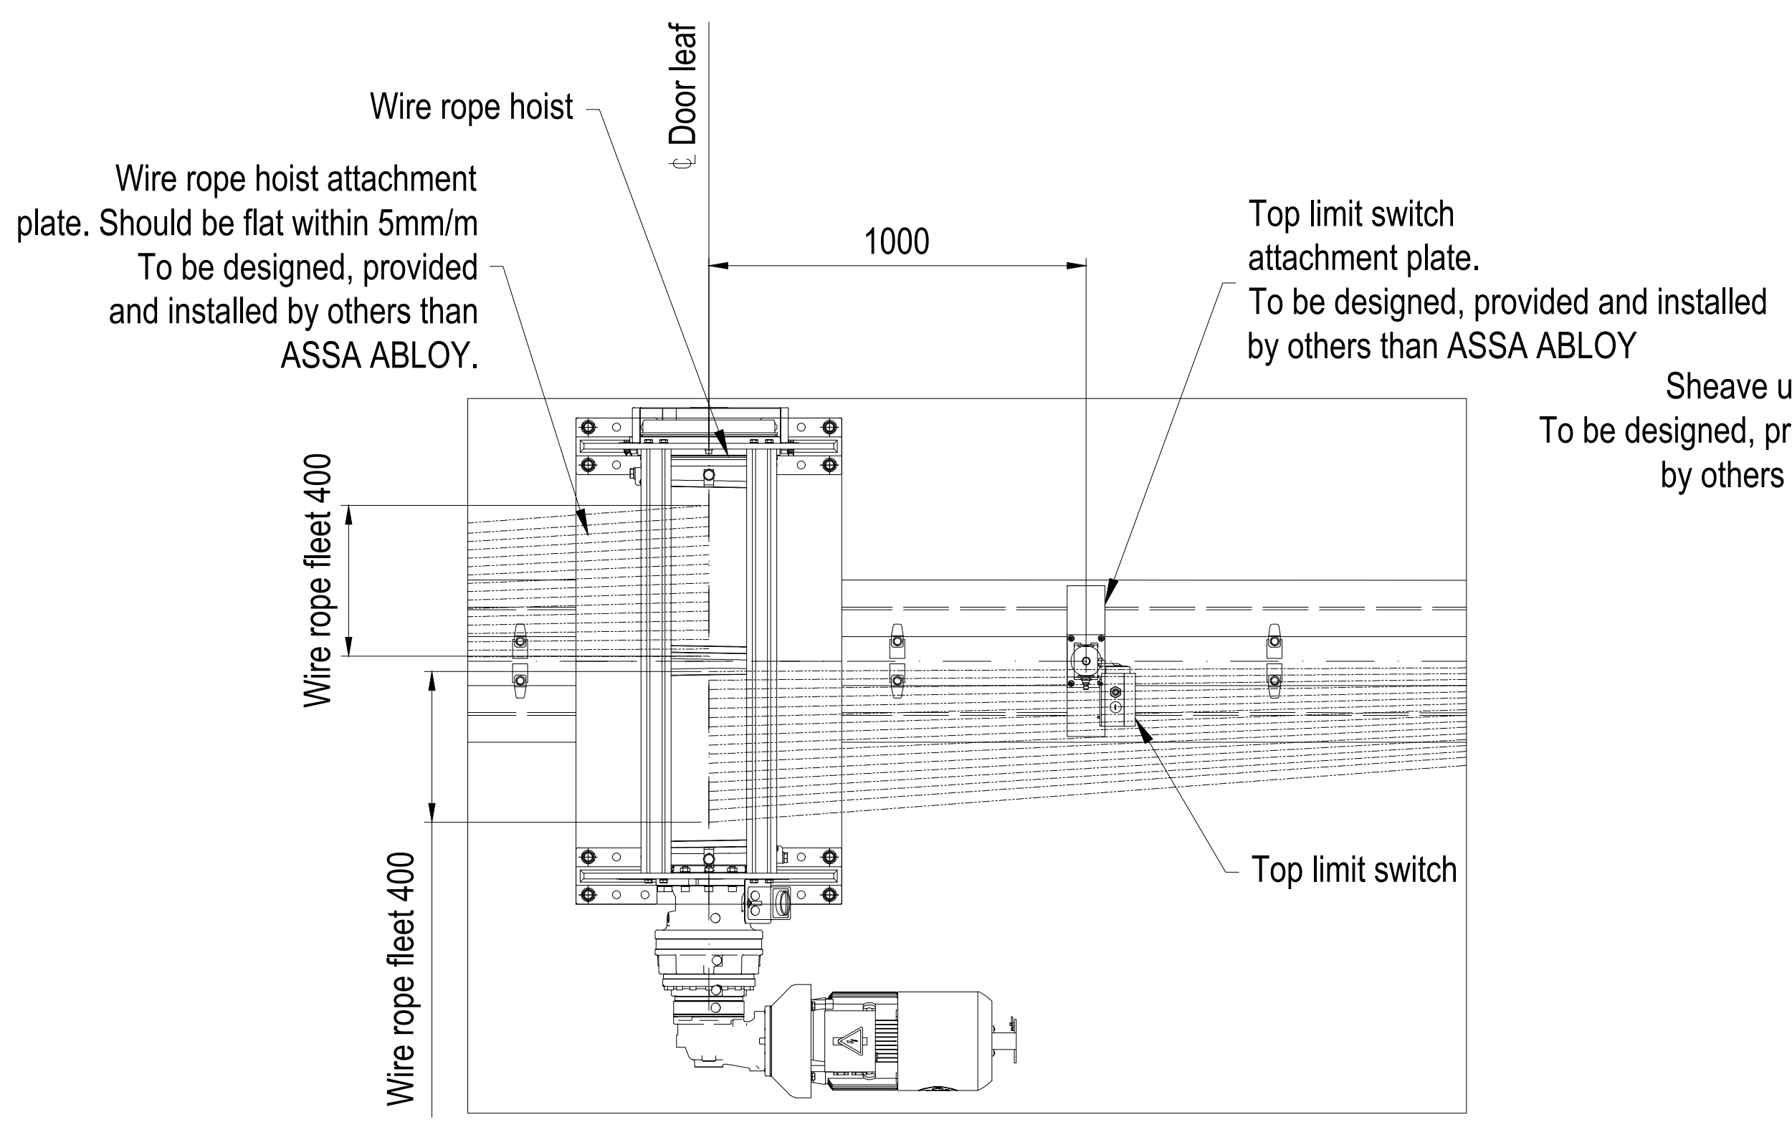
Wire rope hoist
℄ Door leaf
Wire rope hoist attachment
plate. Should be flat within 5mm/m
To be designed, provided
and installed by others than
ASSA ABLOY.
1000
Top limit switch
attachment plate.
To be designed, provided and installed
by others than ASSA ABLOY.
Wire rope fleet 400
Wire rope fleet 400
Top limit switch

DETAIL K, SCALE (1:20)

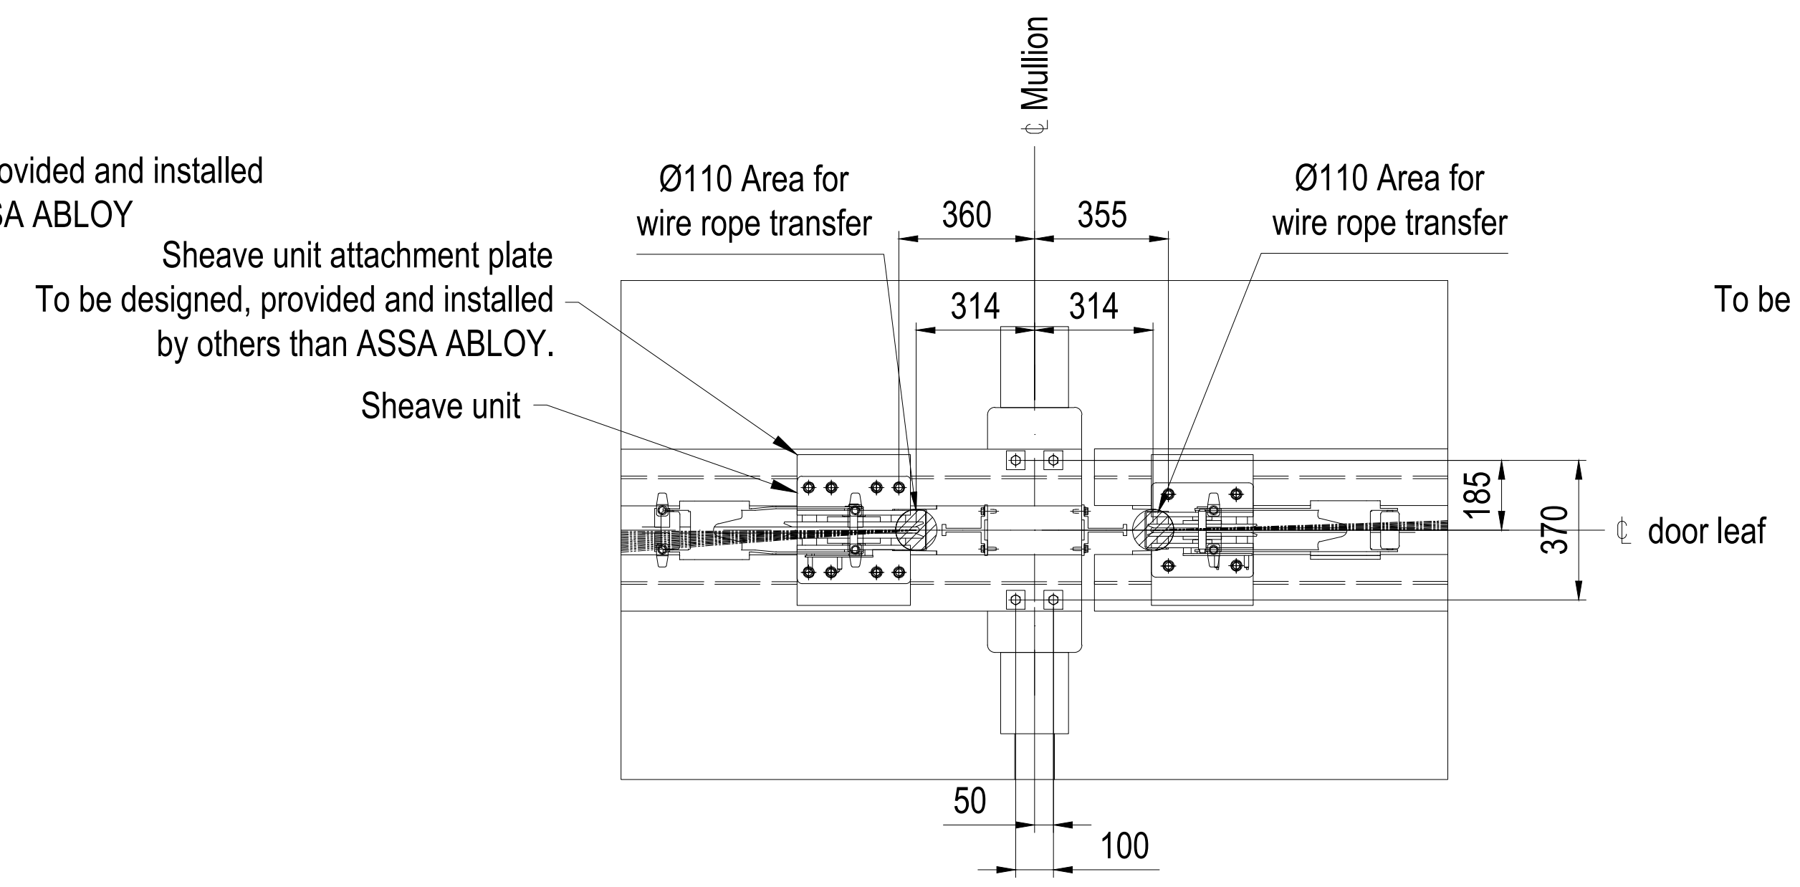

DETAIL L, SCALE (1:20)

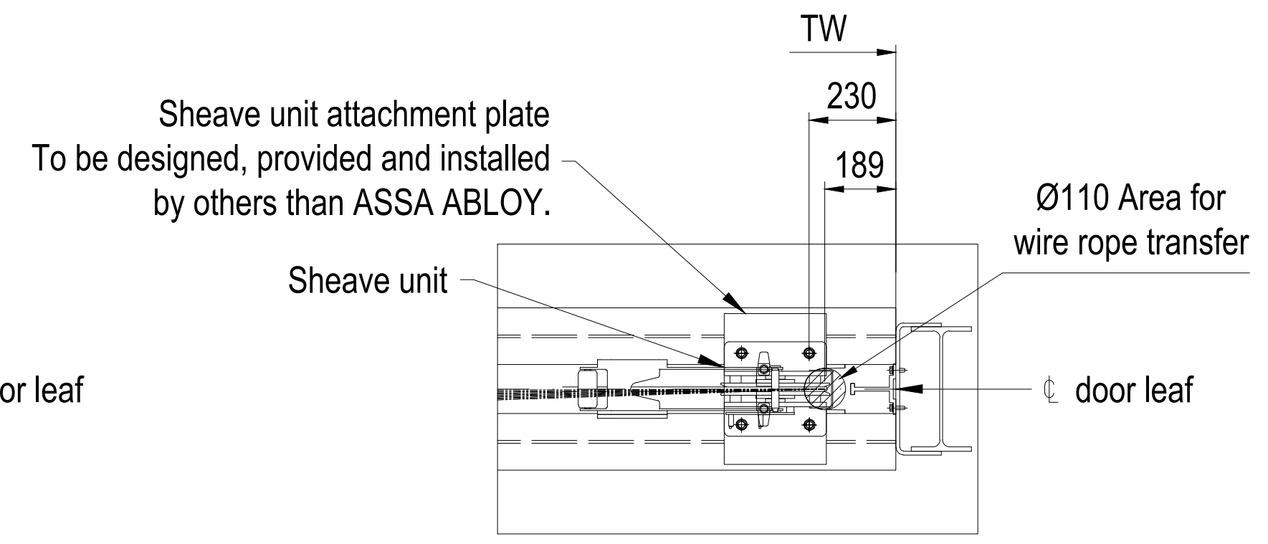
TW
230
189
Sheave unit attachment plate
To be designed, provided and installed
by others than ASSA ABLOY.
Sheave unit
Ø110 Area for
wire rope transfer
℄ door leaf

DETAIL M, SCALE (1:20)

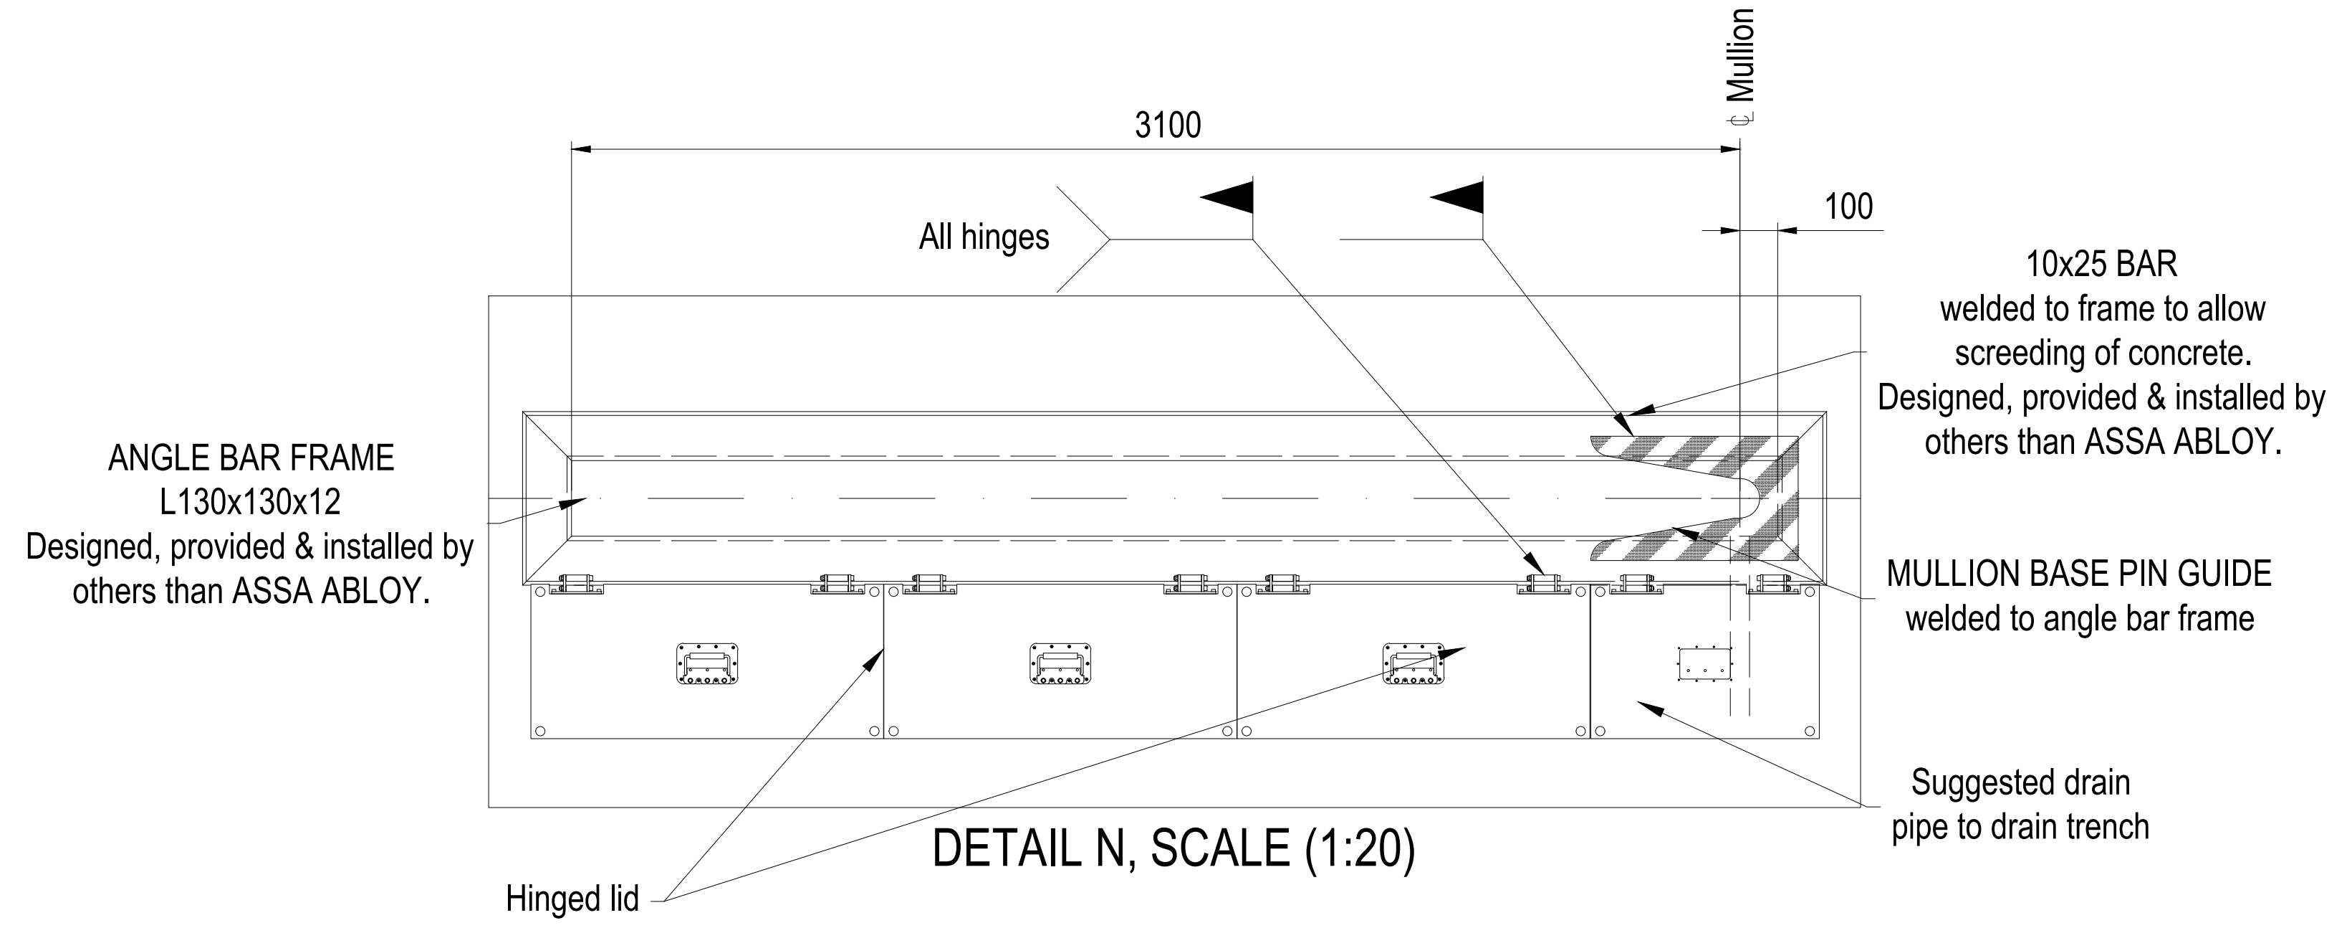

DETAIL N, SCALE (1:20)

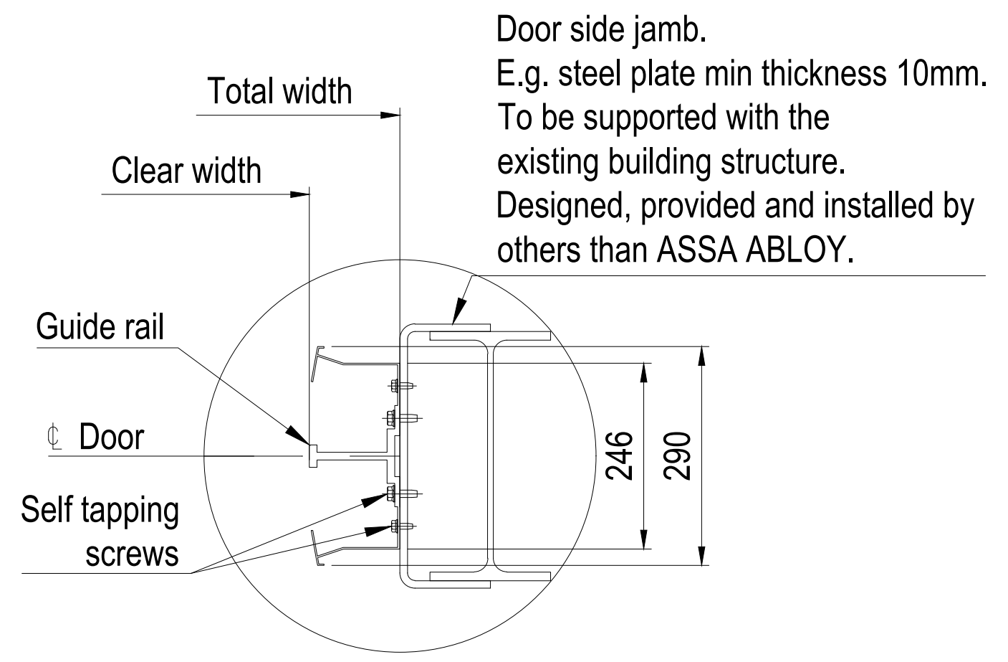

DETAIL O, SCALE (1:10)

DOOR IDENTITY NUMBER: 84800001

LOAD DIAGRAM & NOTES, ref. to drwng. no. 77446

INTERFACE, SECTIONS ref. to drwng. no. 77445

INTERFACE, ELEVATION ref. to drwng. no. 77443

DESIGNED
EB
SIZE A1F
SCALE 1:100
CODE
84800
ITEM NO
DATE
2022-08-23
ASSA ABLOY

If not otherwise stated:
Tolerances
ISO 2768-m
EN ISO 13920-B
Cutting class
ISO 9013-442
Weld class
ISO 5817-C
Surface finish
Smooth raw surface

GMR Aero Technic Hangar1
India
Megadoor 84000x23000/14000
Interface, Plan views

PLOT DATE
DRAWING NO
77444
REVISION
B

This document is the property of ASSA ABLOY Entrance Systems AB and shall not without our written permission be copied, imparted to a third party or used for any other unauthorized purpose.