

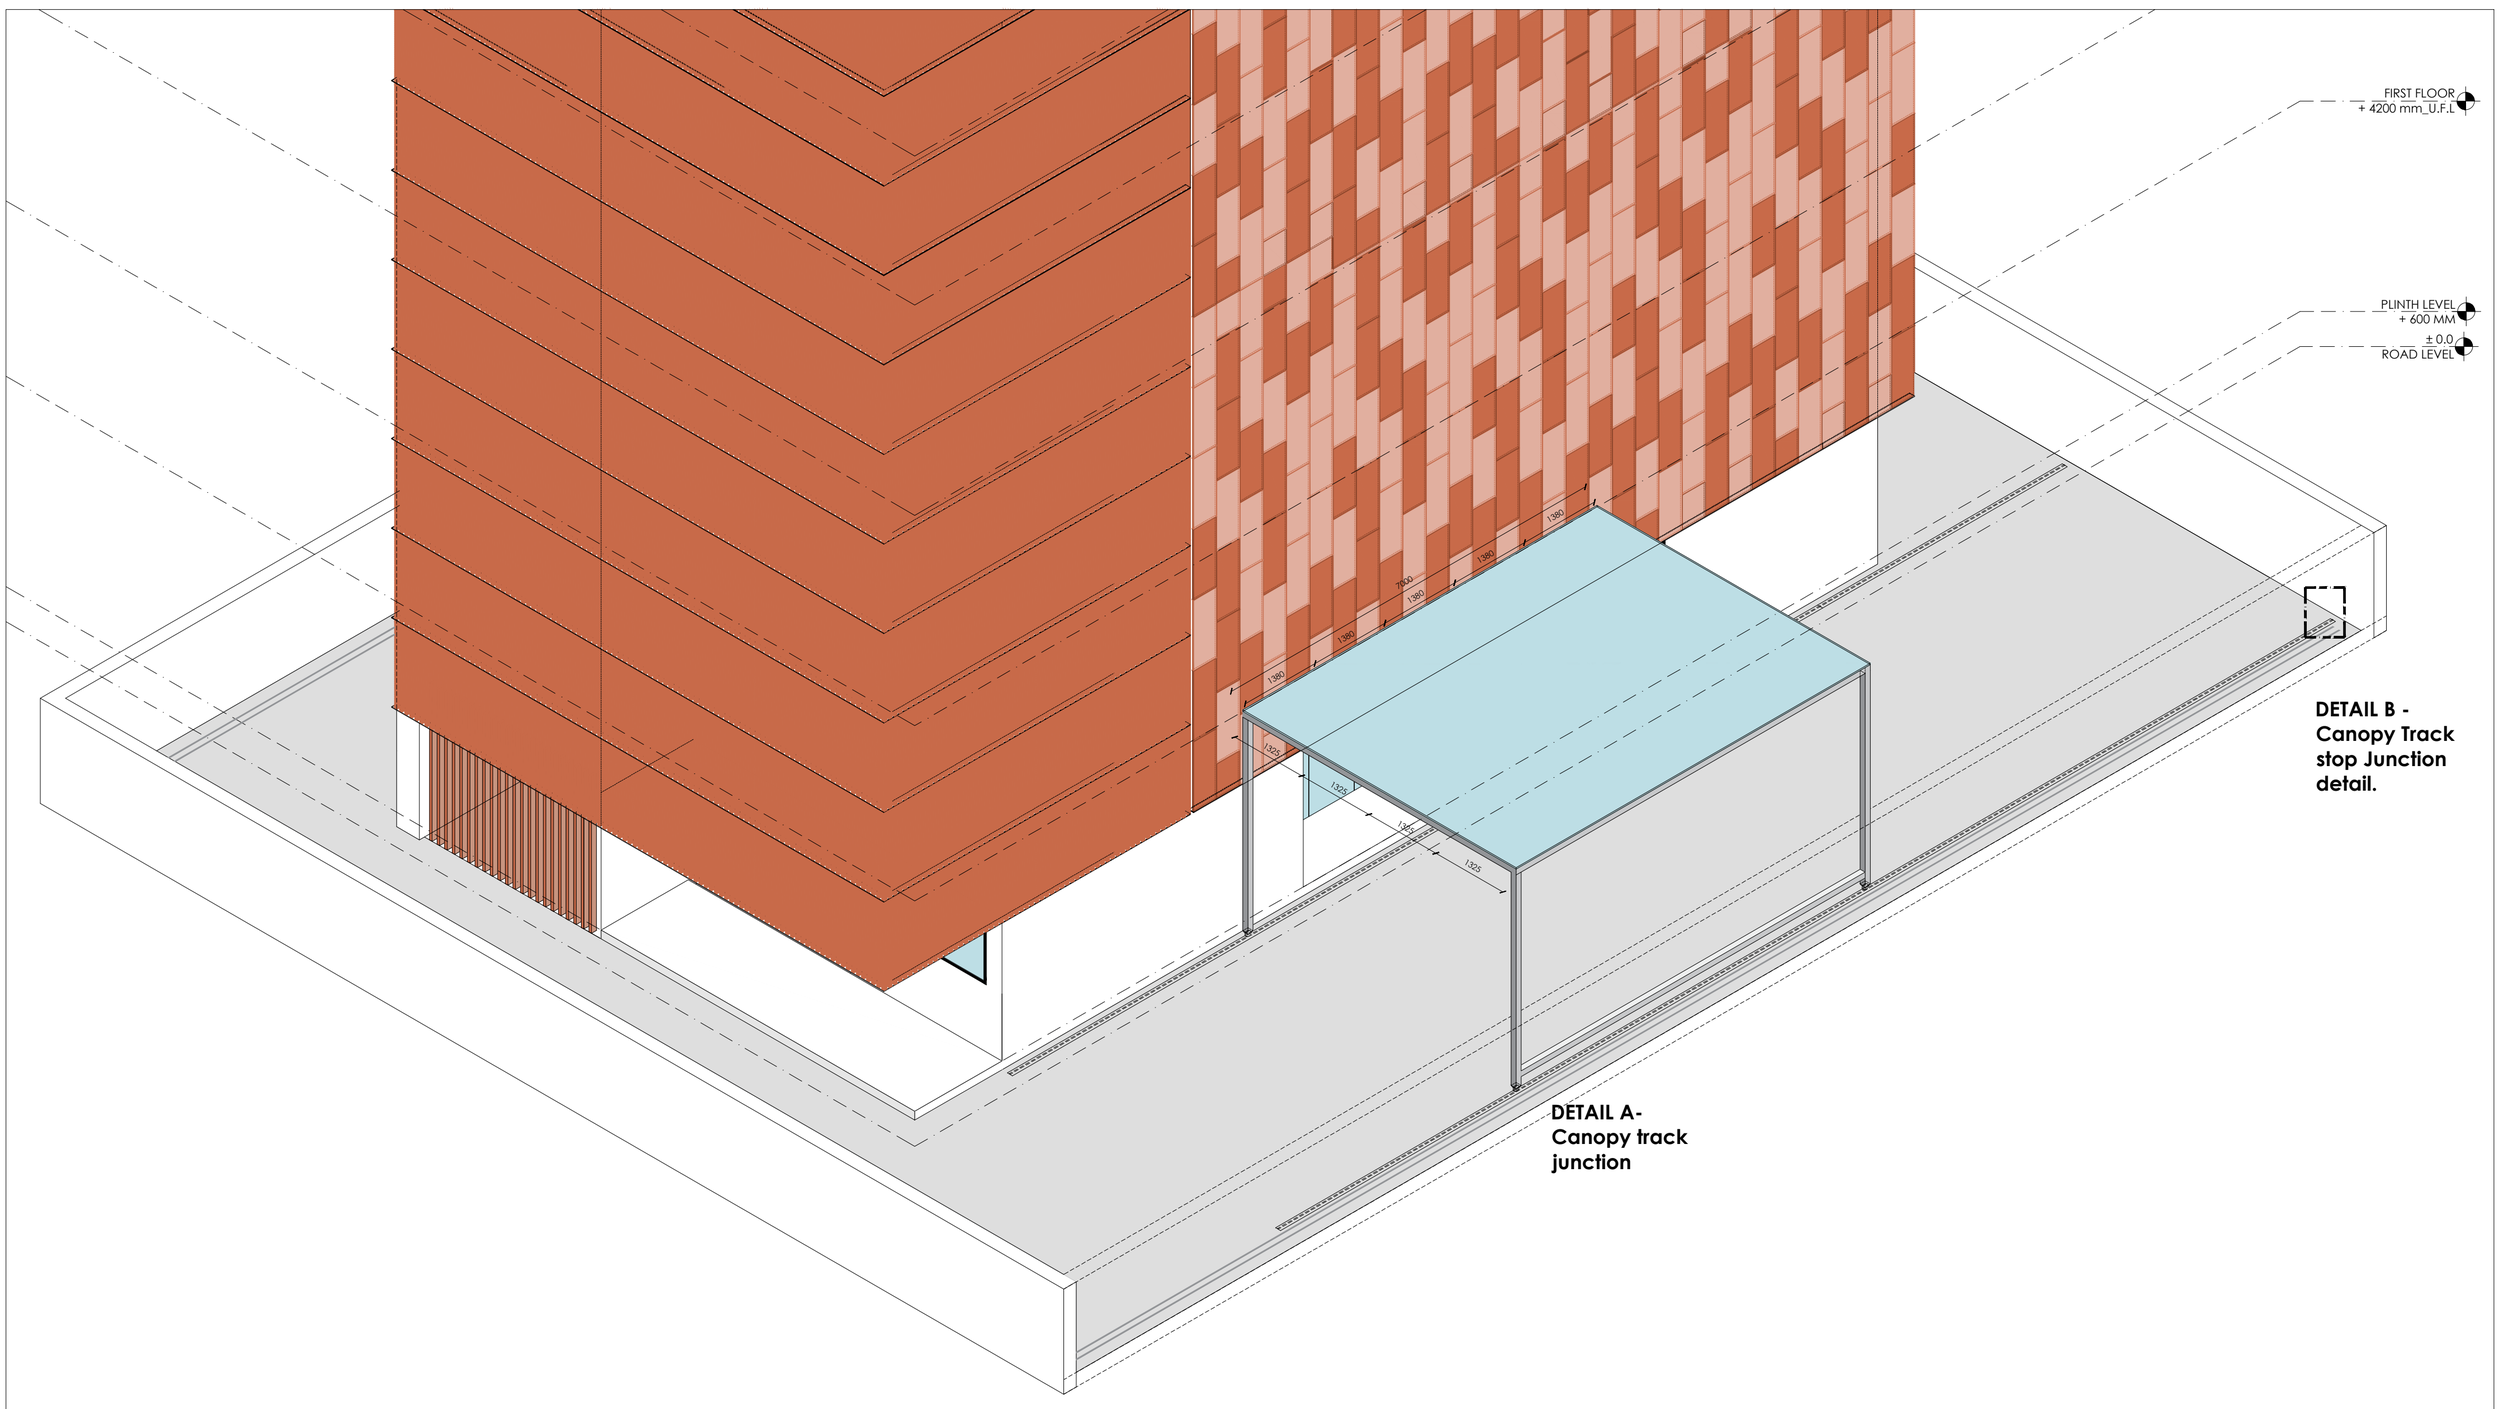



GROUND FLOOR ISOMETRIC VIEW

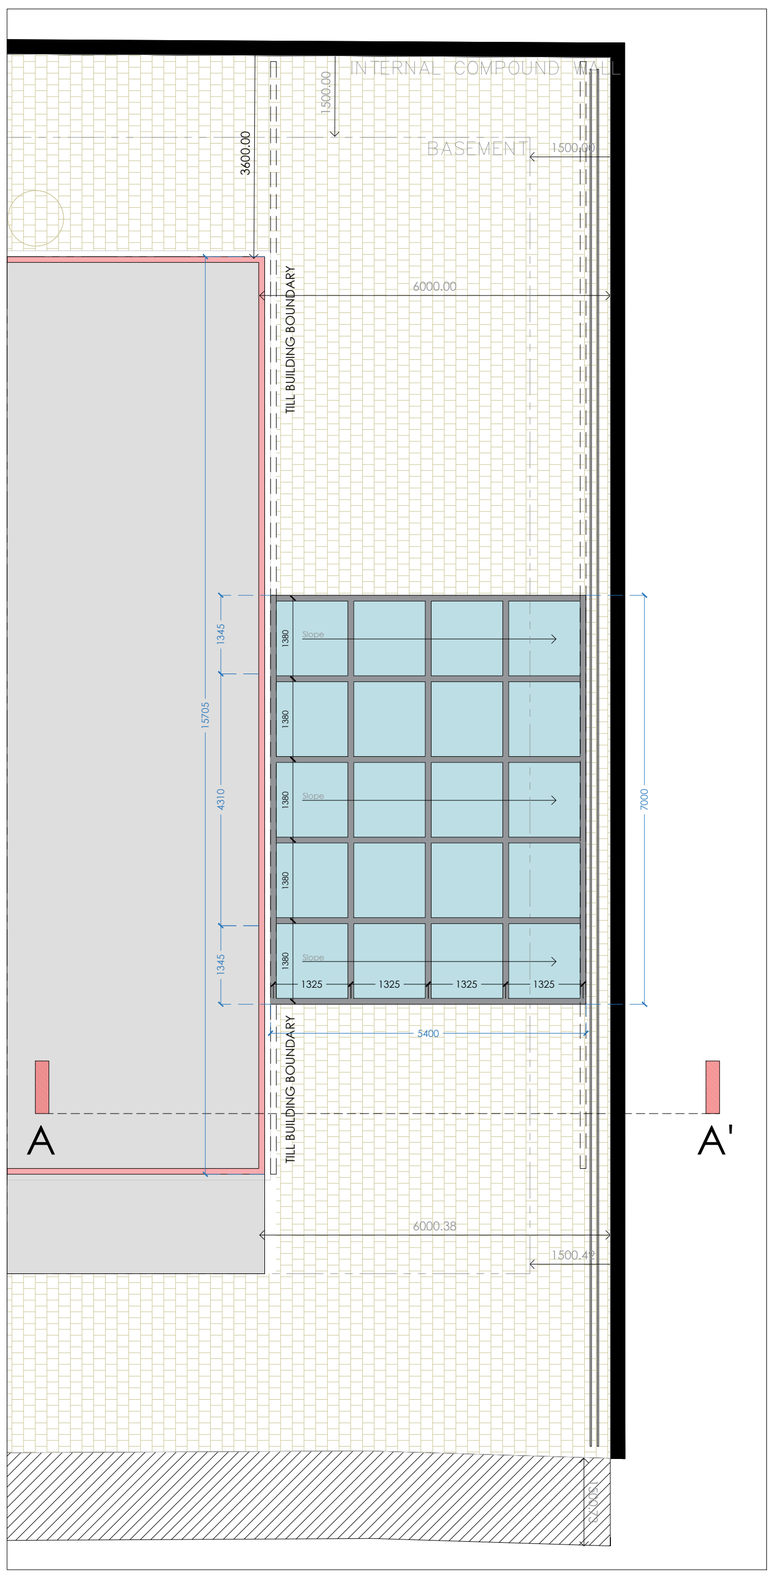

CANOPY PLAN

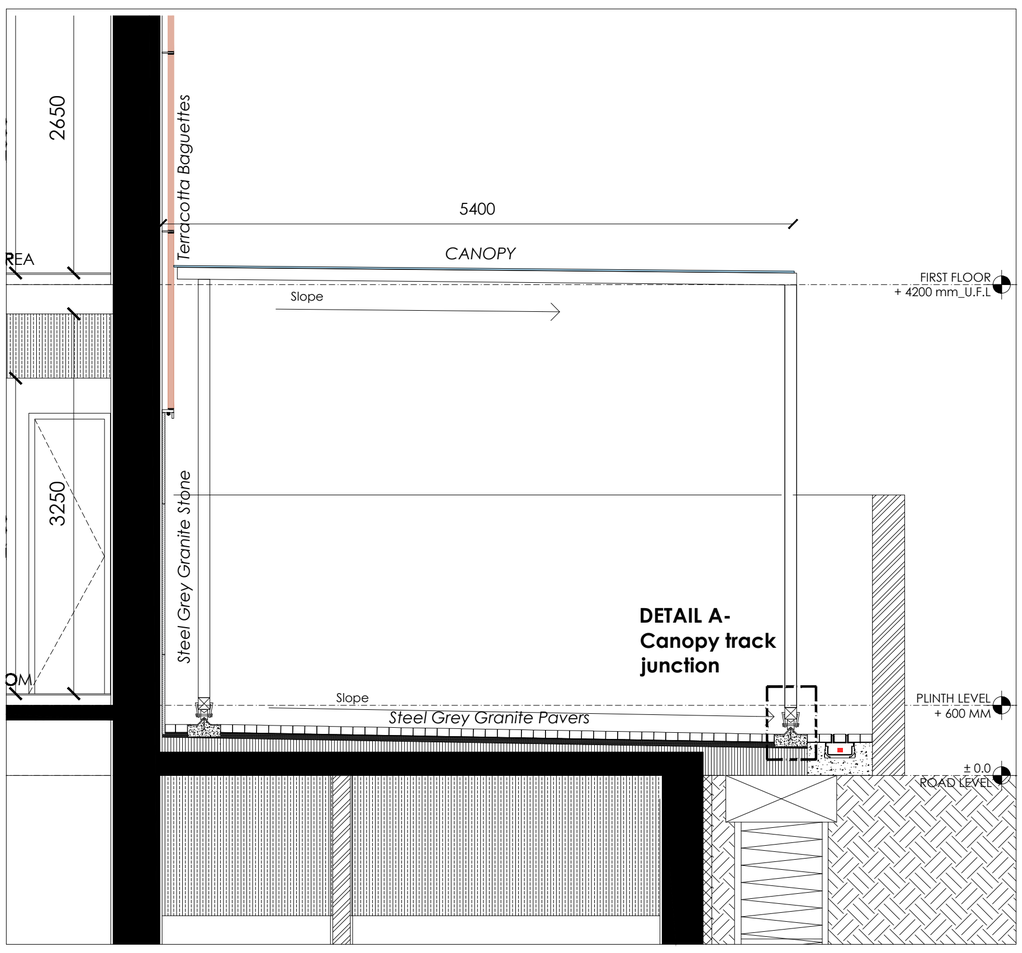

SECTION A-A'

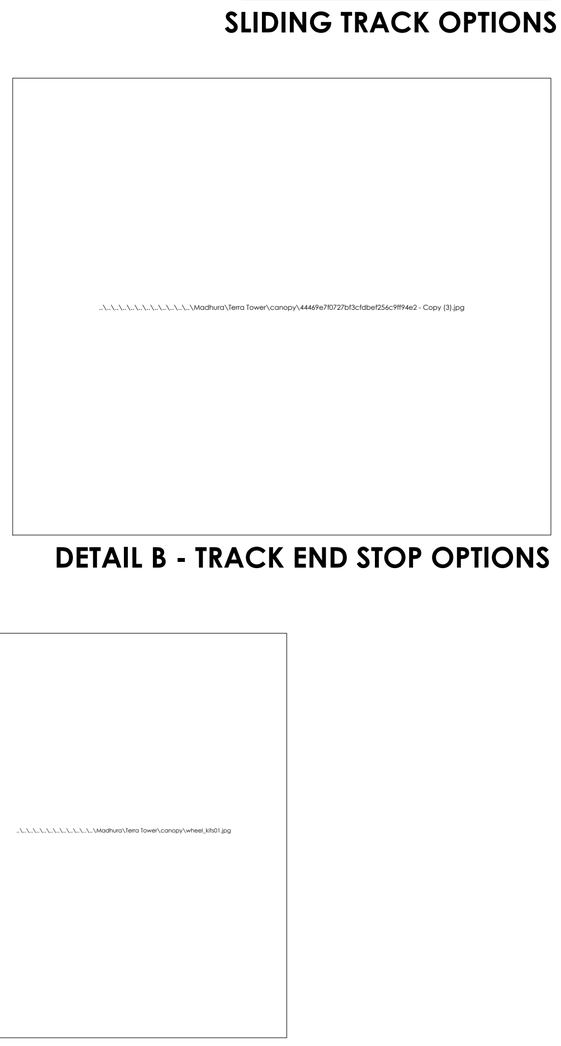


SLIDING TRACK OPTIONS

DETAIL B - TRACK END STOP OPTIONS



DETAIL A - HEAVY DUTY SLIDING TRACK WHEELS OPTIONS

 

LOCATION	DRAWING NO.
Matunga, Mumbai	

REVISIONS

Sr. no.	Date	Description
R0	14-11-2022	---

NOTE :

1. **Do not scale the drawings. For any discrepancy in the measurements, please refer to the Architect.**
2. **For all the structural details, kindly refer to structural consultant's details and drawings**
3. **Existing Road Level (E.R.L) is considered as ± 0.0 lvl. All reference here are considered from this level.**

LEGEND

Project Title : ***Terra Tower_House for Society Tea***

Drawing Title : ***GROUND FLOOR SLIDING CANOPY CONCEPT***

Drawing No : ---

Drawing Status : For reference

Revision number : R0

Scale : 1: 100(A1 size)

Date : 14.11.2021

Drawn By : Madhura K.

Checked By : Aishwarya K.

SPASM DESIGN
ARCHITECTS