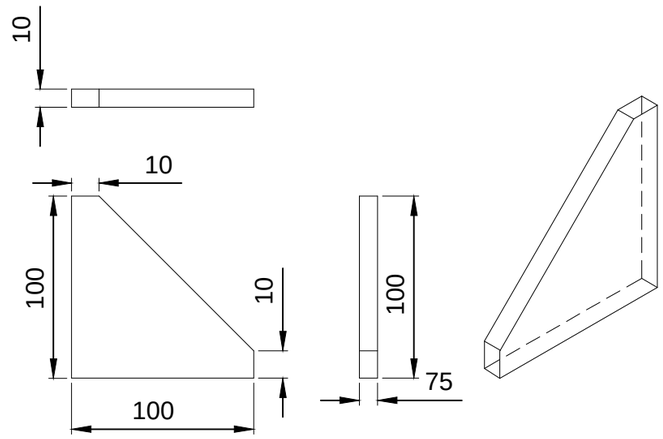

RIB DETAILS

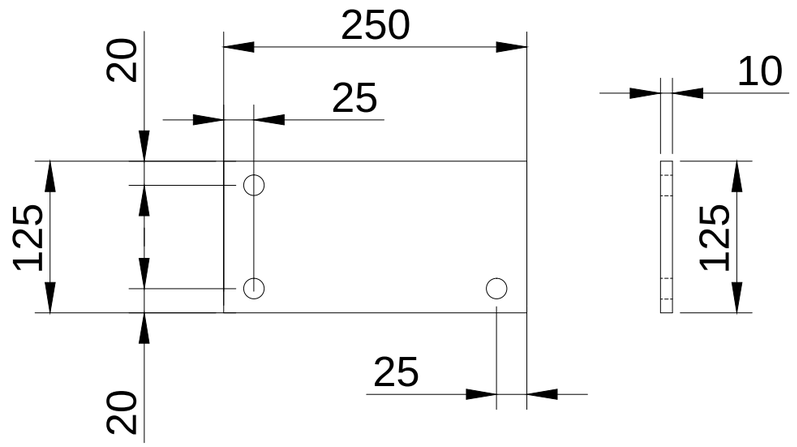

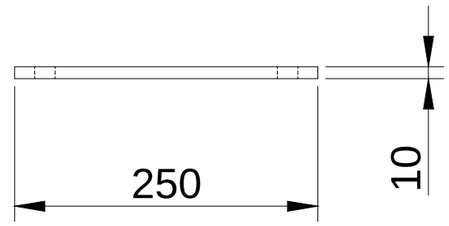

BOTTOM PLATE DETAILS

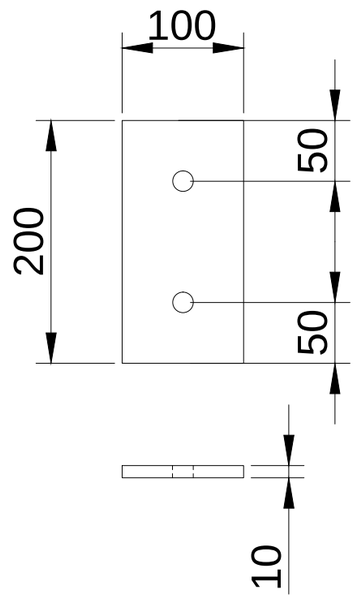

WALL PLATE DETAILS

MATERIAL	QTY.
MS	02 NOS

This drawing & design is the property of NIHVA TECHNOLOGIES. Not to be sold or copied to any other concern.

TITLE
RIB ,BOTTOM PLATE & WALL PLATE DETAILS

	NAME	SIGN	DATE
DRAWN	SURAJ		04/08/2018
CHECK	PRADEEP		04/08/2018
APPRD.	R.D		04/08/2018

NIHVA TECHNOLOGIES PVT. LTD.
NIHVA TECHNOLOGIES PVT. PUNE
Tel : 020 66304033
Email:- info@nihva.com
Website:- www.nihva.com

CLIENT -
PROJECT -
SITE LOCATION -
If any queries contact : design@nihva.com
DWG. NO. : NIHVA/18-19/VDR/089
REV- 0
ALL DIMENSION ARE IN mm
SCALE: NTS
WT:
SHEET: 01 OF 01