

Abbrevation's:
WOW-Wall Opening Width
WOH-Wall Opening Height
CH- Clear Height
UC-Under Cut
FFL-Finished Floor Level

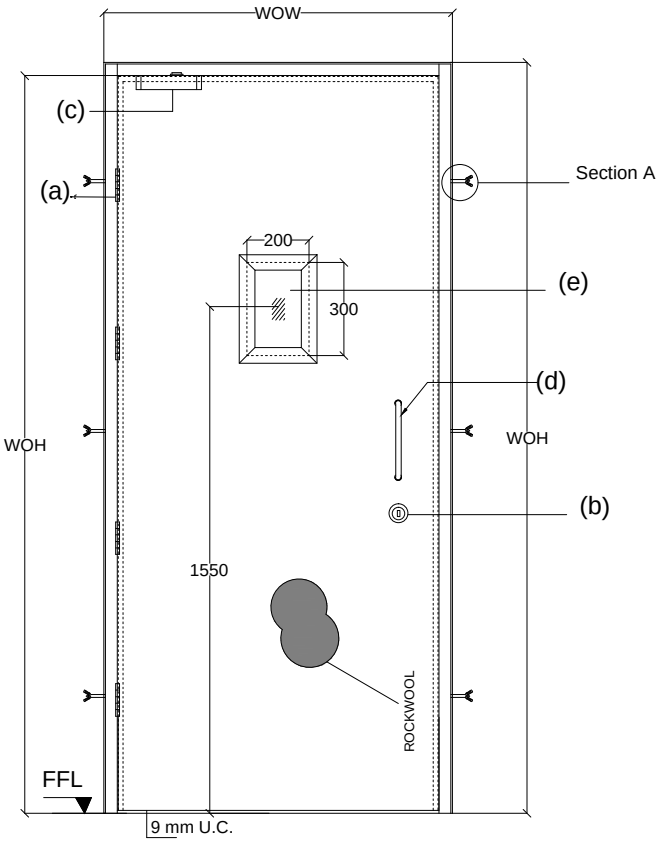

ELEVATION

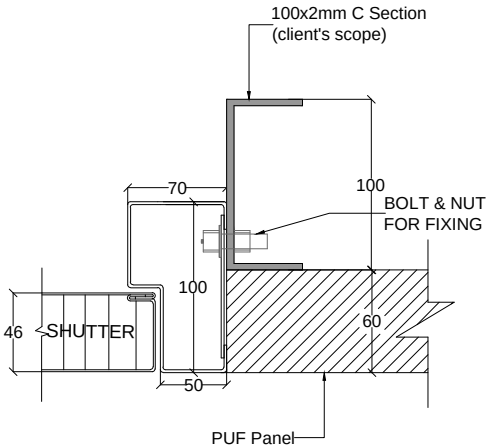

TOP VIEW



ASSESORIES DETALES

(a) HINGES: DORMA SS hinges 4"x3"x3mm

(b) LOCK : Mortise Dead Lock ML 112-Dorset with cylinder (One side key & other side turn bolt on Rose SSDORSET-CL 204) with escutcheon.

(c) DOOR CLOSER.

(d) HANDLE : D Handle (300x22) pair.

(e) VISION PANEL - 5mm THK. GLASS OF SIZE-200X300mm

Shutter thickness : 46 mm
Frame Sheet thick : 1.5mm
Shutter sheet thick : 1.2mm
Fixing : On MS sheet of 2mm Thk. with nut & bolt.

NOTE:- *All Dimensions are in mm.
*Tolerance:-All Linear Dimensions ±3mm,Others ±0.5mm.
*The Drawing Is For Location of Hardware only. Drawing Does Not Represent The Hardware For More Clarity, Please Go Through Hardware Broucher.

Fire door size

WOW	WOH	TYPE 1 LH	TYPE 2 RH	TYPE 3 LHR	TYPE 4 RHR	QUANTITY
1200	2100			10		10

This drawing & designing is the property of NIHVA TECHNOLOGIES. Not to be sold or copied to any other concern.

TITLE: 2 HRS FIRE RATED STEEL DOOR

	SIGN	DATE
DRAWN	OMKAR	09/12/17
CHECK	SHEKHAR	09/12/17
APPROVAL	SHEKHAR	09/12/17
MFG.		

If any queries contact : design@nihva.com

ALL DIMENSION ARE IN mm

NIHVA TECHNOLOGIES PVT. LTD.
NIHVA TECHNOLOGIES PVT. LTD. PUNE
Tel : 020 66304033
Email:- info@nihva.com
Website:- www.nihva.com

CLIENT-
PROJECT -
SITE -
DWG. NO. : NIHVA/17-18/VDR/0222 REV. : 0
SCALE: NTS WT: SHEET: 01 OF 01