




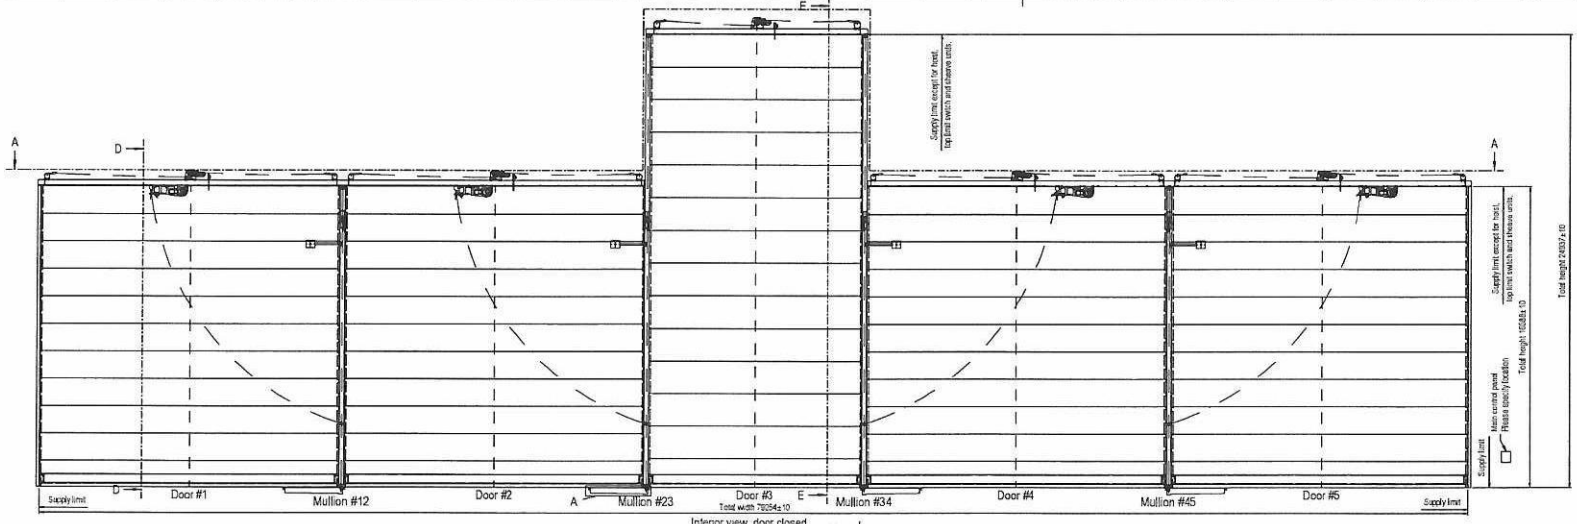


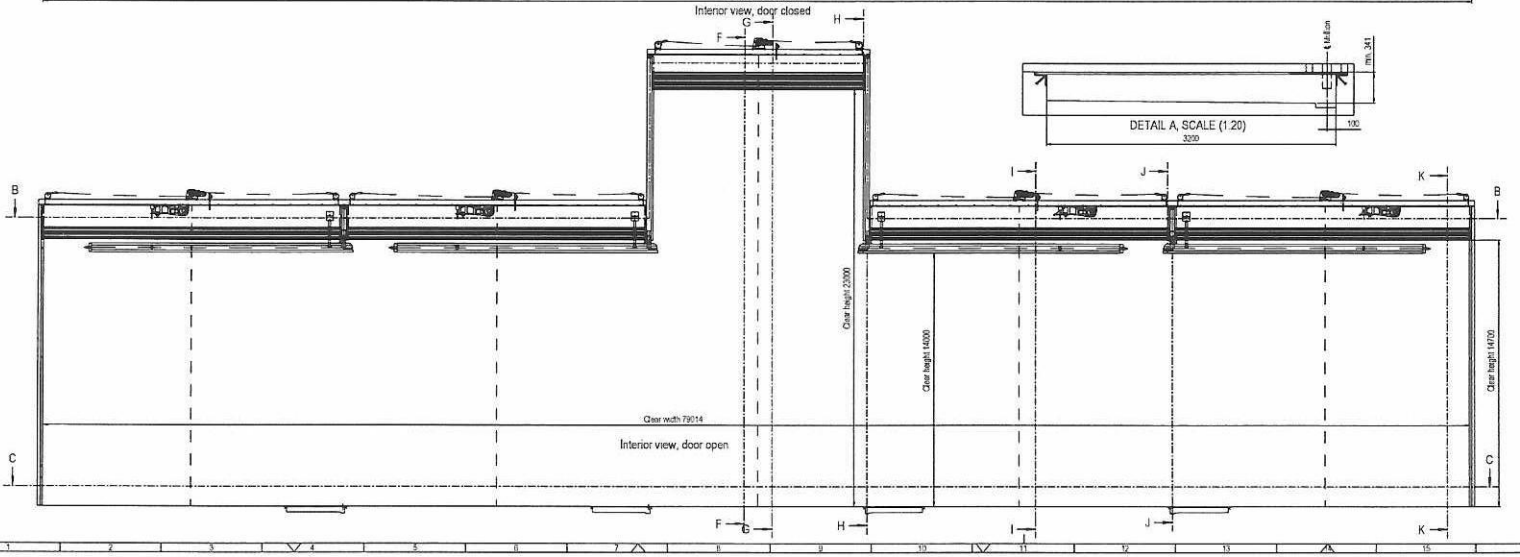

5.9T/27 Door #3

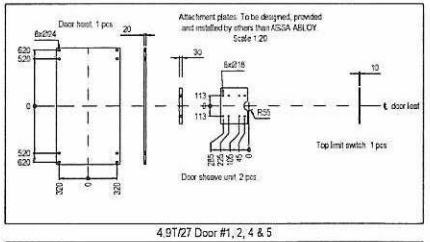



4.9T/27 Door #1, 2, 4 & 5

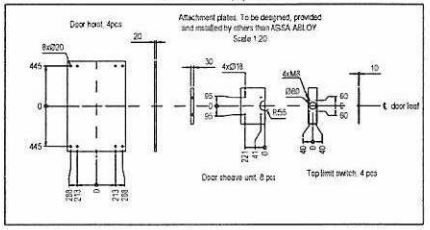




| |
|---|
| DOOR IDENTITY NUMBER 84800001 |
| LOAD DIAGRAM & NOTES, ref. to drwng. no. 77446 |
| INTERFACE, SECTIONS ref. to drwng. no. 77445 |
| INTERFACE, PLAN VIEWS ref. to drwng. no. 77444 |


| | | |
|---|---|---|
| EB | A1F 1:100 | GMR Aero Technic Hangar1 |
| 84800 | | India |
| 2022-08-23 | | Megadoor 79014x23000/14000 |
| | | Interface, Elevation |
| | | 77443 B |


NIHVA TECHNOLOGIES PVT. LTD. PUNE

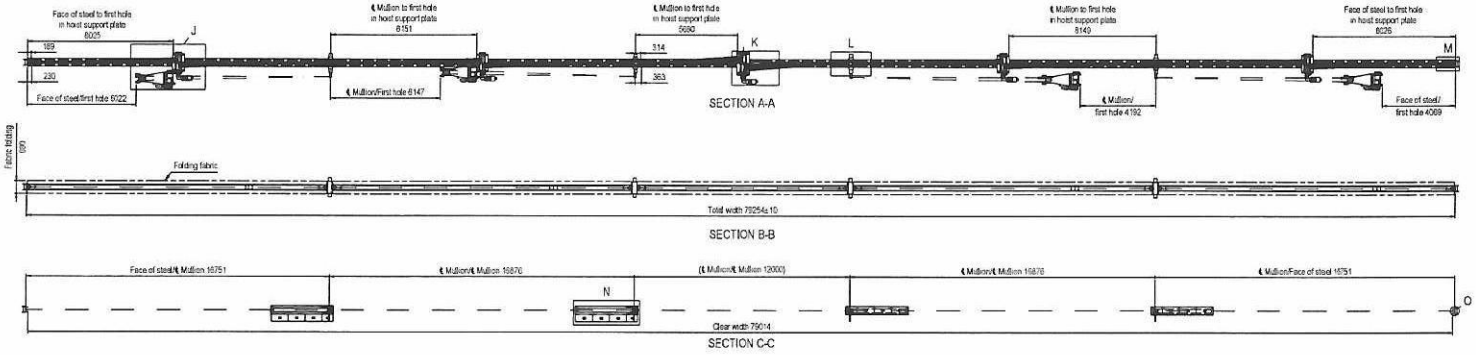


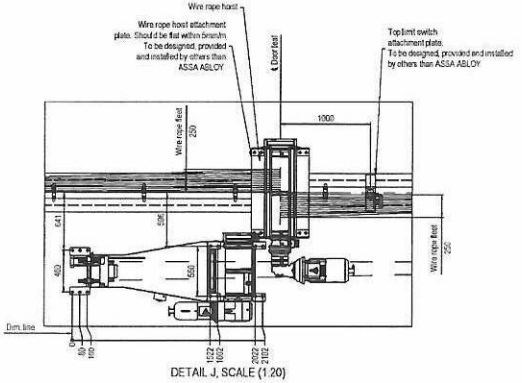


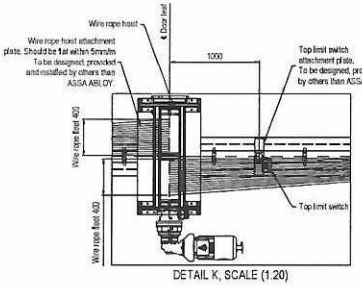
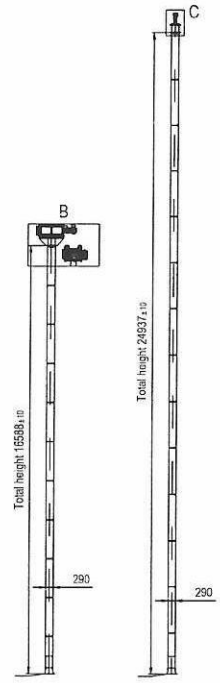


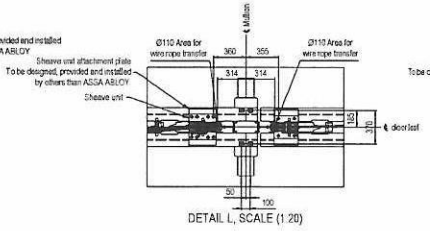
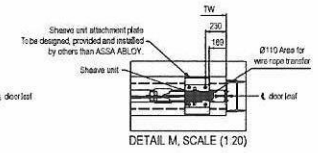
| | |
|---|---|
| DOOR IDENTITY NUMBER 84800001 | |
| LOAD DIAGRAM & NOTES, ref. to drwng. no. 77446 | |
| INTERFACE, SECTIONS ref. to drwng. no. 77445 | |
| INTERFACE, ELEVATION ref. to drwng. no. 77443 | |

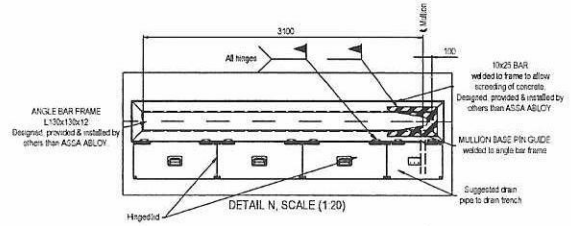
| | | | |
|---|---|---|---|
| DRAWN BY: FB | SIZE: A1F | SCALE: 1:100 | GMR Aero Technic Hangar1 |
| ORDER NO.: 84800 | | | India |
| DATE: 2022-08-23 | | | Megadoor 84000x23000/14000 |
| | | | Interface, Plan views |
| | | | DRAWING NO.: 77444 |
| | | | REVISION: B |

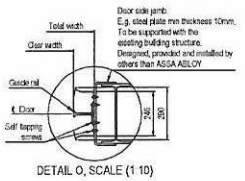NIHVA TECHNOLOGIES PVT. LTD.


| Revision | | Date | By |
|---|---|---|---|
| A | Corrected mullion hoist positions: floor pits altered | 2022-09-02 | EB |
| B | New measurements, doors redrawn | 2022-10-12 | EB |





SECTION D-D SECTION E-E

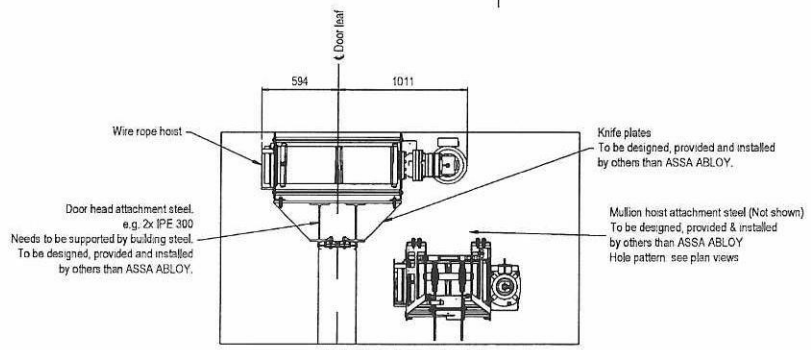



DETAIL B, SCALE (1:20)

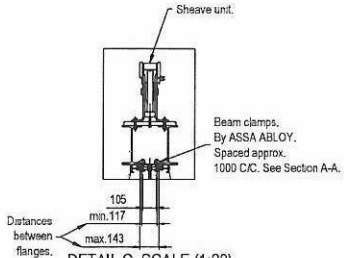



DETAIL C, SCALE (1:20)

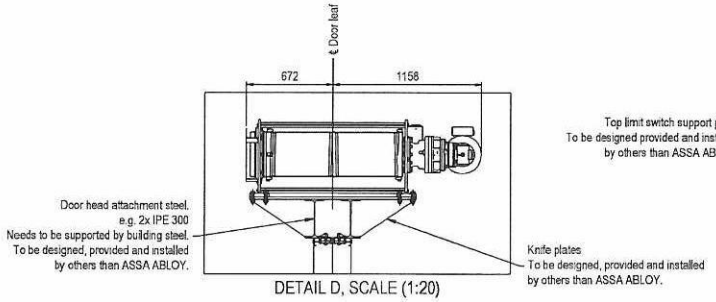


DETAIL D, SCALE (1:20)

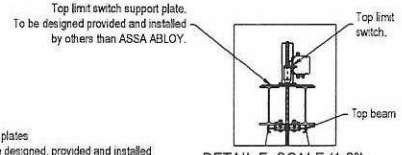



DETAIL E, SCALE (1:20)

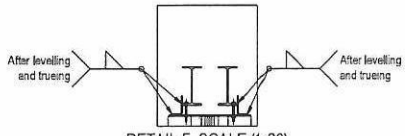



DETAIL F, SCALE (1:20)





SECTION F-F

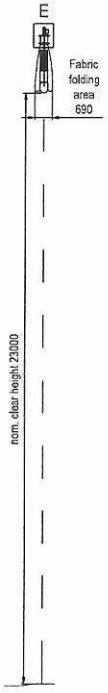



SECTION G-G

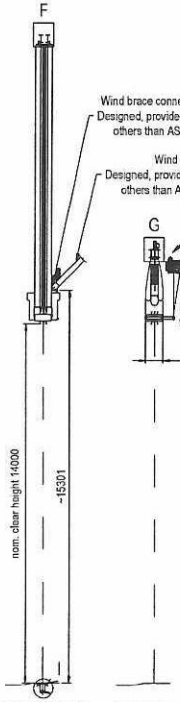


SECTION H-H

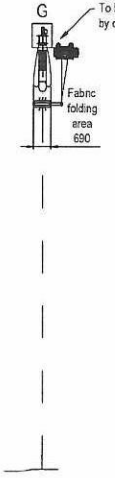



SECTION I-I

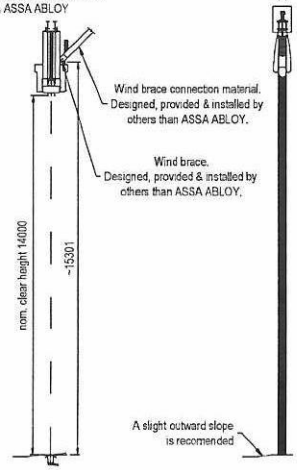



SECTION J-J





SECTION K-K

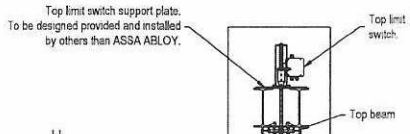


DETAIL G, SCALE (1:20)

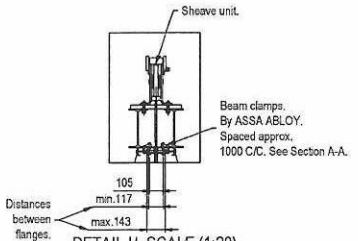


DETAIL H, SCALE (1:20)

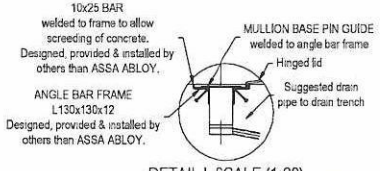


DETAIL I, SCALE (1:20)

DOOR IDENTITY NUMBER: 84800001

LOAD DIAGRAM & NOTES, ref. to drwng. no. 77446

INTERFACE, PLAN VIEWS ref. to drwng. no. 77444


INTERFACE, ELEVATION ref. to drwng. no. 77443


| | | | |
|---|---|---|---|
| DESIGNED EB | SIZE A1 | SCALE 1:100 | GMR Aero Technic Hangar1 |
| CODE 84800 | If not otherwise stated: Tolerances ISO 2768-mK EN/ISO 13920-B | | India |
| ITEM NO | Cutting class ISO 9013-442 | | Megadoor 79014x23000/14000 |
| DATE 2022-08-23 | Weld class ISO 5817-C | | Interface, sections |
| ASSA ABLOY | Surface finish Smooth raw surface | DRAWING NO 77445 | REVISION B |

PLOT DATE


This document is the property of ASSA ABLOY Entrance Systems AB and shall not without our written permission be copied, applied to a third party or used for any other unauthorized purpose.


LOAD DIAGRAM
Nominal static vertical loads are indicated. Value within brackets include dynamic surload factor 1.25 for door leaf loads in open position.
Includes items provided by ASSA ABLOY only

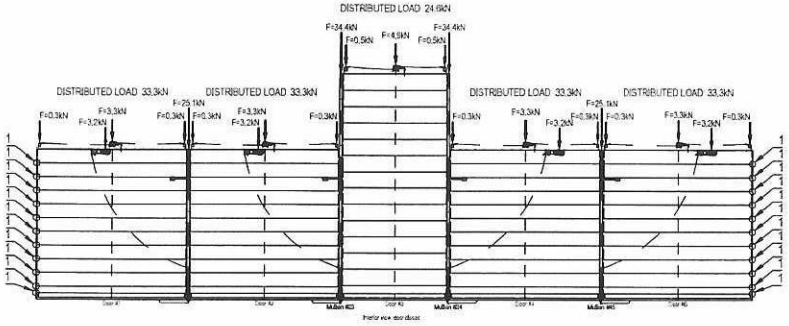

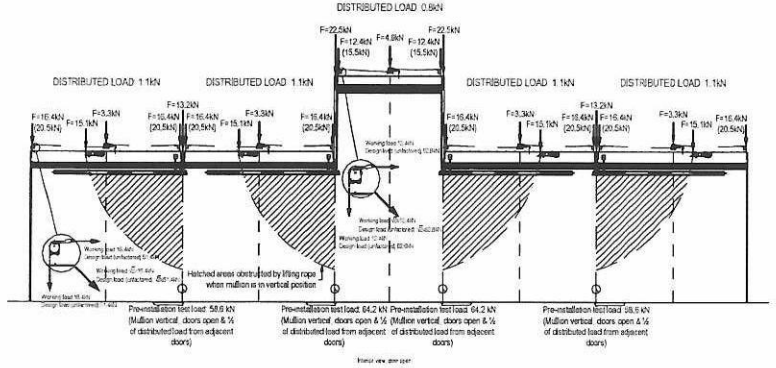
Steel building company in cooperation with door installing company must make a pre-installation load test on the structure, where the mullions are located, in order to simulate the vertical deflection of the structure that occurs when doors are installed. This vertical deflection figure will be used to determine the correct installation level of the mullions. Required material/equipment and personnel by others than ASSA ABLOY.




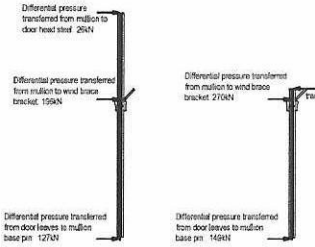


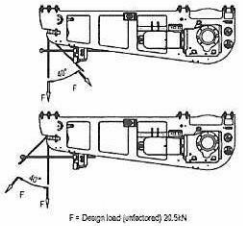





HOIST 4.9T

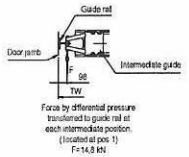

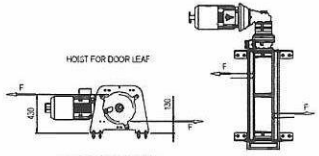
HOIST 5.9T

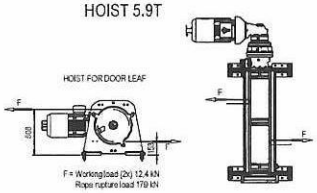


| Revision | Date | By |
|---|---|---|
| A Corrected mullion head positions. Door qty altered | 2022-08-02 | EB |
| B New measurements, doors redrawn, model added | 2022-10-12 | EB |

NOT INCLUDED IN DOOR SUPPLY
1. Design and supply of all door supporting structural components.
2. Design and supply of all closure between door and adjacent steel.
3. Design and supply of coverage, such as roofing or enclosure, for door components at door head.
4. Door jambs adjustable for overall door width and true to plumb.
5. Paint job after completed door installation.
6. Any frameworks being provided by ASSA ABLOY will be clearly indicated as "by ASSA ABLOY"

REQUIREMENTS ON BUILDING
7. Door head support must be straight within 1/600 of span in the in/out direction and free from protrusions of any kind.
8. For a single door leaf, door head support should be horizontal and straight within 1/600 of span at distributed full door load.
9. Door side jambs must be smooth, straight and parallel, out of plumb must not exceed 2mm/m (total deviation at full height 5 mm) in any direction.
10. Any footings at bottom of jamb columns must not interfere with installation of guide rails at floor level.
11. At time of installation, finished floor free from obstructions, out to a distance of 2 m on each side of door centreline must be available.
12. Bracket/attachment plate for hoist should be flat within 5mm/m.

DOOR PROPERTIES
13. The door is designed to withstand a differential pressure of 1.2kPa.
14. Mullions and mullion jets are designed to allow for 128mm of downward deflection and 128mm of upward deflection due to external loads such as wind.
15. Guide rails: top- and intermediate beams in extruded aluminium with natural finish.
16. Environmental category: Megadoor standard
17. Bottom beam in carbon steel painted. Light grey (RAL7047).
18. Colored clamp strips on both sides
19. The door fabric is a UV stabilized, flame retardant, self-extinguishing, PVC coated polyester fabric with fire technical properties Euroclass B-s2, d0 (according to EN 13501-1:2007)
Colour of fabric: TBD
RED (NCS S2570-R, RAL 3001)
BLUE (NCS S3560-R60B, RAL 5005)
GREY (NCS 3500, RAL 7004)
WHITE (NCS 0500, RAL 9016)
TAN (NCS 2010-Y40R, RAL 1001)
WHITE ALUMINUM ( RAL 9006)
GREEN (NCS 8010-G10Y, RAL 6009)
ANTHRACITE GREY ( NCS 6005-B20G, RAL 7016)
(Please specify)

ELECTRICAL
20. One main control panel provided of PLC type.
21. One additional screen.
22. Control mode: Impulse up / Constant contact down.
23. Cables are included.
24. Back-up power socket & switch.
25. Audible & visual alarm.
26. Approx. size of main control panel: WxHxD (500x600x250 mm)
27. Location of main control panel: Please specify location
28. Aux. Voltage: 24VDC
29. Power supply: 400V (3Ph) 50Hz
30. Power: 41.3kW
31. Nom. current: 97.7A
32. Start. current: 214.2A
33. (max. allowed voltage drop at start: 5%)

WIRE ROPE HOIST UNIT
LIDAN 4.5T/227(4x)
2x Ø12mm wire ropes. Rupture load 100kN/rope.

LIDAN 5.9T/227(1x)
2x Ø16mm wire ropes. Rupture load 179kN/rope.

MULLION HOIST UNIT
LIDAN 1.75T/71(4x)
2x Ø10mm wire ropes. Rupture load 69.6kN/rope.

DOOR IDENTITY NUMBER 84800001

INTERFACE, SECTIONS ref. to drwng. no. 77445

INTERFACE, PLAN VIEWS ref. to drwng. no. 77444

INTERFACE, ELEVATION ref. to drwng. no. 77443

| | |
|---|---|
| DRAWN BY | EB |
| SIZE | A1F |
| SCALE | 1:200 |
| DOOR NO | 84800 |
| DATE | 2022-08-24 |

GMR Aero Technic Hangar1
India
Megadoor 84000x23000/14000
Load diagram & Notes

77446 B

NIHVA TECHNOLOGIES PVT. LTD. PUNE