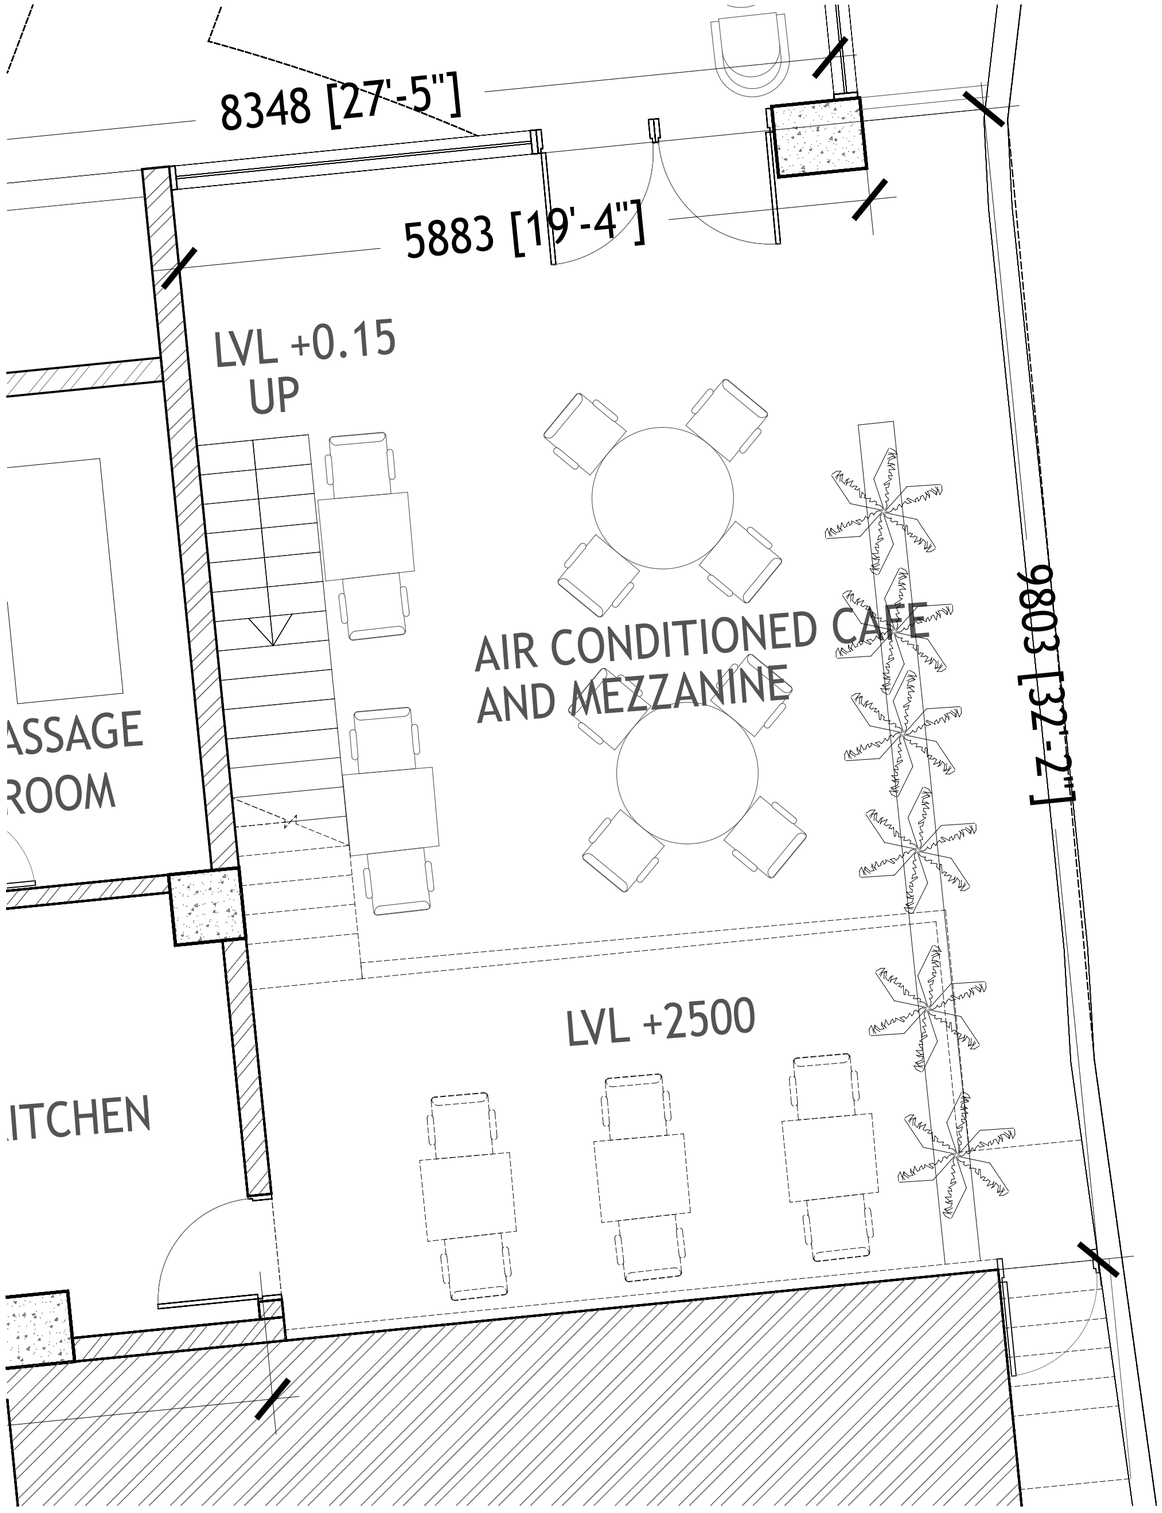


01 CLUBHOUSE CAFE

ARCHITECTURE DESIGN

sP+a

Planning Urban Design Architecture

22C New Kantwadi Scheme
Near China Blue
Off Turner Road, Bandra W
Mumbai 400050
Tel.: 91 22 2640 0557
www.sp-arc.net

Copyright © 2022-23
All rights reserved.

SIGN/STAMP

DATE

CONSULTANTS

MEP:

LIGHTING:

ACOUSTIC:

NOTES

1. ALL DIMENSIONS ARE IN MM.
2. DO NOT SCALE DRAWINGS.
3. ANY AMBIGUITY OR DISCREPANCY DISCOVERED SHALL BE REPORTED IMMEDIATELY TO THE ARCHITECT.
4. ALL LEVELS ARE MEASURED FROM THE UNFINISHED FLOOR LEVEL.
5. THESE DRAWINGS TO BE READ IN CONJUNCTION WITH STRUCTURAL AND SERVICES DRAWINGS.

NORTH

REVISION

NO.	DESCRIPTION	DATE

* APPLICABLE ON THIS SHEET

CLIENT

CHAITANYA TOWERS

PROJECT NAME

CHAITANYA TOWERS

SHEET TITLE

CLUBHOUSE CAFE

DRAWN BY: SM

CHKD BY: AJ

DATE: 13-10-2023

SHEET NUMBER:

A-1.07

LAYOUTS SIGN OFF- REVISION 09