


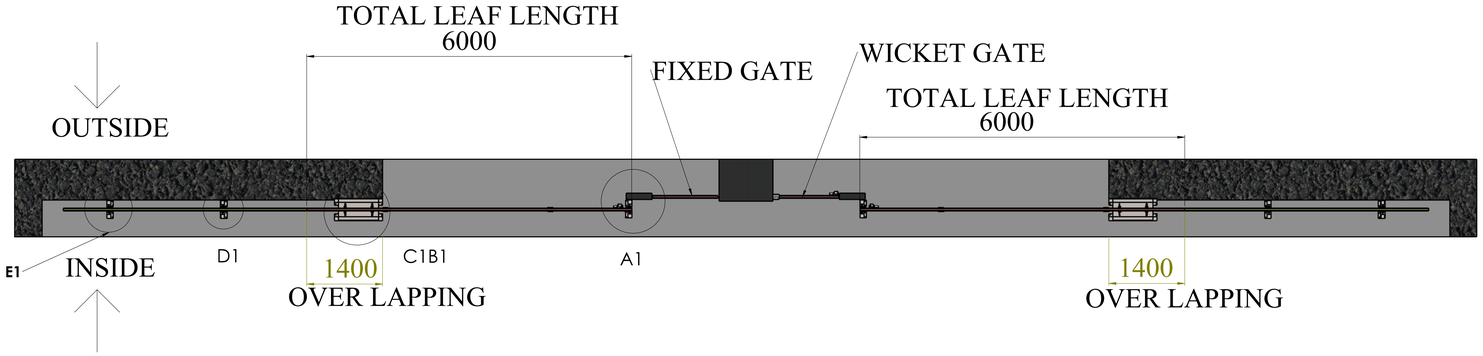


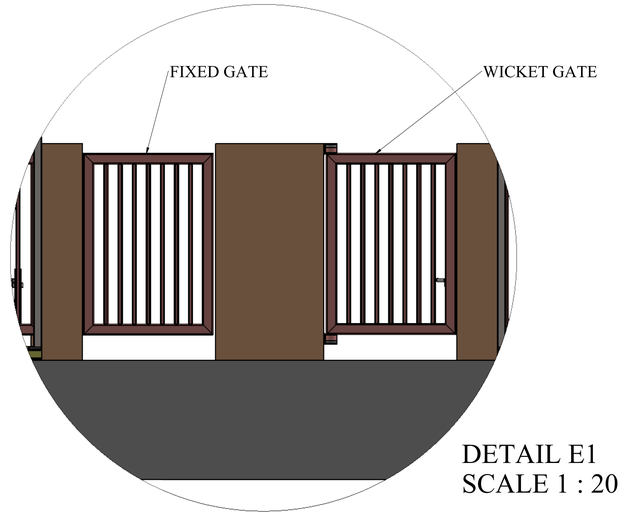


DETAIL E1
SCALE 1 : 20

FIXED GATE AND SWING
GATE VIEW

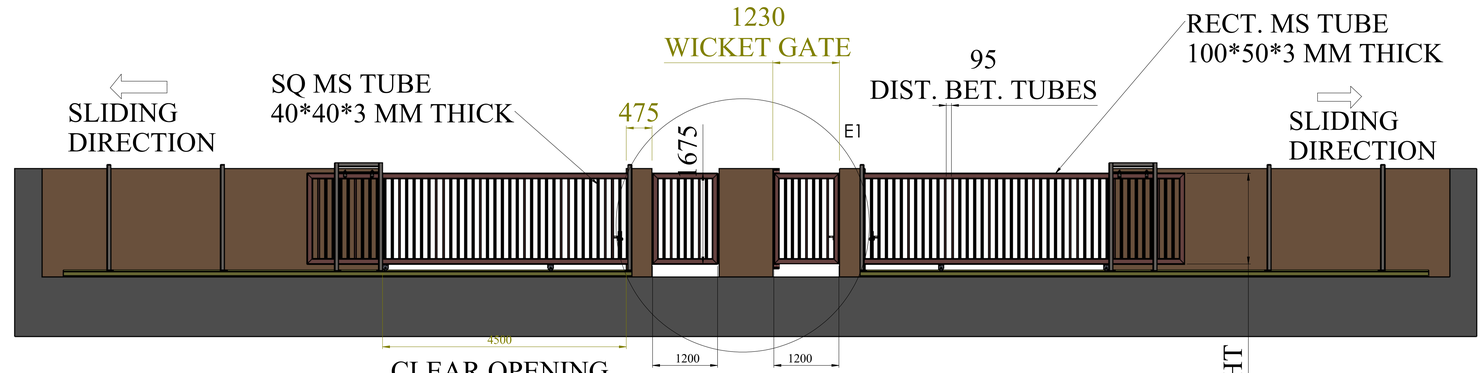


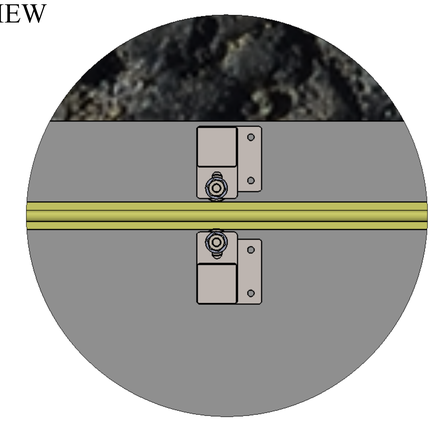

DETAIL D1
SCALE 1 : 4

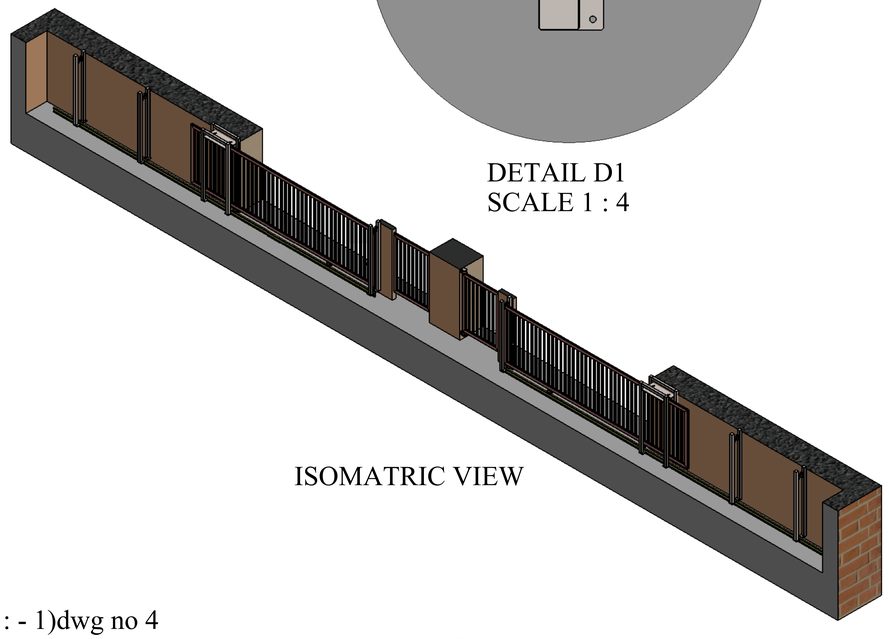


ISOMATRIC VIEW

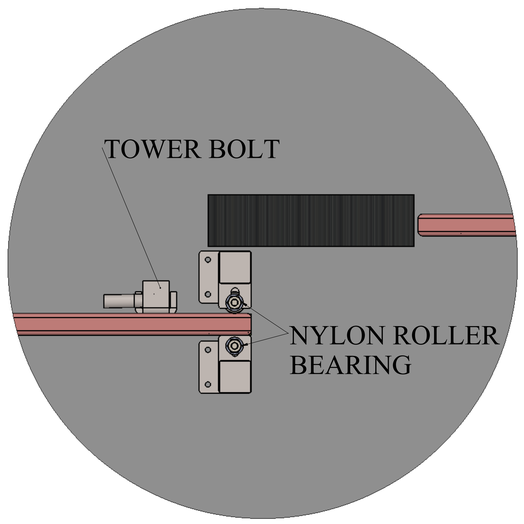

POST 1 AND NYLON ROLLER
BEARING ASSEM.

DETAIL A1
SCALE 1 : 5

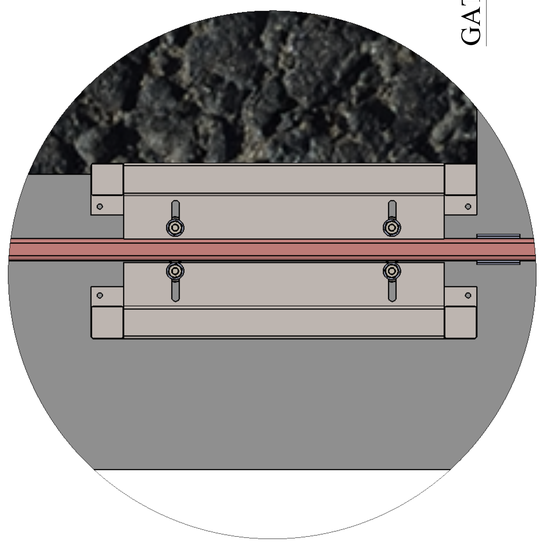

POST 2 AND NYLON ROLLER
BEARING ASSEM.

DETAIL C1B1
SCALE 1 : 5

Note : - 1)dwg no 4
2) barbed wire is not menstion in this dwg.
3)Total column -10(A1,B1,C1,D1,E1 SAME AS RIGHT SIDE ADD 5 POST)
4) 03 column posts when the gates is in the closed position.(A1,B1,C1)
5) 04 column posts when the gates is in the fully open position.(B1,C1,D1,E1)

UNLESS OTHERWISE SPECIFIED:
DIMENSIONS ARE IN MILLIMETERS
SURFACE FINISH:
TOLERANCES:
LINEAR:
ANGULAR:
FINISH:
DEBURR AND BREAK SHARP EDGES
DO NOT SCALE DRAWING
REVISION

	NAME	SIGNATURE	DATE
DRAWN			
CHK'D			
APPV'D			
MFG			
Q.A			

MATERIAL:
WEIGHT:
TITLE:
DWG NO.
SCALE:1:100
SHEET 1 OF 1

SBFINAL ASSM. GA DRAWING (TYPE NO 04