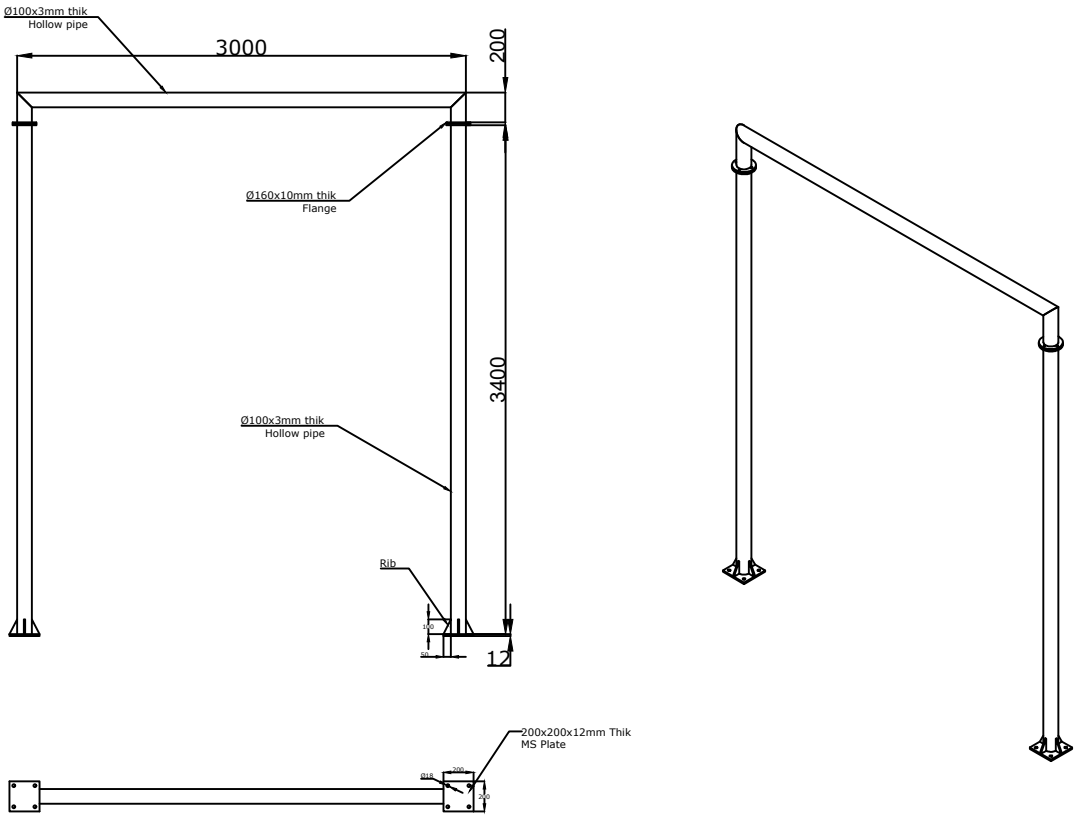


Sr.No	Description	Qty
1	STD Flange	4
2	200x200x12mm MS. Plate	2
3	M10x40mm Hex Bolt	8
4	M10 Hex Nut	8
5	M10 Spring Washer	16
6	M16x200mm Anchor Fastener	8

This drawing & design is the property of NIHVA TECHNOLOGIES. Not to be sold or copied to any other concern.

TITLE:- Door Safety Structure

NIHVA TECHNOLOGIES PVT. LTD.

NIHVA TECHNOLOGIES PVT. LTD. PUNE
Tel : 020 66304033
Email:- info@nihva.com
Website:- www.nihva.com

	NAME	DATE	SIGN
DRAWN	S.J	20/07/2024	
CHECK	B.B	20/07/2024	
APPRD.			

If any queries contact : design1@nihva.com

ALL DIMENSION ARE IN mm

CLIENT - Bilcare

LOCATION -

PRODUCT - QTY-01 Nos

DWG NO:- NIHVA/24-25/00XX REV-00

SCALE: NTS | SCALE:-- 1:1 | SHEET: 01 OF 01