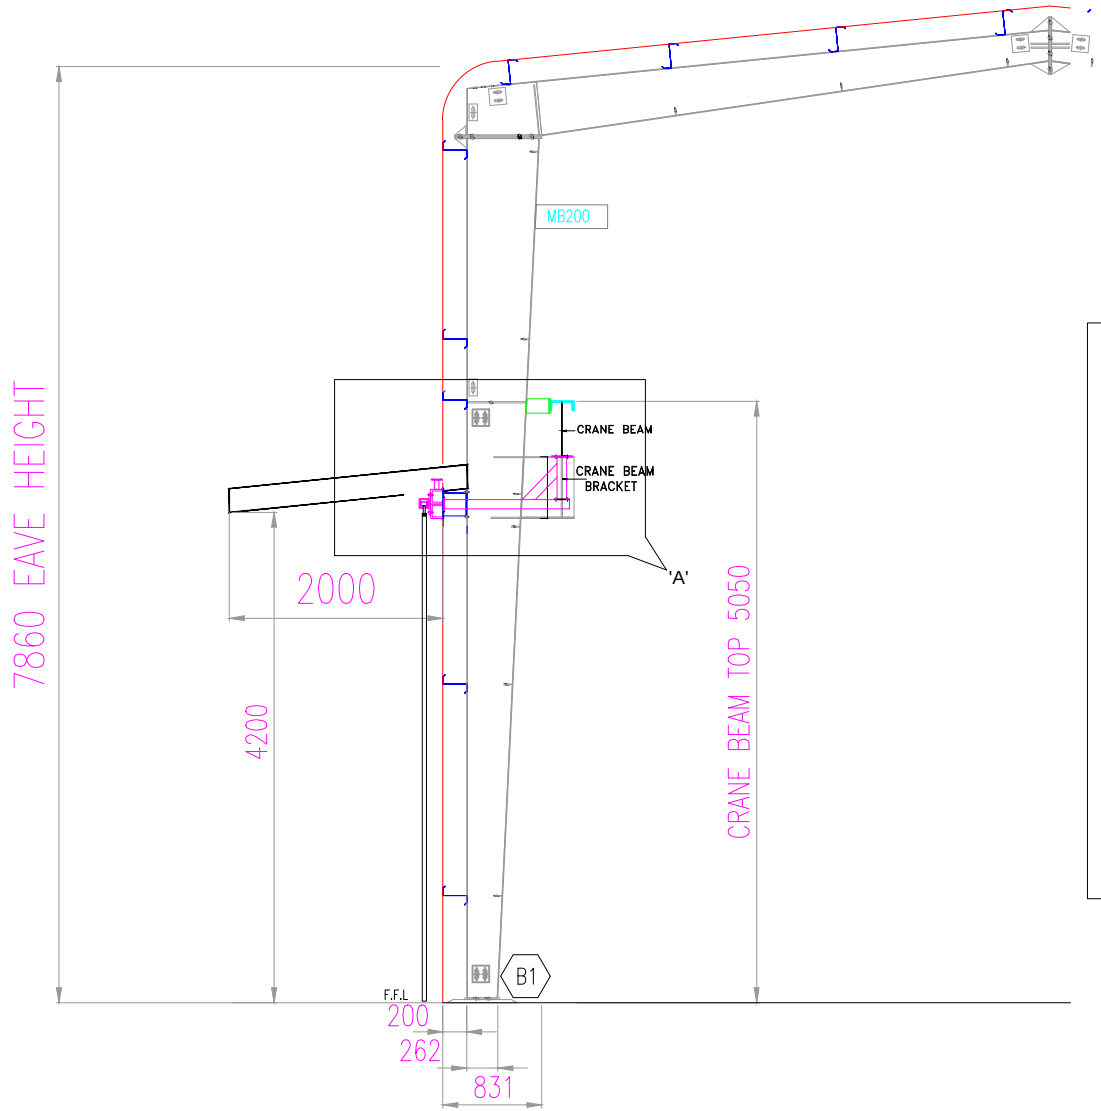
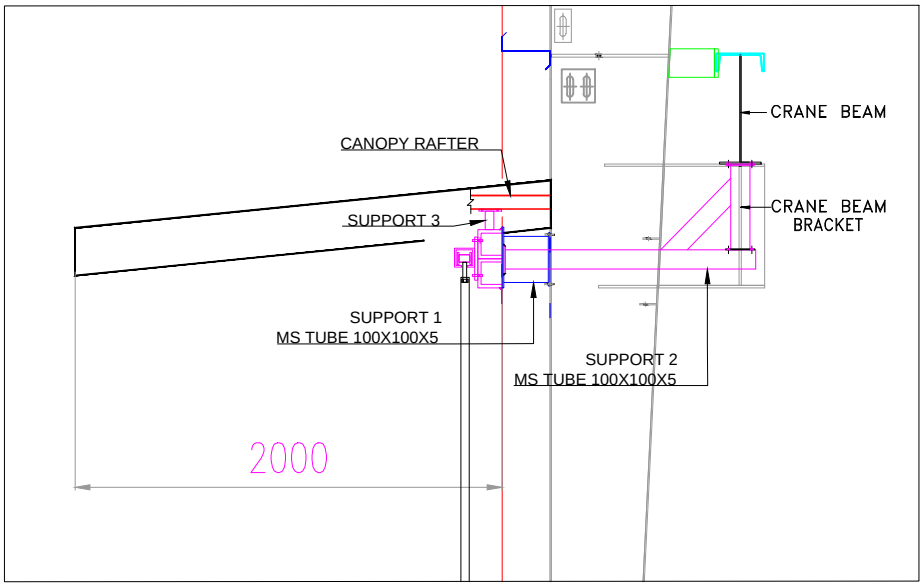



DETAIL'S VIEW 'A'

TOLERANCE - ±10mm

This drawing & design is the property of NIHVA TECHNOLOGIES. Not to be sold or copied to any other concern.

| | | | |
|---|---|---|---|
| TITLE: SLIDING DOOR STRUCTURE DETAILS | | | NIHVA TECHNOLOGIES PVT. LTD. PUNE |
| | NAME | SIGN | DATE |
| DRAWN | SURAJ | | 11-10-2018 |
| CHECK | PRADEEP | | 11-10-2018 |
| APPRD. | R.D | | 11-10-2018 |
| If any queries contact : design@nihva.com | | | |
| ALL DIMENSION ARE IN mm | | | |

NIHVA TECHNOLOGIES PVT. LTD.
Tel : 020 66304033
Website:- www.nihva.com
Email:- info@nihva.com

| | | | |
|---|---|---|---|
| CLIENT -REWARD CONSTRUCTION PVT. LTD | | | |
| PROJECT -REWARD CONSTRUCTION PVT. LTD | | | |
| SITE LOCATION -RANJANGAON | | | |
| DWG. NO. : NIHVA/18-19/0142 | | | REV- 0 |
| SCALE: NTS | WT: | | SHEET: 01 OF 01 |