

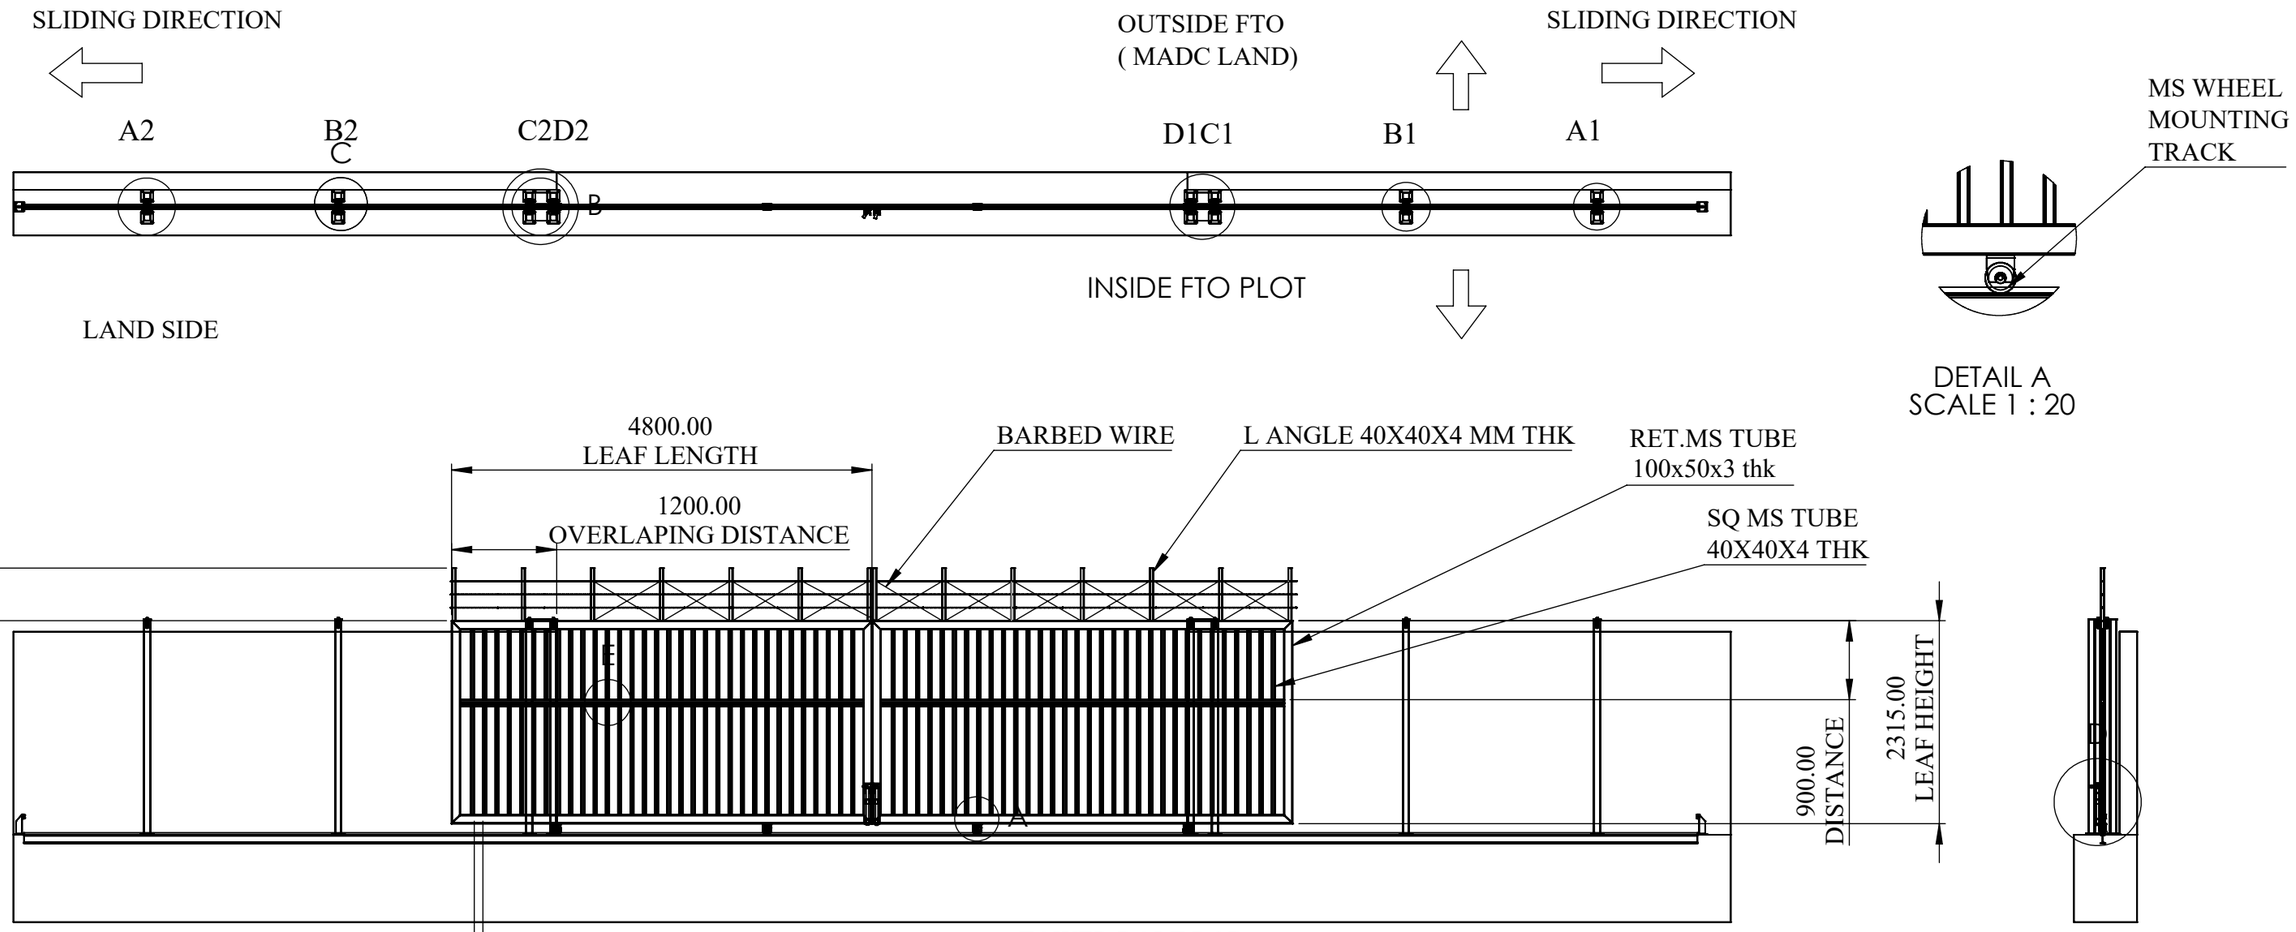


DETAIL A
SCALE 1 : 20

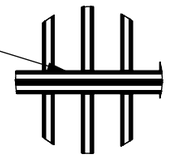


DETAIL E
SCALE 1 : 22

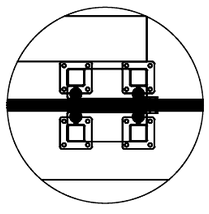


DETAIL B
SCALE 1 : 27

POST AND NYLON
BEARING ASM

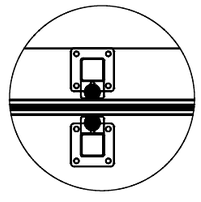

DETAIL C
SCALE 1 : 20

POST2 AND NYLON
BEARING ASM

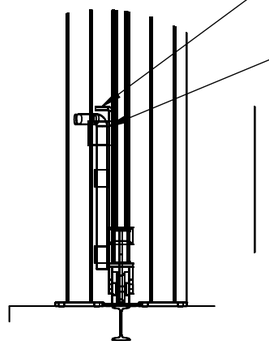

DETAIL D
SCALE 1 : 18

TOWER BOLT LOCKING
ARRANGEMENT

NOTE: 1) GA DRAWING TYPE 02
2) BARBED WIRE DESIGN IS ZIGZAG PATTERN.
3) Total Column-8 (A1,B1,C1,D1 Same as right side add 4 Post)
4) 04 column posts when the gate is in the closed position. (C1,D1) & C2,D2)
5) 08 column posts when the gate is in the open position (A1,B1,C1,D1& A2,B2,C2,D2)

TITLE - GATE AUTOMATION				NIHVA TECHNOLOGIES PVT.LTD.PUNE Website - www.nihva.com
DWG NO - NTPL-290-PM-002			QTY - 1	
	NAME	SIGNATURE	DATE	PROJECT NO - NTPL-290-PM
DRAWN	V.B.		29-07-2025	PRODUCT - BYPARTING SLIDING GATE
CHK'D	B.S.		29-07-2025	SITE LOCATION - AMRAVATI
APPV'D	V.T.		29-07-2025	TYPE 2
if any queries contact - supportautomation@nihva.com				REVISION -00
ALL DIMENSION ARE IN mm			A3	SCALE - SHEET 1 OF 1