

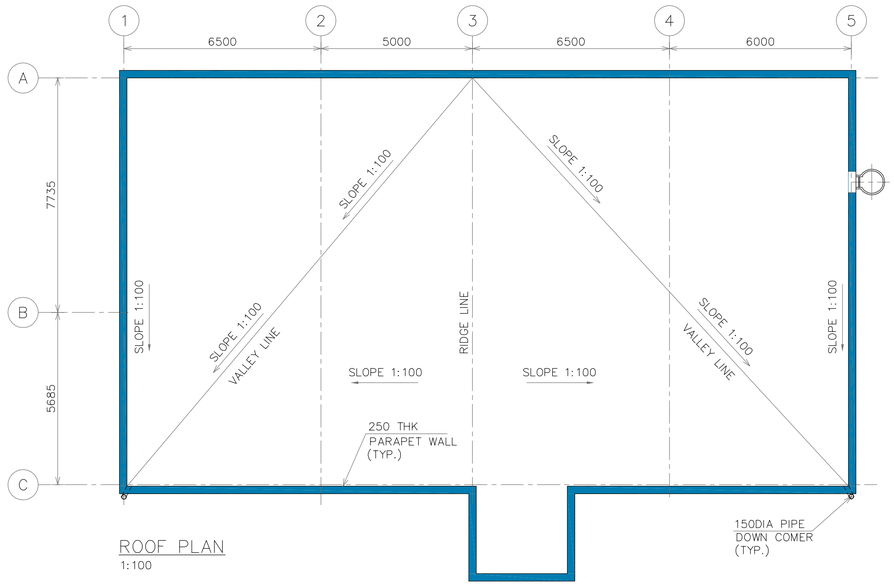



ROOF PLAN
1:100

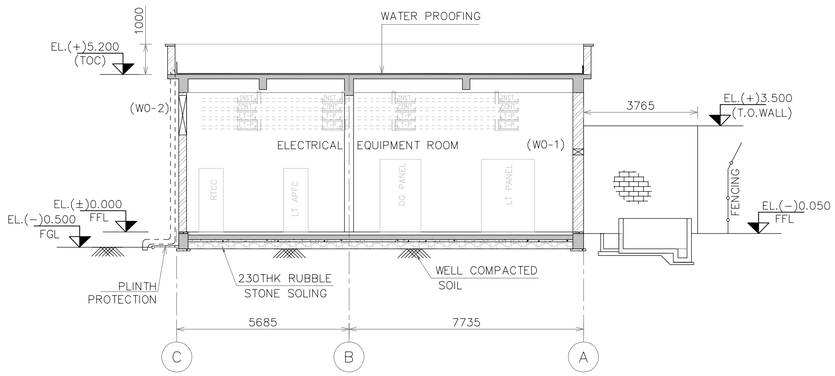


SECTION A-A
1:100

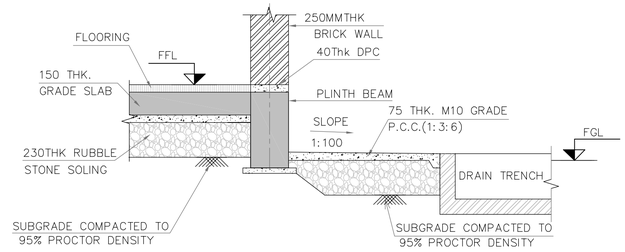


TYP. DETAIL OF PLINTH PROTECTION
1:20

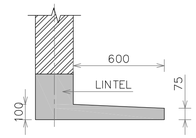


TYPICAL DETAIL OF LINTEL
WITH CHAJJA ALOFT
(300MM PROJECTION ON EITHER SIDE
OF OPENING FOR CHAJJA)
1:20

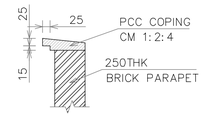


TYP. DETAIL OF COPING
1:10

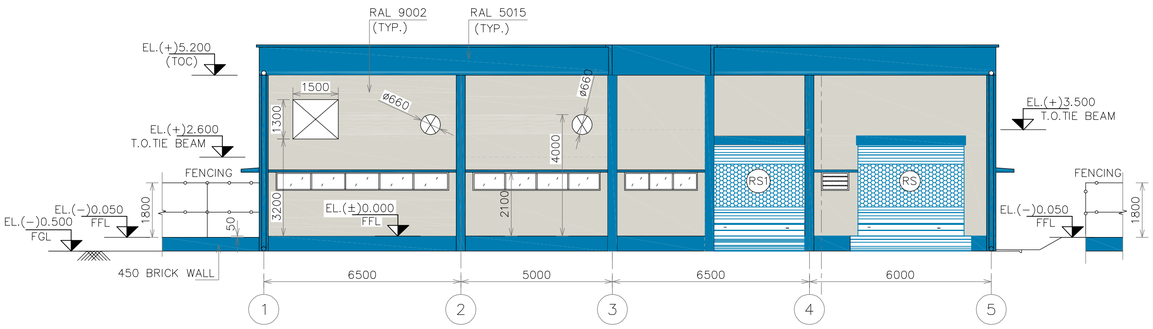



VIEW 1-1
1:100

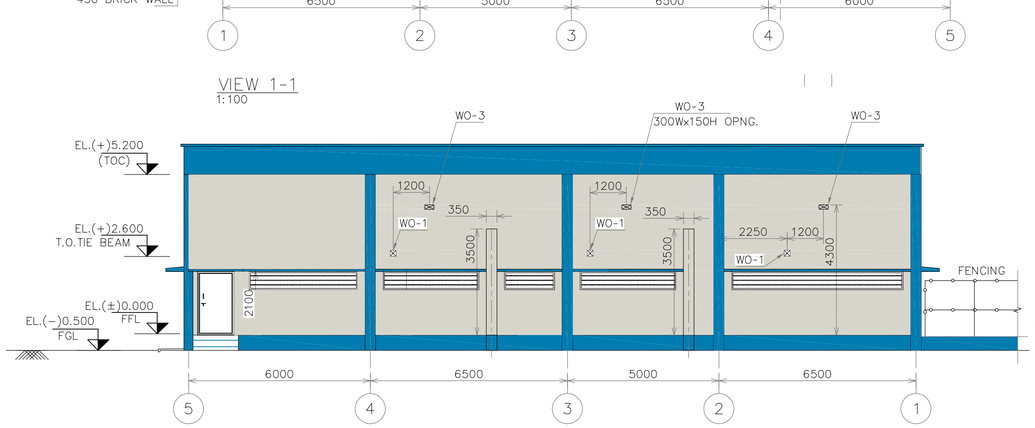

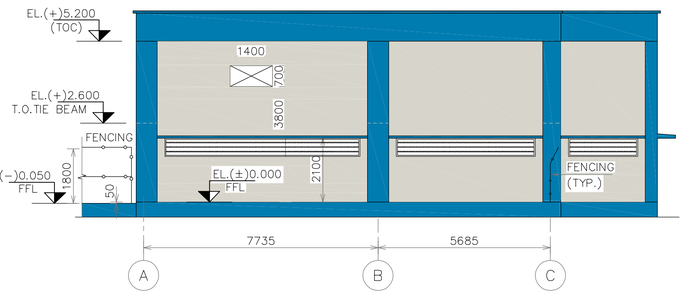


VIEW 2-2
1:100

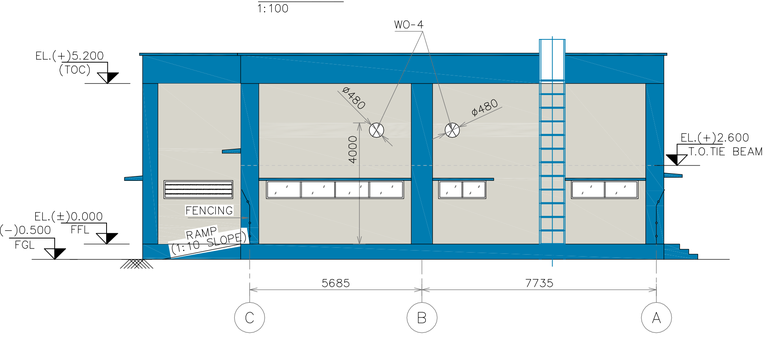

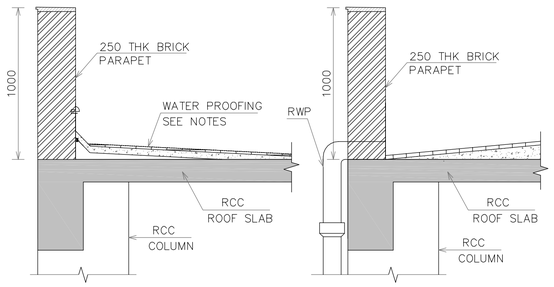

ROOF TREATMENT WITH
WATER PROOFING
1:20

TYP. DETAIL OF RWP
1:20

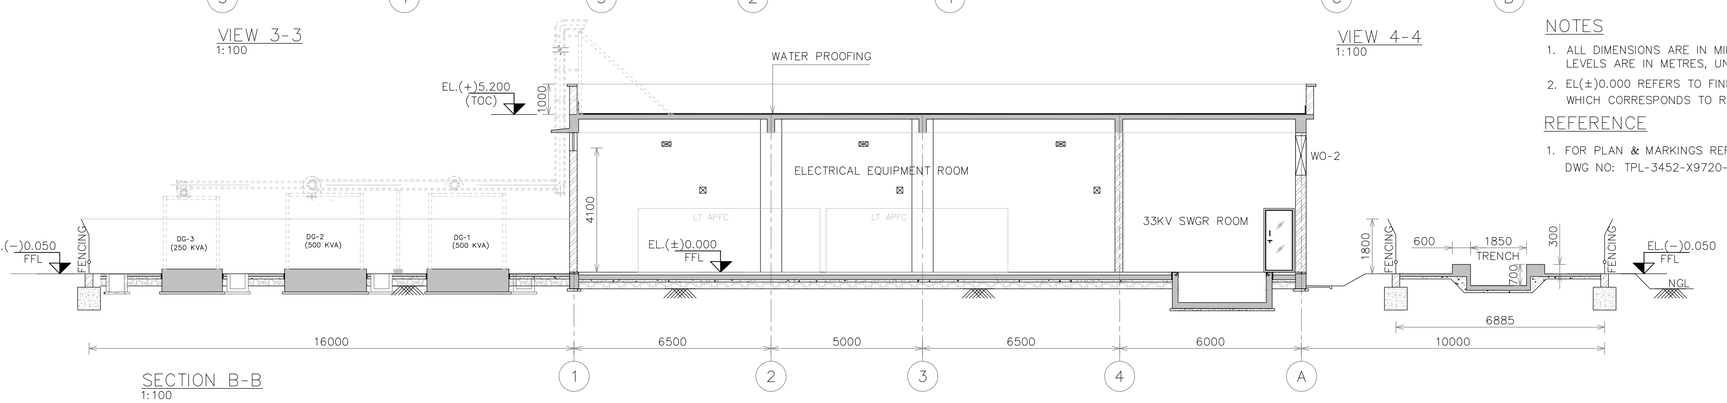

SECTION B-B
1:100

VIEW 3-3
1:100

VIEW 4-4
1:100

NOTES

1. ALL DIMENSIONS ARE IN MILLIMETRES AND LEVELS ARE IN METRES, UNO.
2. EL(±)0.000 REFERS TO FINISHED FLOOR LEVEL WHICH CORRESPONDS TO RL 44.30

REFERENCE

1. FOR PLAN & MARKINGS REFER DWG NO: TPL-3452-X9720-EC-AC-6236 (Sht 1 of 2)

REV.NO.	DATE	REVISION	CIVIL	MECH	ELEC	INST	APPD	DRAWN
			CLEARED					
2	07.01.17	ISSUED FOR APPROVAL					AS	GMN
1	03.01.17	ISSUED FOR APPROVAL					AS	GMN
0	05.12.16	ISSUED FOR APPROVAL					AS	GMN

THIS DRAWING IS PROPERTY OF **"TATA PROJECTS LIMITED"** MUST NOT BE PASSED ON TO ANY PERSON OR BODY NOT AUTHORIZED BY US TO RECEIVE IT NOR BE COPIED OR OTHERWISE MADE USE EITHER IN FULL OR IN PART BY SUCH PERSON OR BODY WITHOUT OUR PRIOR PERMISSION IN WRITING.

EPC CONTRACTOR
TATA PROJECTS LIMITED
H. NO.1-7-80 TO 87, "MITHONA TOWERS – 1"
PRENDERGHAST ROAD, SECUNDERABAD – 500003.

PROJECT TITLE
PLANT FACILITY FOR
MADHEPURA ELECTRIC LOCOMOTIVE PRIVATE LIMITED
AT MADHEPURA, BIHAR.

OWNER
MADHEPURA ELECTRIC LOCOMOTIVE PRIVATE LIMITED

OWNER A/E CONSULTANT :
SEMAC CONSULTANTS PVT LTD
6-1-276, 2ND FLOOR, ARCHANA BLOCK,
CONJEEVARAM HOUSE, PADMARAO NAGAR
SECUNDERABAD – 500025.

	SIGNATURE	DATE
DRAWN	GMN	05.12.16
DESIGNED	SR	05.12.16
CHECKED	AS	05.12.16
DEPT.HEAD	AS	05.12.16

DWG. TITLE:
FACTORY AREA
ELECTRICAL SUBSTATION BUILDING
ARCHITECTURAL ELEVATIONS & SECTIONS

RELEASED FOR		
	INFORMATION	
	APPROVAL	
	ENGINEERING	
	CONSTRUCTION	✓

DEPT. CIVIL | JOB NO. 0000 | SCALE: – | SHEET: 2 OF 2 | SIZE : A1
FILE NAME. ALSTOM-M-AR-STF-101
DWG.NO. TPL-3452-X9720-EC-AC-6236
REV./ISSUE R2