

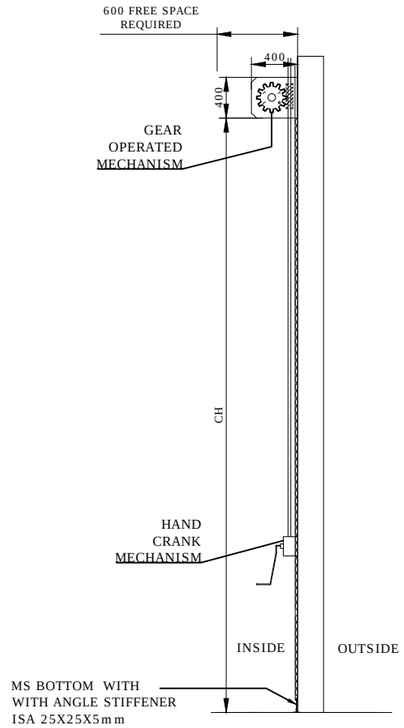



SIDE VIEW

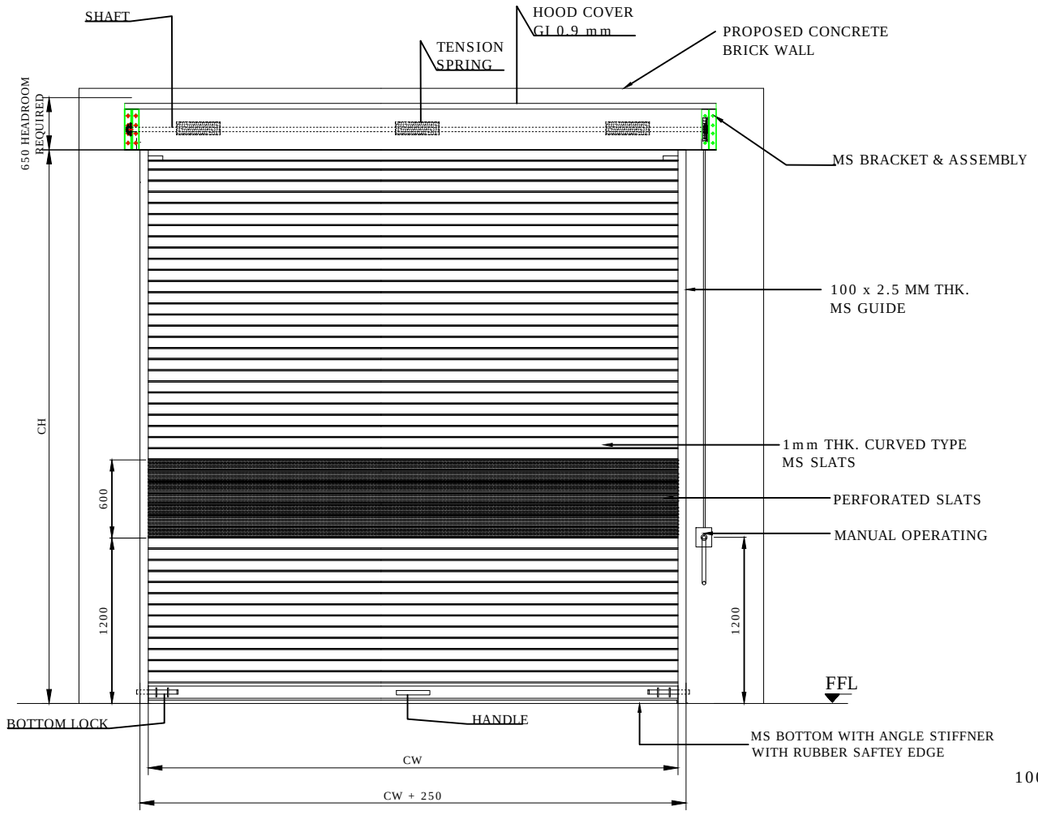


INSIDE ELEVATION

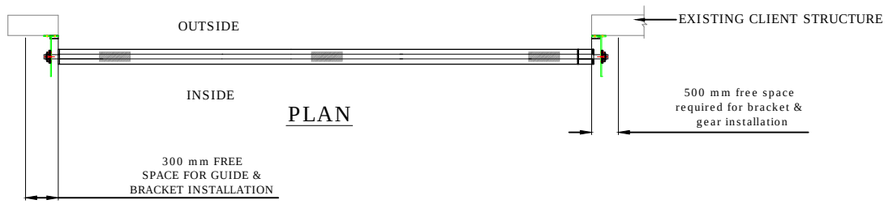

PLAN

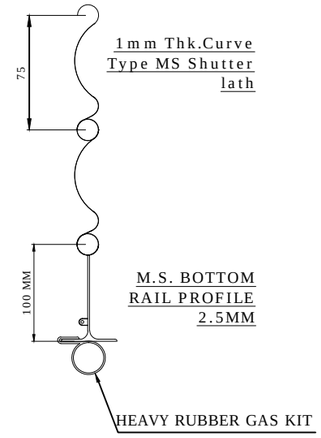

M.S. BOTTOM RAIL PROFILE 2.5MM

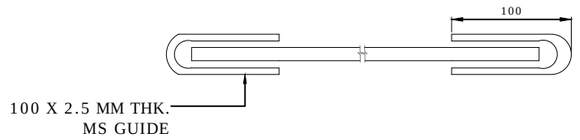

RAL 9007	GREY AL.	APPROVED
RAL 9010	PURE WHITE	
RAL 9002	GREY WHITE	
RAL 7035	LIGHT GREY	
RAL 5002	ULT. M. BLUE	
RAL CODE	RAL COLOR	APPROVED

TOLERANCE - ±10mm

NOTE-
1. ALL CIVIL WORK WILL BE CLIENT'S SCOPE.
2.IF STRUCTURE REQUIRED FOR SHUTTER IS IN CLIENT'S SCOPE.
3. MOUNTING LOCATION: INSIDE AREA
4. MOUNTING SURFACE ON CONCRETE BRICK WALL.

REV 01- (14/02/2022)
1. ADDED APPROVED RAL COLOR.
2. MENTIONED MOUNTING OF SHUTTER ON BRICK WALL.
3. MENTIONED MOUNTING LOCATION INSIDE.
4. BOTTOM BRACKET SIZE CHANGED TO 100 MM.

SR NO	(CW) CLEAR WIDTH	(CH) CLEAR HEIGHT	QUANTITY
2	4000	3400	01 NO
1	4000	3700	01 NO

This drawing & design is the property of NIHVA TECHNOLOGIES. Not to be sold or copied to any other concern.

TITLE: GEAR OPERATED ROLLING SHUTTER

	NAME	SIGN	DATE
DRAWN	G.I.P		17.01.2022
CHECK	A.K.		17.01.2022
APPRD.			

NIHVA TECHNOLOGIES PVT. LTD.
Website:- www.nihva.com
NIHVA TECHNOLOGIES PVT. LTD. PUNE
Tel : 020 66304033
Email:- info@nihva.com

CLIENT -SCON PROJECTS
PROJECT - ROLLING SHUTTER
SITE LOCATION - NASHIK

If any queries contact : design@nihva.com
DWG. NO. : NIHVA/21-22/CLT/0313
REV- R01
ALL DIMENSION ARE IN mm
SCALE: NTS
WT:
SHEET: 01 OF 01