



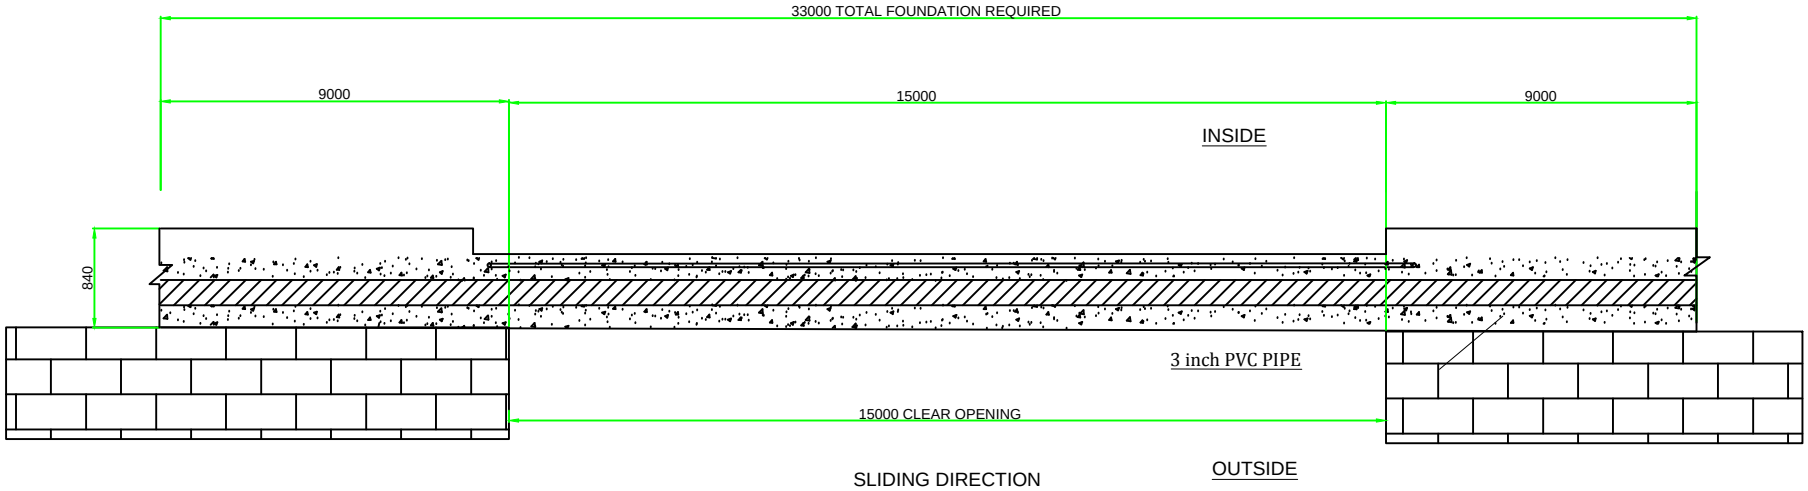

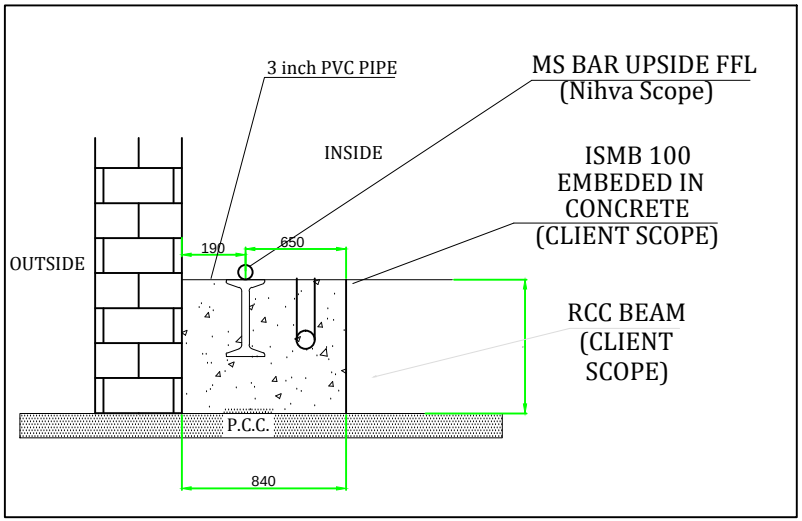

15m SLIDING GATE FOUNDATION

This drawing & designing is the property of NIHVA TECHNOLOGIES. Not be sold or copy to any other concern.

TITLE	ALL DIMENSION ARE IN mm	NIHVA TECHNOLOGIES PVT. LTD.
SLIDING GATE FOUNDATION		NIHVA TECHNOLOGY PVT. LTD. PUNE Tel : 020 66304033 Email:- info@nihva.com Website:- www.nihva.com
CLIENT APPROVAL		

	SIGN	DATE	
DRAWN	OMKAR	11/03/16	CLIENT - HYOSUNG T& D
CHECK	ANIL	11/03/16	PROJECT -
REV.	00		SITE -PUNE
APPRD.			DWG. NO. - NIHVA/15-16/242
MFG			SCALE: 01 | WT: | SHEET: 01 OF 01
Ref. No.			If any queries contact : projects@nihva.com