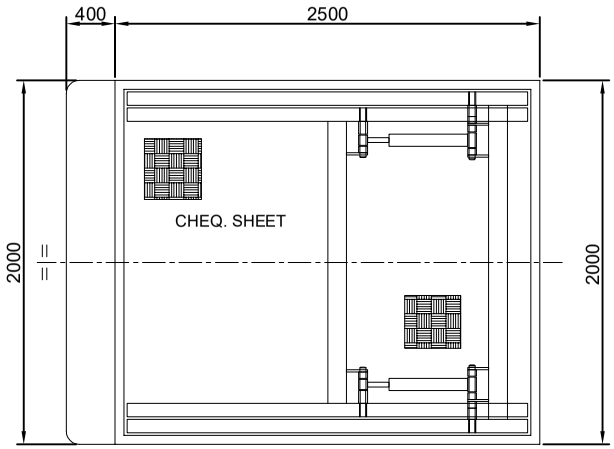
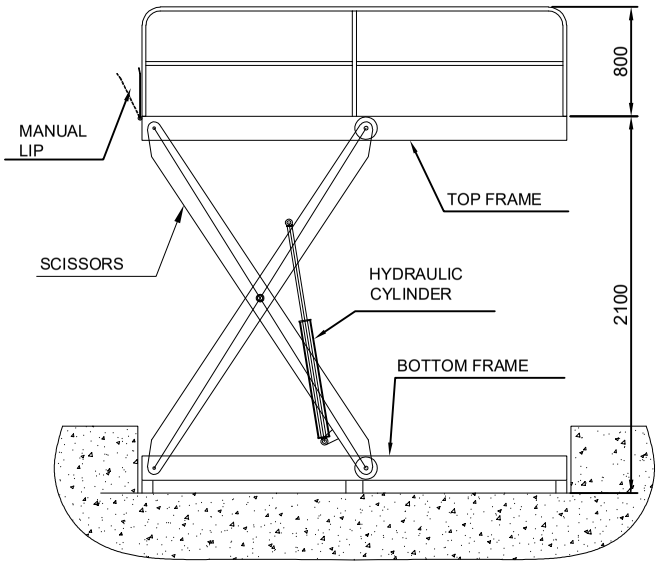
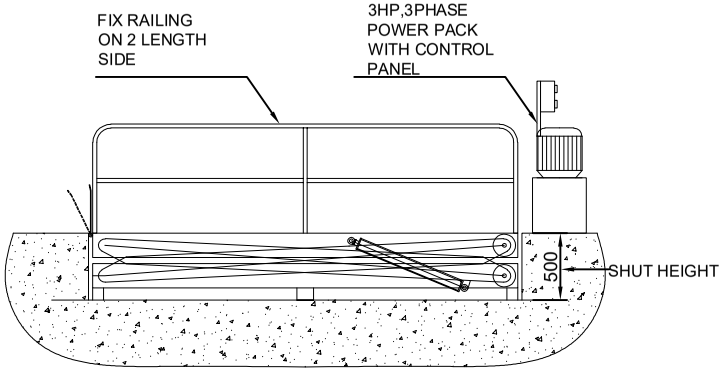


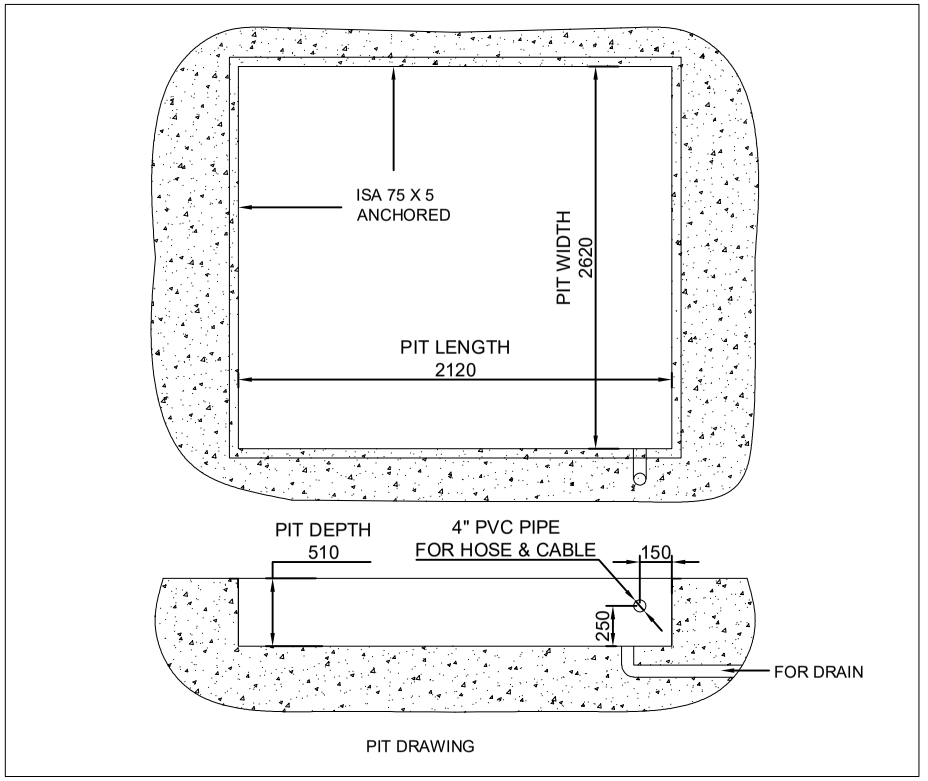

TOP VIEW




OPEN HEIGHT FRONT VIEW




CLOSED HEIGHT FRONT VIEW




PIT DRAWING

NOTE :

1. PIT FOR SCISSORLIFT HAS TO BE DIAGONALLY WITHIN 3-5 MM
2. BASE OF THE PIT HAS TO BE IN WATER LEVEL AND RIGHT ANGLE TO THE VERTICAL SIDE WALLS
3. PROPER ARRANGEMENT FOR ROUTING HOSES AND CABLES HAVE TO BE MADE DEPENDING ON SITE CONDITIONS AND POSITION OF POWER PACK
4. COVERING REQUIRED FOR CABLES AND RELATED CIVIL WORK IS IN CLIENTS SCOPE
5. WATER DRAINAGE AND PIT CLEANING NEEDS TO BE CONSIDERED AND DONE BY CLIENT
6. PIT & ALL CIVIL WORK IS IN CLIENT SCOPE.
7. TOLERANCE ± 10 MM.

| | |
|---|---|
| SAFETY RAILING | 800 MM HT |
| POWER PACK | 3HP,3PHASE |
| MAX HT | 2100MM |
| LIFT HT | 1600 MM |
| SHUT HT | 500 MM |
| PLATFORM SIZE | 2000W x 2500L |
| CAPACITY | 1.5 TON |

| Rev No. | Revision | Date | Revised By |
|---|---|---|---|

This drawing & design is the property of NIHVA TECHNOLOGIES. Not to be sold or copied to any other concern.

TITLE:- PIT MOUNTED SCISSOR LIFT

| | NAME | DATE | SIGN |
|---|---|---|---|
| DRAWN | SUJATA.B | 25/10/2021 | |
| CHECK | G.PATIL | 25/10/2021 | |
| APPRD. | A.KURHADE | 25/10/2021 | |

If any queries contact : design@nihva.com

ALL DIMENSION ARE IN mm

NIHVA TECHNOLOGIES PVT. LTD.
NIHVA TECHNOLOGIES PVT. LTD. PUNE
Tel : 020 66304033
Email:- info@nihva.com
Website:- www.nihva.com

CLIENT - EMCURE PHARMACEUTICALS LIMITED

LOCATION - AHMEDABAD

PRODUCT - SCISSOR LIFT

DWG NO:-NIHVA\21-22\0254 | REV- 0

SCALE: NTS | SCALE:-- 1:1 | SHEET: 01 OF 01