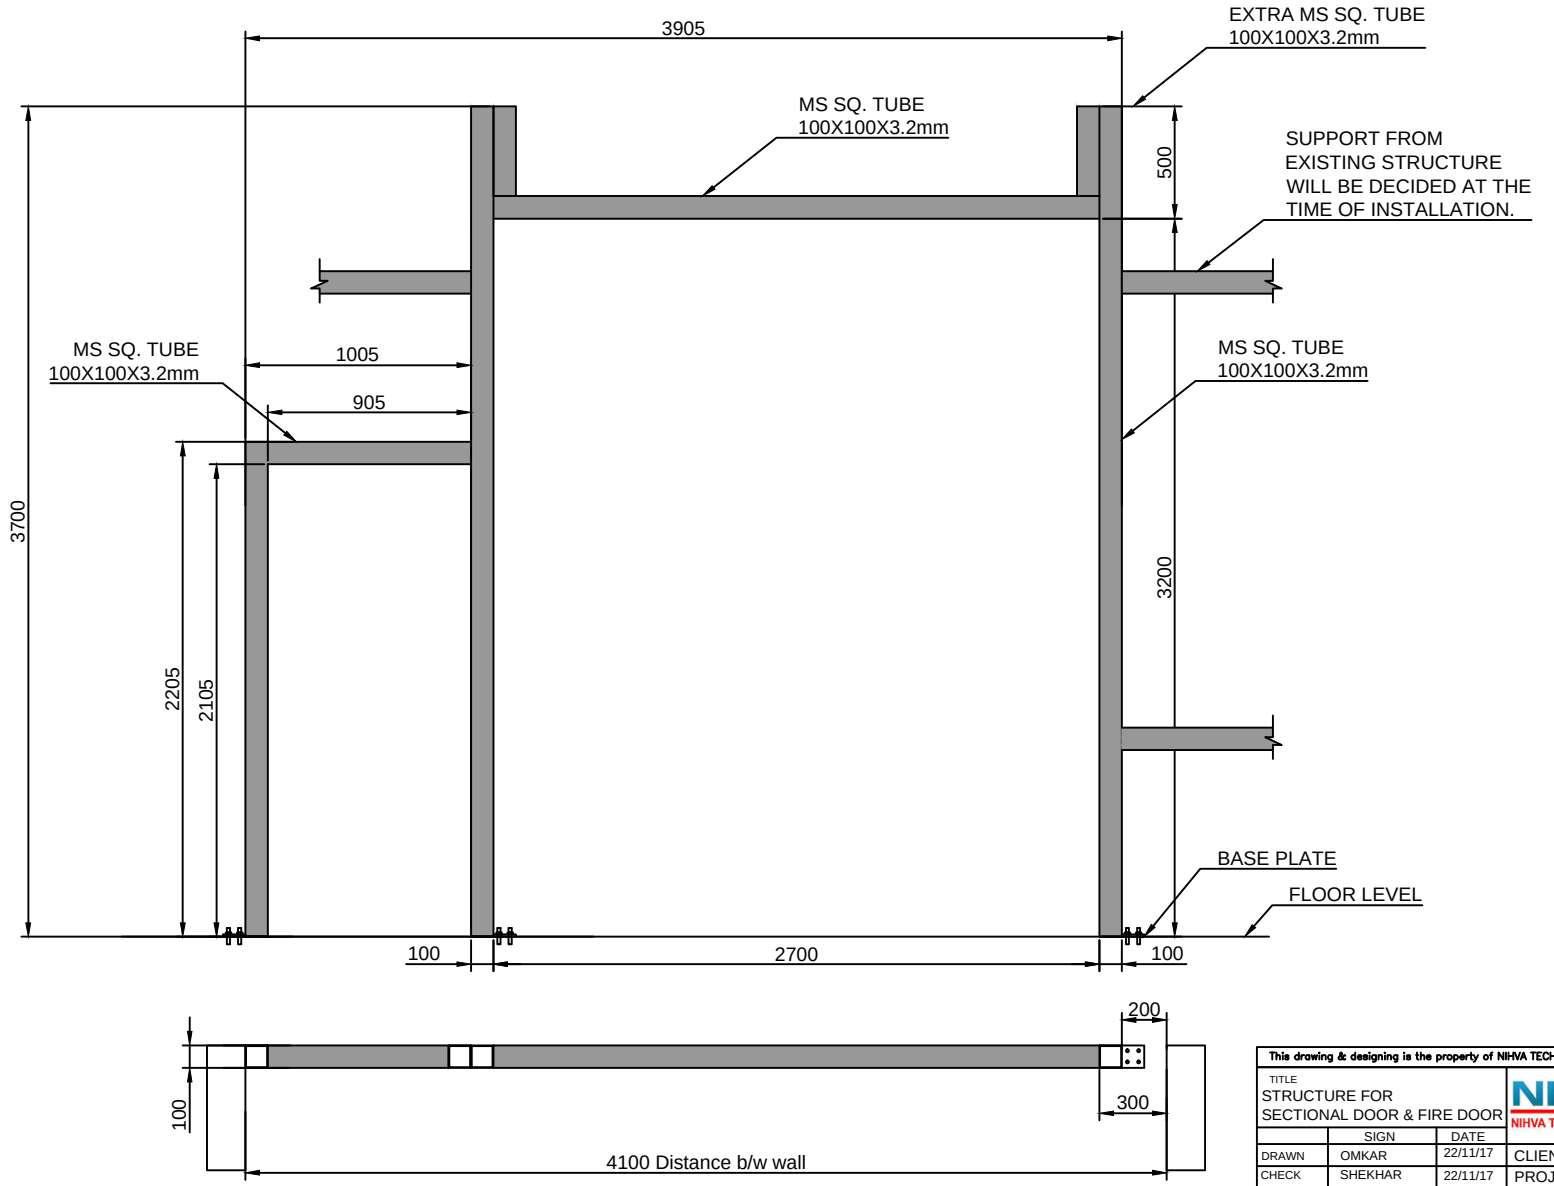

This drawing & designing is the property of NIHVA TECHNOLOGIES. Not to be sold or copied to any other concern.

TITLE: STRUCTURE FOR SECTIONAL DOOR & FIRE DOOR	NIHVA TECHNOLOGIES PVT. LTD.	NIHVA TECHNOLOGIES PVT. LTD. PUNE Tel : 020 66304033 Email:- info@nihva.com Website:- www.nihva.com

	SIGN	DATE
DRAWN	OMKAR	22/11/17
CHECK	SHEKHAR	22/11/17
APPROVAL	SHEKHAR	22/11/17

CLIENT - FERRERO INDIA PVT. LTD.		
PROJECT -		
SITE - BARAMATI		
DWG. NO. : NIHVA/17-18/0286/R01		REV-1
SCALE: NTS	WT:	SHEET: 01 OF 01

If any queries contact : design@nihva.com

ALL DIMENSION ARE IN mm