
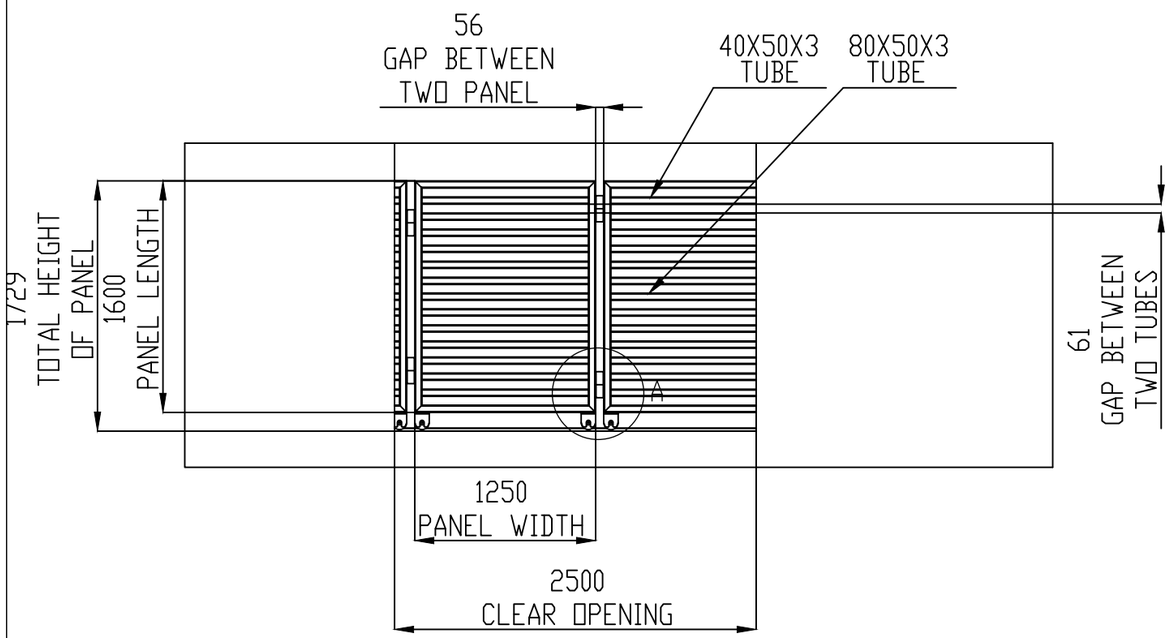
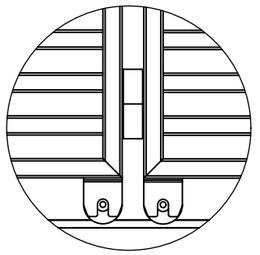



DETAIL A
SCALE 1 : 15

WHEEL ASM.

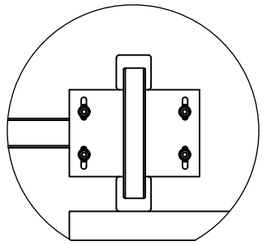


DETAIL B
SCALE 1 : 20


POST AND ROLLER
BEARING ASM.

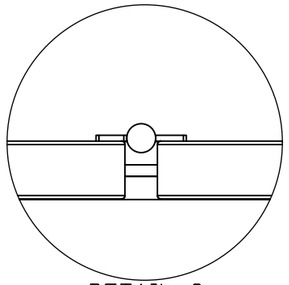

DETAIL C
SCALE 1 : 10

HINGES ASM.

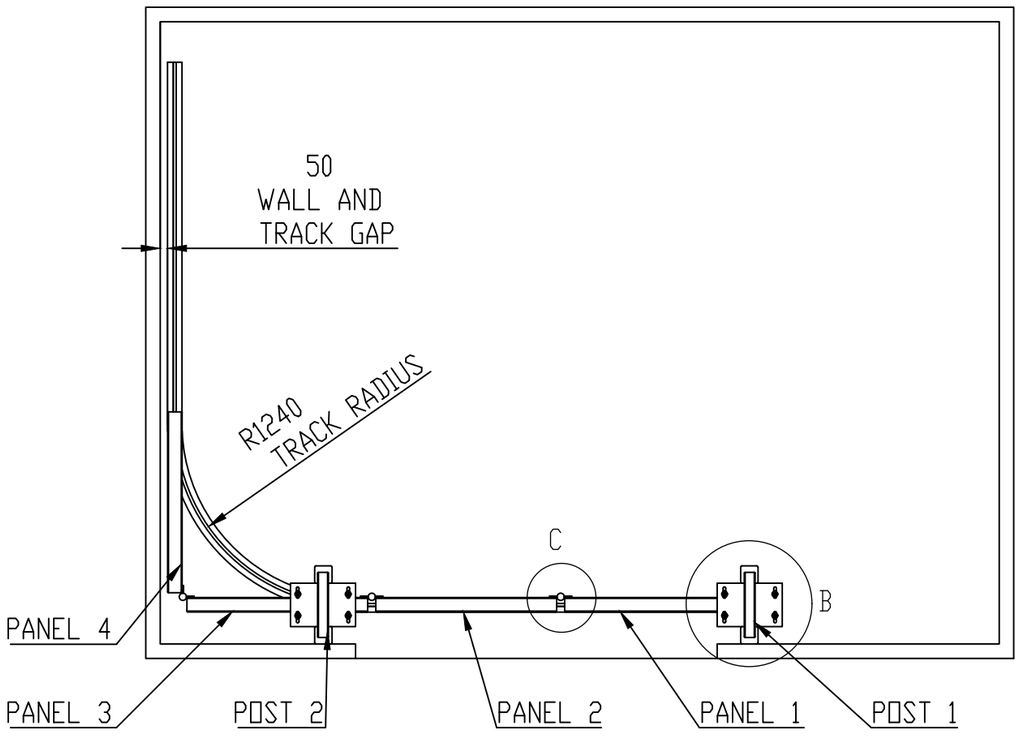

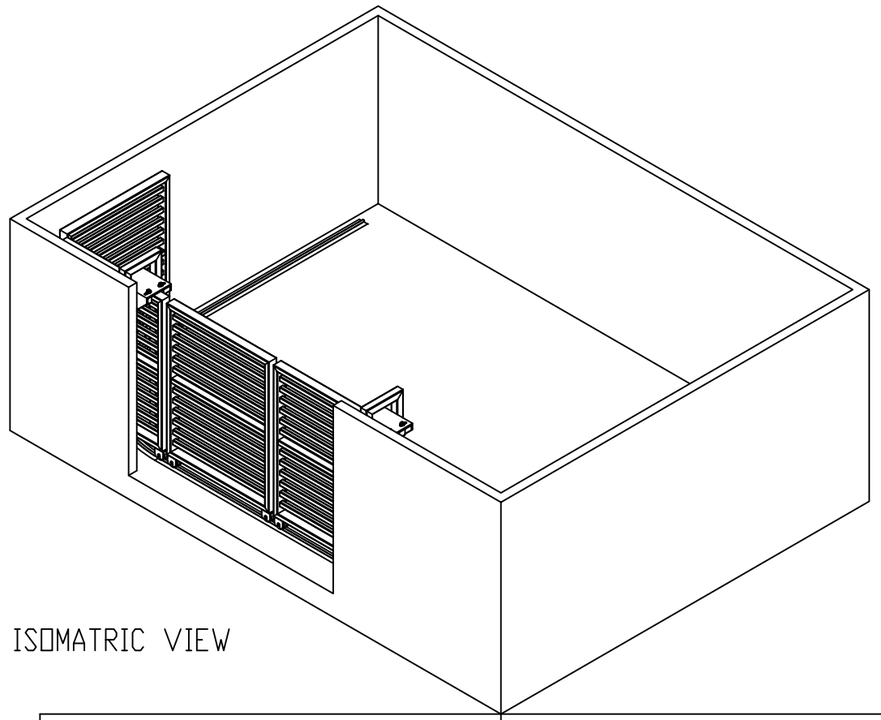ISOMATRIC VIEW

| | | | | |
|---|---|---|---|---|
| TITLE - GATE AUTOMATION | | | | NIHVA TECHNOLOGIES PVT.LTD.PUNE<br>Website - www.nihva.com |
| DWG NO - NTPL268-PM | | | QTY - 1 | |
| | NAME | SIGNATURE | DATE | PROJECT NO - NTPL-000-PM |
| DRAWN | V.G | | 22-05-2025 | PRODUCT - SLINDING FOLDING GATE |
| CHK'D | S.W. | | 22-05-2025 | SITE LOCATION - LUCKNOW |
| APPV'D | V.T. | | 22-05-2025 | |
| if any queries contact - supportautomation@nihva.com | | | | REVISION - 01 |
| ALL DIMENSION ARE IN mm | | | A3 | SCALE - SHEET 1 OF 1 |