

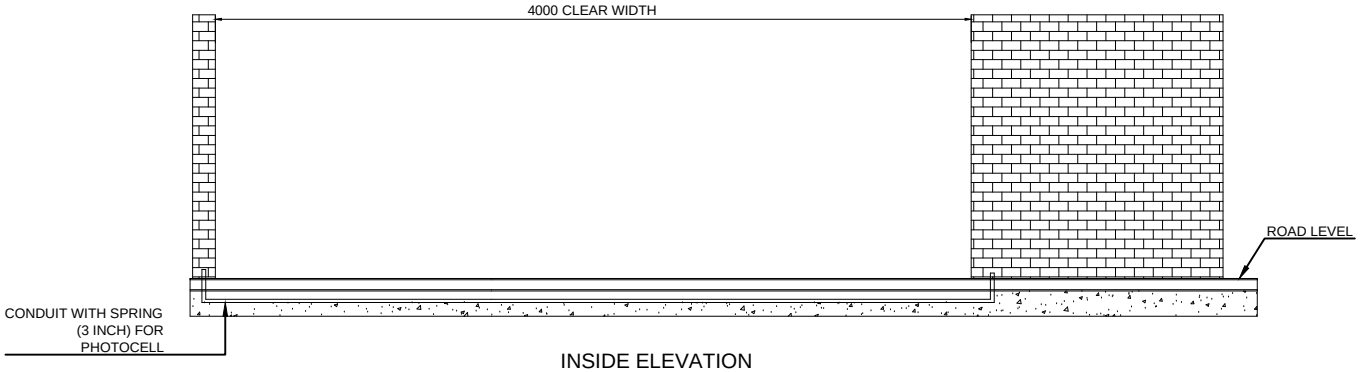


INSIDE ELEVATION

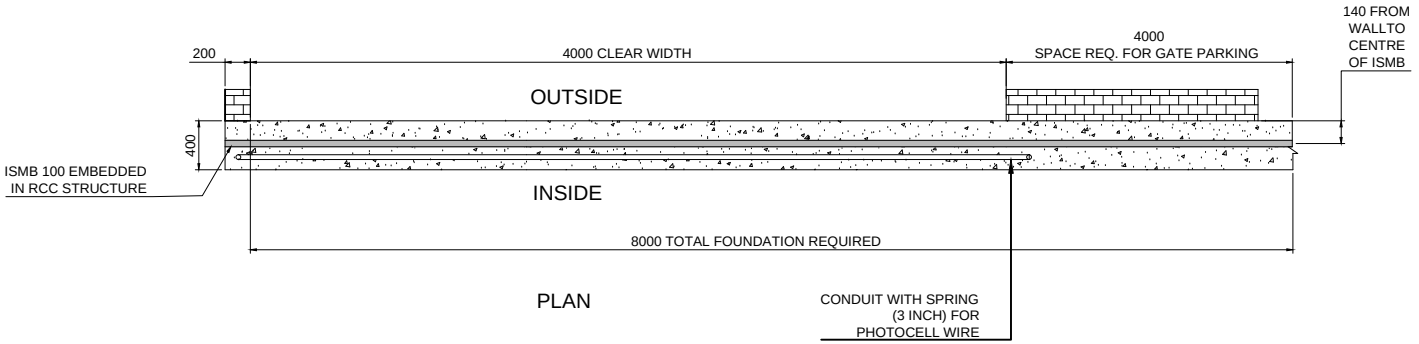

PLAN

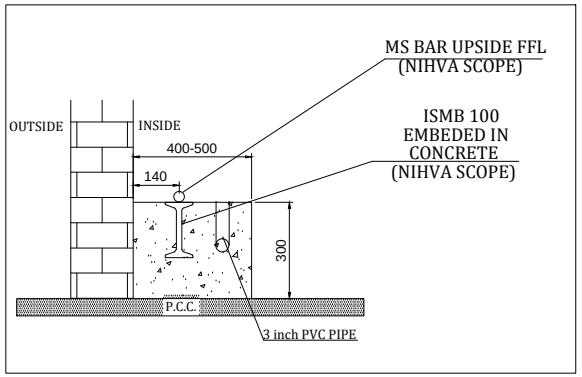

4.0m SLIDING GATE FOUNDATION

ISMB 100 X 50 X 8200L = 1 NO/GATE

This drawing & design is the property of NIHVA TECHNOLOGIES. Not to be sold or copied to any other concern.

TITLE	FOUNDATION FOR 4M SLIDING GATE			NIHVA TECHNOLOGIES PVT. LTD. PUNE Tel : 020 66304033 Email:- info@nihva.com Website:- www.nihva.com
	NAME	SIGN	DATE	
DRAWN	P.A		04.11.19	CLIENT - DHAMALE
CHECK	G.J		04.11.19	PROJECT -
REV.				SITE LOCATION - NIGADI, PUNE
APPROVAL				DWG. NO. : NIHVA/19-20/0145
If any queries contact : projects@nihva.com				SCALE: NTS WT: SHEET: 01 OF 01
ALL DIMENSION ARE IN mm				