

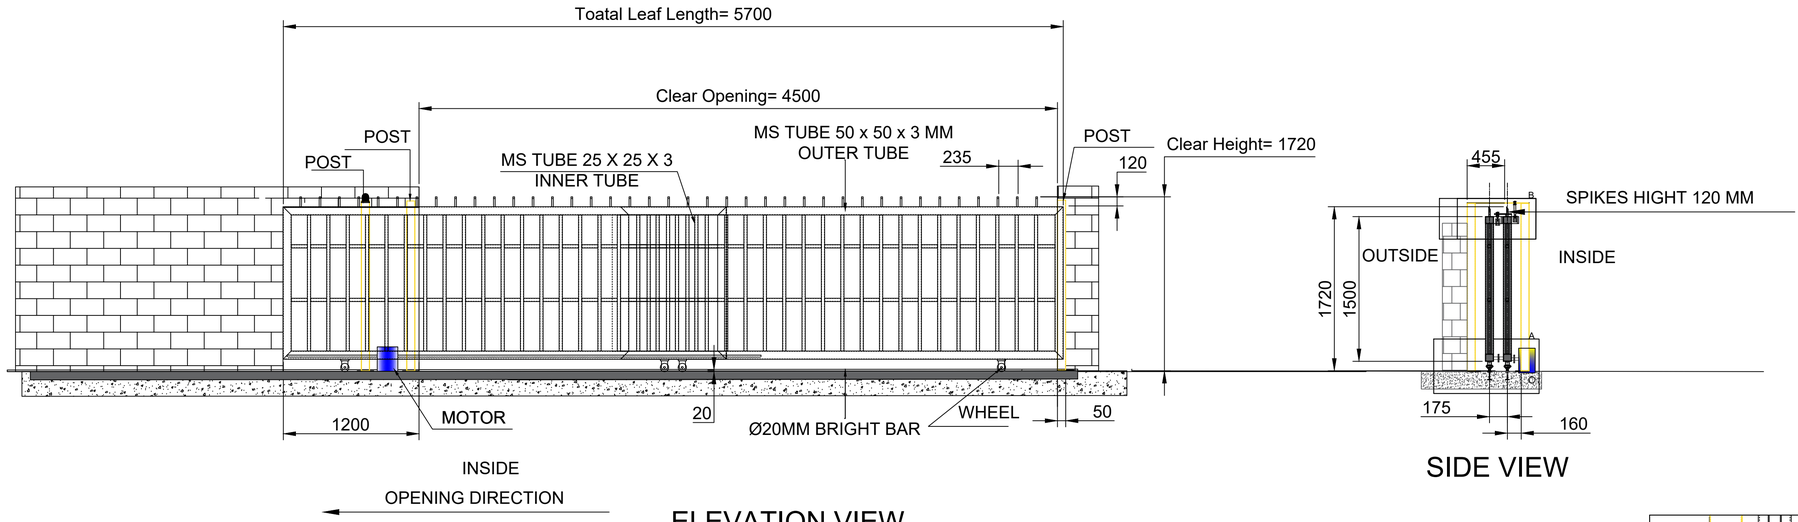


ELEVATION VIEW


SIDE VIEW

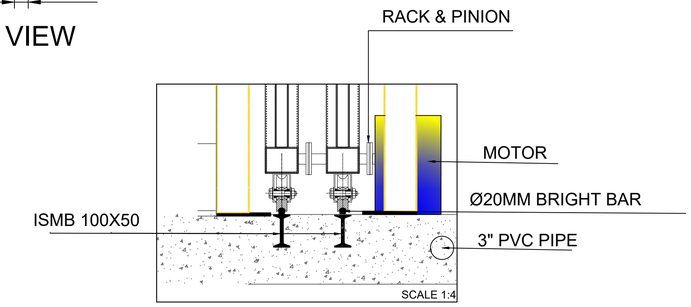

DETAIL A

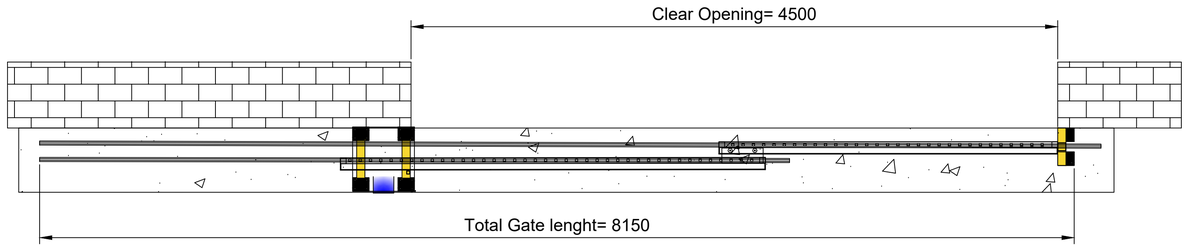

PLAN

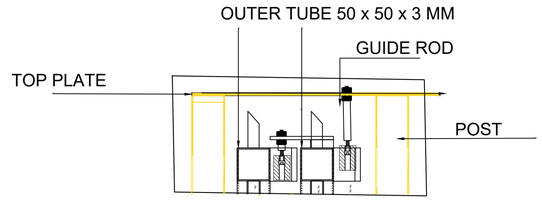

DETAIL B
SCALE 1:4

Technical Specs of Motorized Sliding Gate

1. Opening length - 4500mm
2. Gate Height - 1720mm
3. Parking length required - 3400+100 mm
4. Outer tube size - MS SHS 50 x 50 x 3 mm
5. Inner tube size - MS SHS 25 x 25 x 3 mm
6. Bottom Rail - Bright bar Ø20mm
7. Post size - MS SHS 50 x 50 x 3 mm
8. SURFACE FINISH: POWDER COATING WILL BE SUGGESTED BY CLIENT (RAL CODE)

Note-

1. All dimension are in mm.
2. All civil work is under client scope.
3. 3" PVC pipe in the foundation to be provided by client.
4. Power supply single phase 230v, 50hz.is in client scope
5. Cable for power supply 2.5 sqmm 3 core
6. Cable for photocell - 1.5 sqmm 4 core

RAL CODE	SHADE	COLOUR
RAL 9001	CREAM	
RAL 9002	GREY WHITE	
RAL 9010	PURE WHITE	
RAL 5002	ULTRAMARINE BLUE	
RAL 7035	LIGHT GREY	
RAL 7001	SILVER GREY	

Rev No.	Revision	Date	Revised By
001	GATE CONVERTED TO 2 LEAF AS PER PARKING AVAILABLE	16/08/2022	M. SUTAR
000	RELEASE AS GA DRAWING	04/08/2022	M. SUTAR
CAD PATH:-			

This drawing & design is the property of NIHVA TECHNOLOGIES. Not to be sold or copied to any other concern.

TITLE:-
MOTORISED SLIDING GATE

NIHVA TECHNOLOGIES PVT. LTD.
NIHVA TECHNOLOGIES PVT. LTD. PUNE
Tel : 020 66304033
Email:- info@nihva.com
Website:- www.nihva.com

	NAME	DATE	SIGN
DRAWN	M.SUTAR	04-08-2022	
CHECK	M.SUTAR	04-08-2022	
APPRD.	A.KURHADE	04-08-2022	

If any queries contact : design@nihva.com

ALL DIMENSION ARE IN mm

CLIENT - MEGAWIDE CONSTRUCTION

LOCATION - GMR GOA INTERNATIONAL AIRPORT LIMITED

PRODUCT - MOTORISED SLIDING GATE

DWG NO:- NIHVA/22-23/CLT/0099 | REV- 0

SCALE: NTS | SCALE:-- 1:1 | SHEET: 01 OF 01