


Abbrevation's:
WOW-Wall Opening Width
WOH-Wall Opening Height
DH- Door Height
UC-Under Cut
FFL-Finished Floor Level

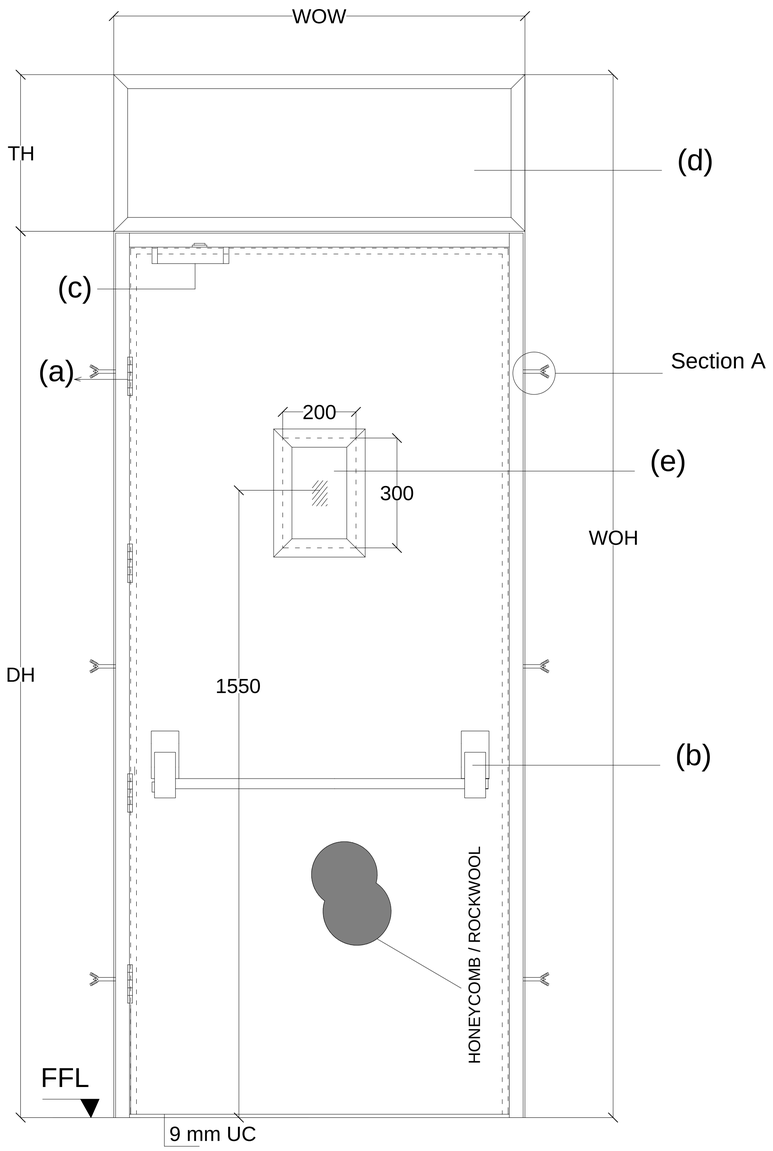


ELEVATION

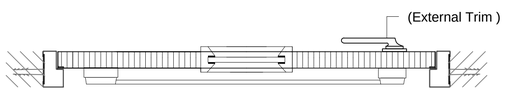


Top View

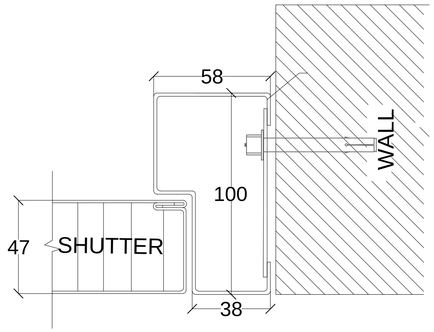


## ASSESORIES DETALES

(a) HINGES: SS hinges 100x75x3mm

(b) LOCK : Mortise Lock with half cylinder.
Panic Bar
Outer trim

(c) DOOR CLOSER : F 8500

(d) FIXED METAL SHEET PANEL

(e) VISION PANEL- 5mm THK. FIRE GLASS SIZE- 200X300mm.

Shutter thickness : 47 mm
Frame Sheet thick : 1.20mm
Shutter sheet thick : 0.80mm
Fixing : On Soliid Brick plasterd wall with Anchors

NOTE:- *All Dimensions are in mm.
*Tolerance:-All Linear Dimensions ±3mm,Others ±0.5mm.
*The Drawing Is For Location of Hardware only. Drawing Does Not Represent The Hardware For More Clarity, Please Go Through Hardware Broucher.

## Door size

| WOW | WOH | DH | TH | TYPE 1 | TYPE 2 | TYPE 3 | TYPE 4 | QUANTITY |
|---|---|---|---|---|---|---|---|---|
| 1191 | 3000 | 2400 | 600 | | | | 1 | 1 |
| 1180 | 3121 | 2400 | 721 | | | | 1 | 1 |
| 1180 | 3029 | 2400 | 629 | | | 1 | | 1 |
| 1195 | 3033 | 2400 | 633 | | | 1 | | 1 |
| 1205 | 3017 | 2400 | 617 | | | 1 | | 1 |
| 1194 | 2958 | 2400 | 558 | | | | 1 | 1 |
| 1192 | 3000 | 2400 | 600 | | | 1 | | 1 |
| 1198 | 2977 | 2400 | 577 | | | | 1 | 1 |

COLOR - SIGNAL RED(RAL 3001)

This drawing & designing is the property of NIHVA TECHNOLOGIES. Not to be sold or copied to any other concern.

TITLE
FIRE RATED DOORS
WITH FIXED GLASS

NIHVA TECHNOLOGIES PVT. LTD.
NIHVA TECHNOLOGIES PVT. LTD. PUNE
Tel : 020 66304033
Email:- info@nihva.com
Website:- www.nihva.com

| | SIGN | DATE |
|---|---|---|
| DRAWN | OMKAR | 03/08/17 |
| CHECK | SHEKHAR | 03/08/17 |
| REV. | 00 | |
| APPROVAL | | |

CLIENT -
PROJECT -
SITE -
DWG. NO. : NIHVA/17-18/VDR/ 0072/R01

If any queries contact : projects@nihva.com
SCALE: NTS | WT: | SHEET: 01 OF 01
ALL DIMENSION ARE IN mm