


NOTE : ~ PLEASE MAINTAIN 8 MM GAP BETWEEN TWO LIP BUSHES.

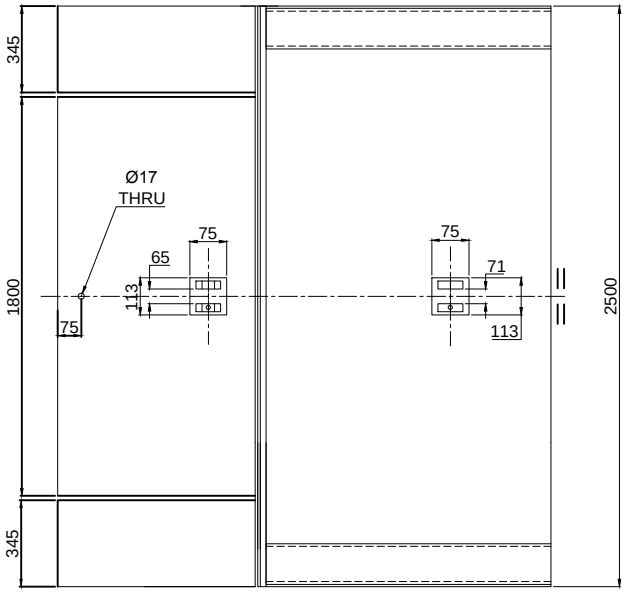



1

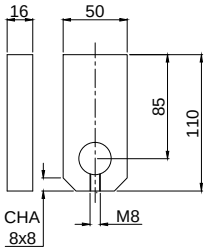

2

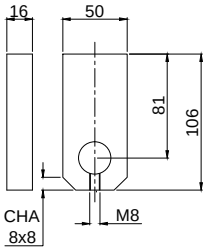

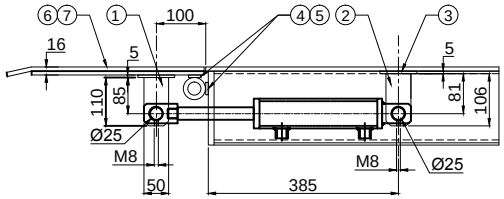

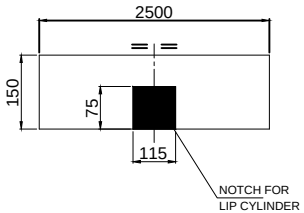

NOTE:~ MTL : MS

PART NO.	PART NAME	DESCRIPTION	QTY
1.	FLAT	50 X 16 X 113L	2 NOS
2.	FLAT	50 X 16 X 110L	2 NOS
3.	FLAT	75 X 5 X 113L	2 NOS
4.	FLAT	25 X 5 X 80L	14 NOS
5.	FLAT	25 X 5 X 60L	8 NOS
6.	CHEQ.SHEET	300 X 8 X 1800L	1 NO
7.	CHEQ.SHEET	250 X 8 X 1800L	1 NO
8.	CHEQ.SHEET	300 X 8 X 345L	2 NOS
7.	CHEQ.SHEET	250 X 8 X 345L	2 NOS

REV NO	DRAWN	DATE	DESCRIPTION
R02	P.A	20.07.20	1. LIP SIZE CHANGE.
R01	P.A	18.12.18	1. LIP SIZE CHANGE.

TOLERANCE - ±5mm

This drawing & design is the property of NIHVA TECHNOLOGIES. Not to be sold or copied to any other concern.

TITLE

LIP CYL MOUNTING

NIHVA TECHNOLOGIES PVT. LTD.

NIHVA TECHNOLOGIES PVT. LTD. PUNE
Tel : 020 66304033
Email:- info@nihva.com
Website:- www.nihva.com

	NAME	SIGN	DATE
DRAWN	P.A		12.12.18
CHECK	P.A		12.12.18
APPRD.	P.A		12.12.18

CLIENT -

PROJECT - DLAG1010

SITE LOCATION -

If any queries contact : design@nihva.com

DWG. NO. : NIHVA/18-19/MFG/DLAG1010/006/R02

ALL DIMENSION ARE IN mm

SCALE: NTS | WT: | REV- R01