
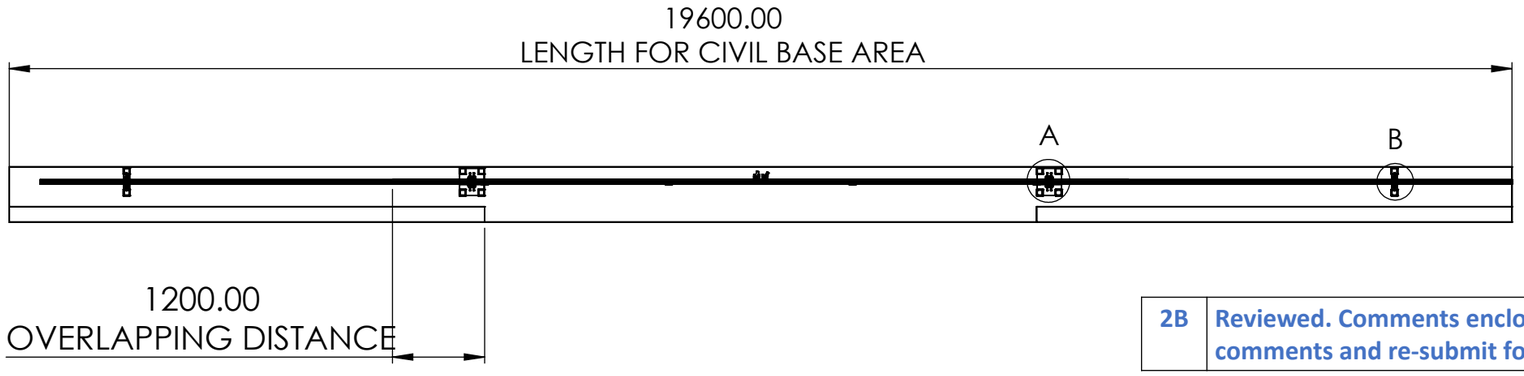



2B	Reviewed. Comments enclosed. Incorporate the comments and re-submit for review.

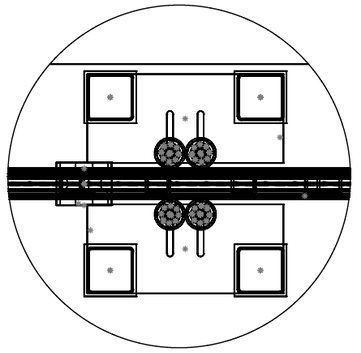


DETAIL A
SCALE 1 : 10

Anuja Raje
Digitally signed by Anuja Raje
Date: 2025.05.16 11:30:36 +05'30'

POST1 AND NYLON BEARING ASM

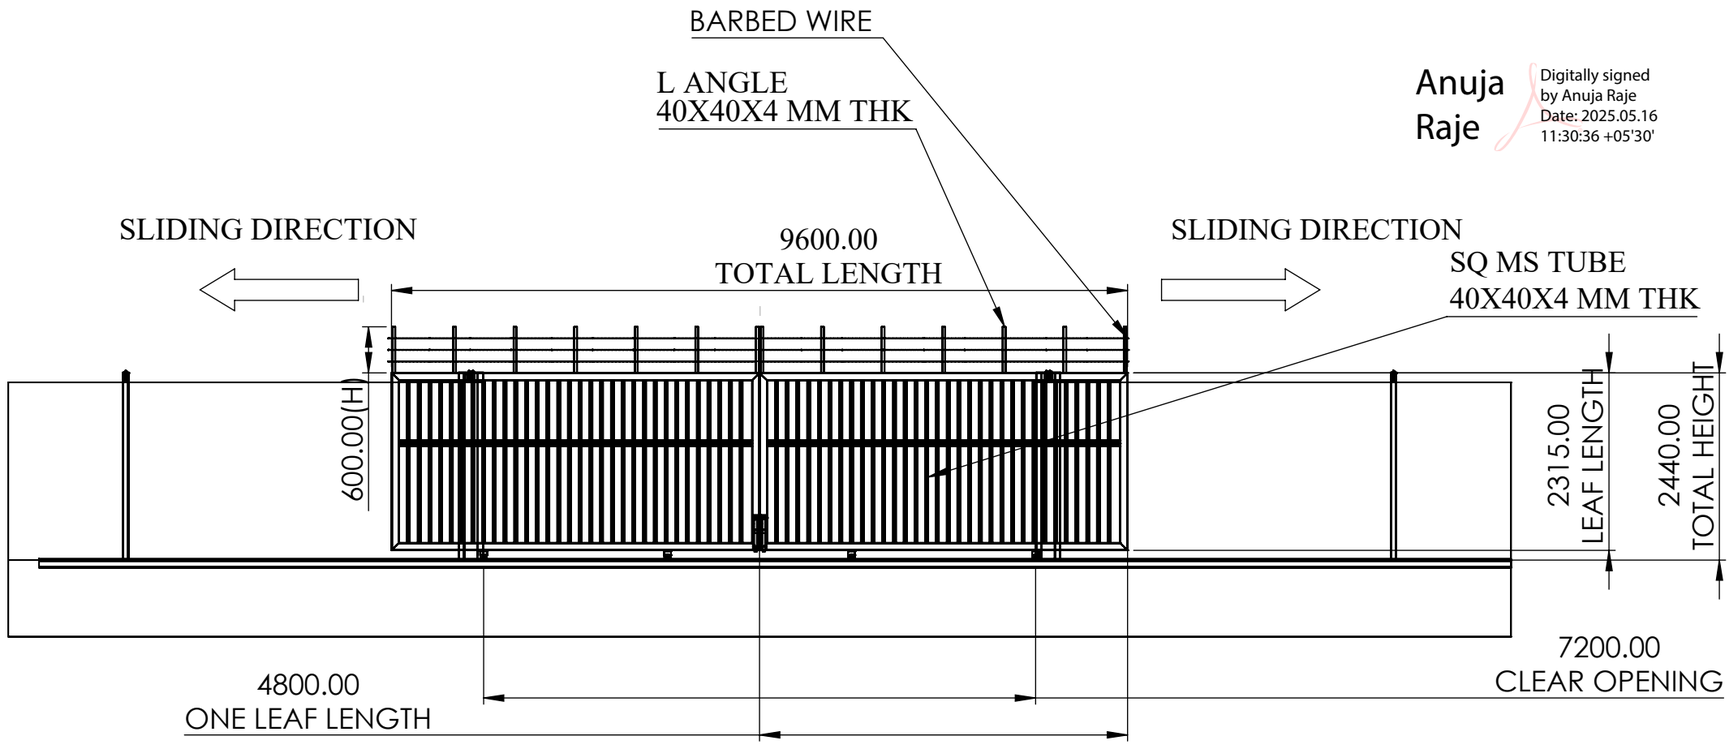

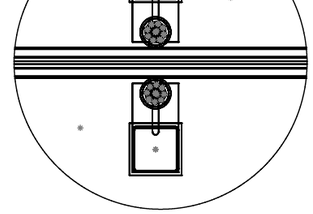

DETAIL B
SCALE 1 : 10

POST 2 AND NYLON BEARING ASM

TCE COMMENTS:

1. Please refer to the latest master layout for the exact site dimensions and space availability.
2. Barbed wire fencing above the sliding gate is under finalization with the Air India team. TCE will confirm shortly.
3. Please specify whether the elevation view is from the inside or outside. It is currently unclear.
4. As the door sizes are as per the requirement, kindly consider the weight and design the sections accordingly. Also, the wheel should be a double wheel, as shown in the architectural layout. Locking arrangement details are missing from the GA drawing.

TITLE - GATE				NIHVA TECHNOLOGIES PVT.LTD.PUNE
DWG NO - NTPL268-PM			QTY - 1	Website - www.nihva.com
	NAME	SIGNATURE	DATE	PROJECT NO - NTPL268-PM- AD
DRAWN	V.B.		02-05-2025	PRODUCT -SLIDING GATE
CHK'D	S.W.		02-05-2025	SITE LOCATION -
APPV'D	V.T.		02-05-2025	
if any queries contact - supportautomation@nihva.com				REVISION -00
ALL DIMENSION ARE IN mm			A3	SCALE - SHEET 1 OF 1