




ELEVATION VIEW
(INSIDE)

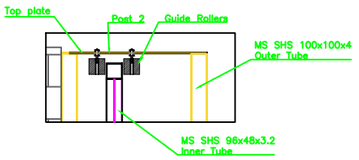



SIDE VIEW




DETAIL B

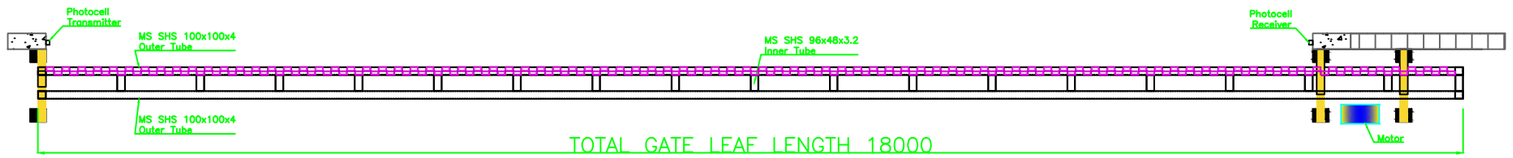

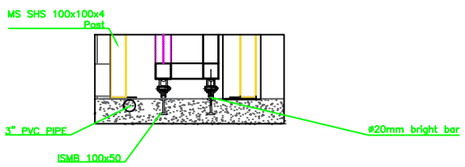
DETAIL A

Technical Specs of Motorized Sliding Gate

1. Opening length - 16000mm
2. Gate Height - 2400mm
3. Parking length required - 18200mm
4. Outer tube size - MS SHS 100x100x4mm
5. Inner tube size - MS RHS 96x48x3mm
6. Bottom Rail - Bright bar Ø20mm
7. Post size - MS SHS 100x100x4mm
8. T`Safety feature - Photocell and flashing light

Note-

1. All dimension are in mm.
2. All civil work is under client scope.
3. 3" PVC pipe in the foundation to be provided by client.
4. 3PH power required near motor.

Rev 01- ( 23-02-2022)

1. Tube sizes changed from 100 x 50 to 96 x 48.
2. Tube mounting changed as per client requirement.
3. Distance between the roller increased for cladding.

This drawing & design is the property of NIHVA TECHNOLOGIES. Not to be sold or copied to any other concern.

| TITLE | | | | |
|---|---|---|---|---|
| MOTORIZED SLIDING GATE | | | | NIHVA TECHNOLOGIES PVT. LTD. PUNE<br>Tel : 020 66304033<br>Email:- info@nihva.com<br>Website:- www.nihva.com |
| | NAME | SIGN | DATE | |
| DRAWN | G.P. | | 23.02.22 | CLIENT - SRF |
| CHECK | A.K. | | 23.02.22 | LOCATION - INDORE |
| APPRD. | V.T. | | 23.02.22 | PRODUCT - MOTORIZED SLIDING GATE |
| If any queries contact : design@nihva.com | | | | NIHVA\21-22\CLT\344 / REV- 1 |
| ALL DIMENSION ARE IN mm | | | | SCALE: NTS / SHEET: 01 OF 01 |