




CRM DOOR 10
QTY - 16 NOS

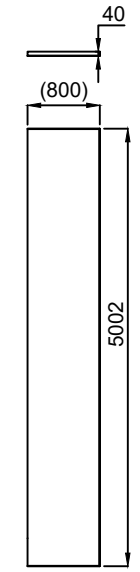


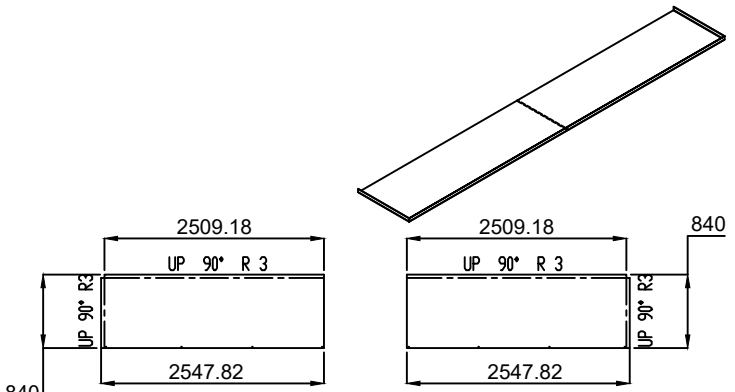


CRM DOOR 10
QTY - 8 NOS
DOWN-SIDE FOLD


CRM DOOR 10
QTY - 8 NOS
UP-SIDE FOLD

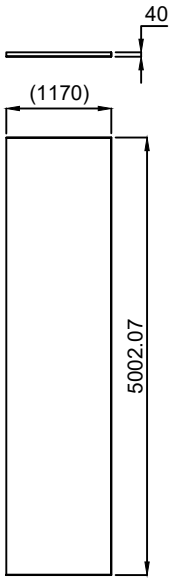

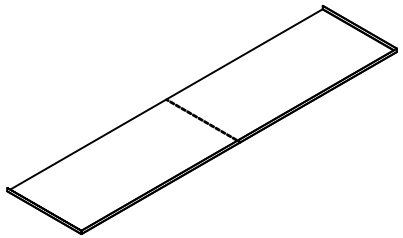

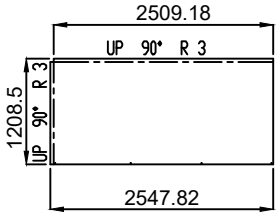

CRM DOOR 10
QTY - 8 NOS
DOWN-SIDE FOLD

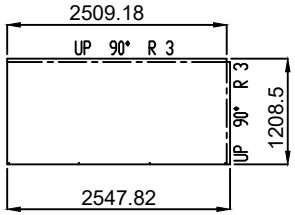

CRM DOOR 10
QTY - 8 NOS
UP-SIDE FOLD

NOTE: DURING BENDING CRITICAL DIMENSION SHOULD BE MANDETORY

PPGI SHEET 0.8 MM

REV.	REVISION DESCRIPTION	Date	Revised By
002	MODIFIED DUE TO RECIEVED COIL SIZE 1210 MM INSTEAD OF 1250 MM	16/05/2022	MAHESH S.
001	MODIFIED SUPPORT'S QTY.	14/05/2022	MAHESH S.
000	RELEASED FOR PRODUCTION	03/05/2022	MAHESH S.

This drawing & design is the property of NIHVA TECHNOLOGIES. Not to be sold or copied to any other concern.

TITLE:- 4 LEAF PPGI CLADDING CRM DOOR 10

NIHVA TECHNOLOGIES PVT. LTD.

NIHVA TECHNOLOGIES PVT. LTD. PUNE
Tel : 020 66304033
Email:- info@nihva.com
Website:- www.nihva.com

	NAME	DATE	SIGN
DRAWN	M.SUTAR	14/05/2022	
CHECK	M.SUTAR	14/05/2022	
APPRD.			

CLIENT - NIHVA TECHNOLOGIES PVT.LTD
LOCATION -
PRODUCT - SLIDING DOOR

If any queries contact : design@nihva.com
DWG NO:-NIHVA/22-23/VDR/0015 REV- 0
ALL DIMENSION ARE IN mm
SCALE: NTS SCALE:-- 1:1 SHEET: 01 OF 01