

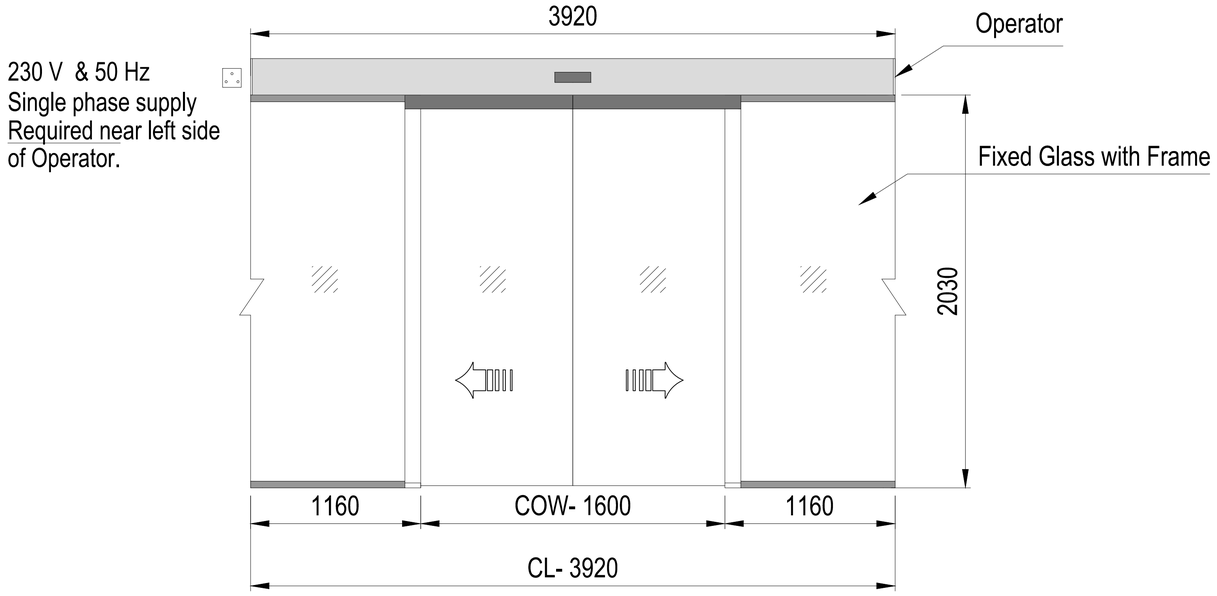


Inside Elevation

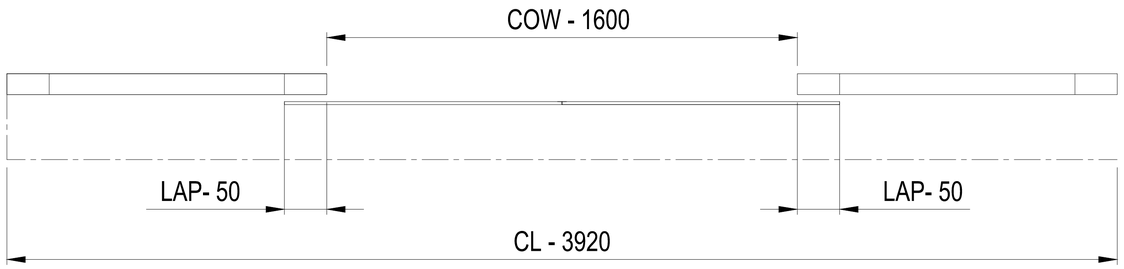


Closed Condition

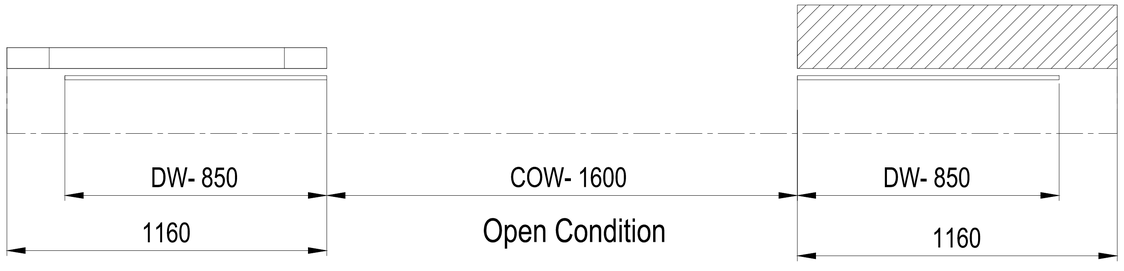

Open Condition

Plan

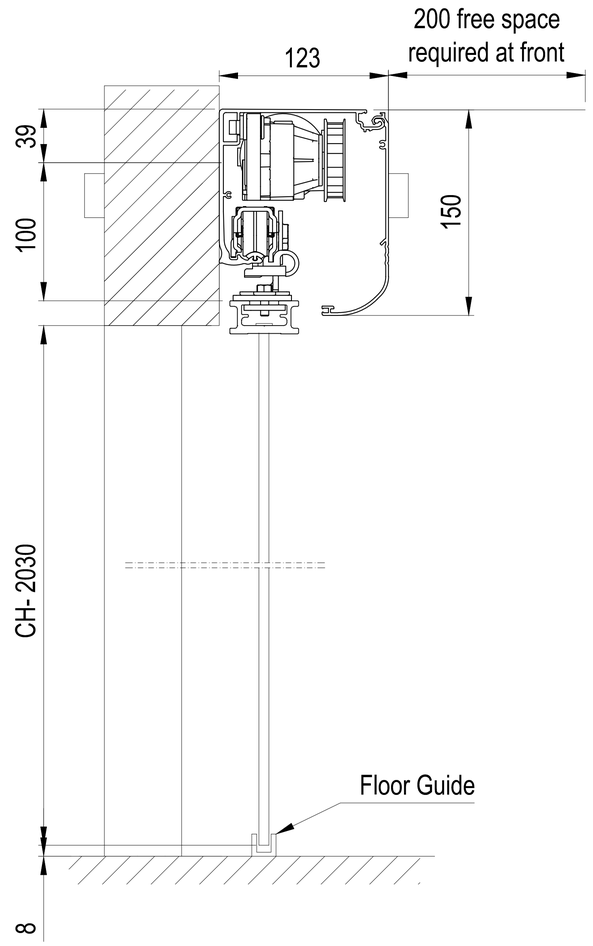

Door Size			
Sr. No.	Clear Width	Clear Height	Quantity
1	1600	2030	1

Glass Type- 10mm Toughened
1. Two fixed glass with frame.
2. Two moving frame without frame.

This drawing & designing is the property of NIHVA TECHNOLOGIES. Not to be sold or copied to any other concern.

TITLE	AUTOMATIC SLIDING GLASS DOOR		NIHVA TECHNOLOGIES PVT. LTD. PUNE Tel : 020 66304033 Email:- info@nihva.com Website:- www.nihva.com
	SIGN	DATE	
DRAWN	OMKAR	29/07/17	CLIENT - VIBGYOR INTERIORS & DESIGNERS
CHECK	S.S.	29/07/17	PROJECT - INDO SCHOTTLE
REV.	00		SITE - URWADE,MULASHI
APPROVAL			DWG. NO. : NIHVA/17-18/0139
If any queries contact : projects@nihva.com			SCALE: NTS | WT: | SHEET: 01 OF 01
ALL DIMENSION ARE IN mm			