


DRAWING

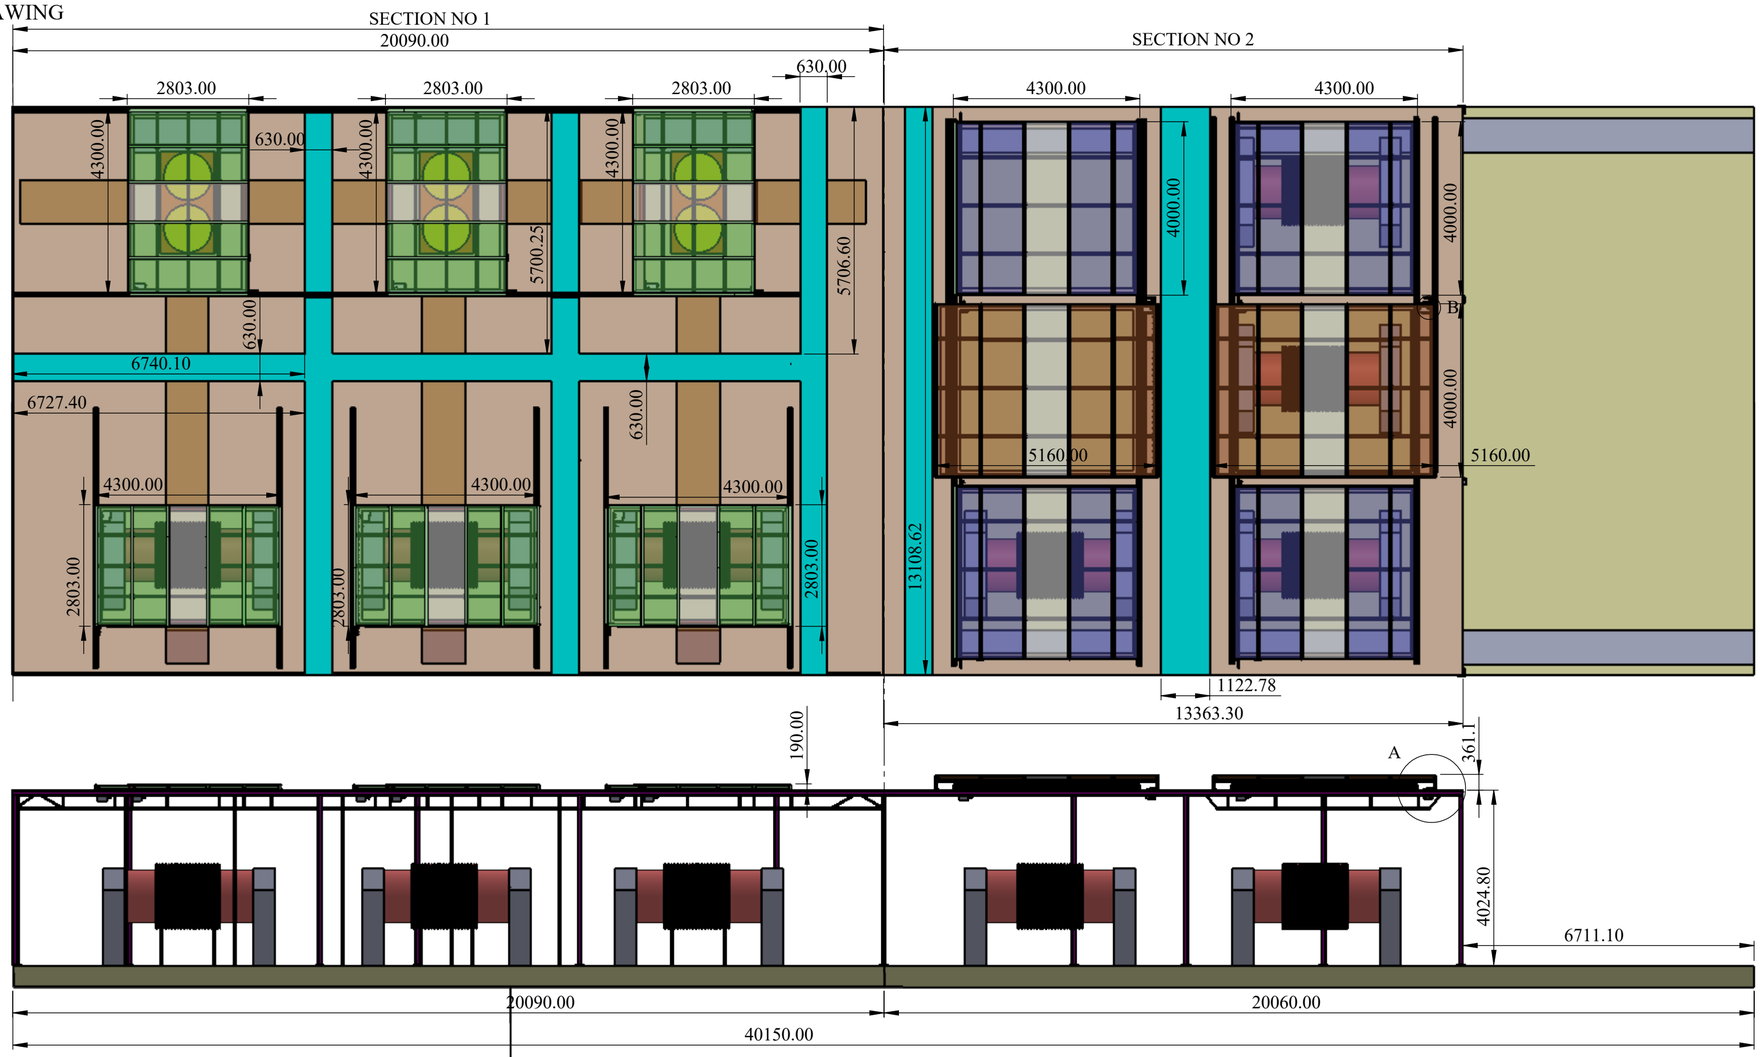

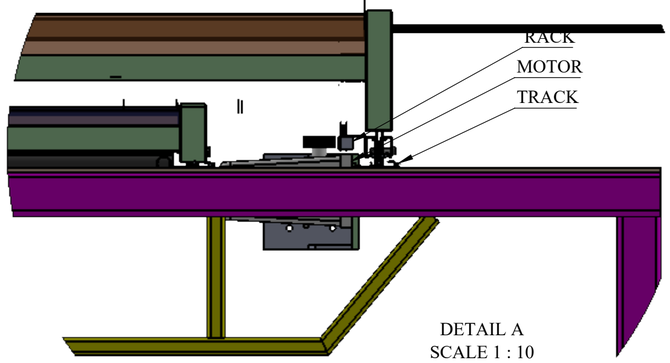

DETAIL A
SCALE 1 : 10
MOTOR ARRANGMENT

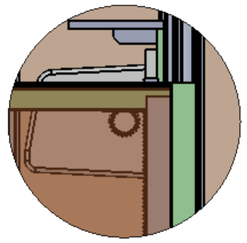

DETAIL B
SCALE 1 : 10

REV DESCRIPTION	DATE	REV NO
	08-08-2025	REV 00
1.		

NOTE :

SPECIAL INSTRUCTION'S :

	NAME	SIGNATURE	DATE
DRAWN	V.W.		28-08-2025
CHK'D	S.P.		04-09-2025
APPV'D	V.T.		05-09-2025

TITLE - ROOF AUTOMATION

DWG NO - NTPL-244-PM-001-00-00-00

NIHVA Technologies Pvt. Ltd.

NIHVA TECHNOLOGIES PVT.LTD.PUNE
Website - www.nihva.com

PRODUCT - RETRACTABLE ROOF

PROJECT NO - NTPL-244-PM | REVISION - 00

SITE LOCATION - GUJARAT | WEIGHT -

MATRIAL - | QTY - 1

If any queries contact - Design@nihva.com


PROJECTION METHOD:

SCALE :

ALL DIMENSION ARE IN mm | A2

DRAWING

REV DESCRIPTION	DATE	REV NO
	28-08-2025	REV 00
1.		

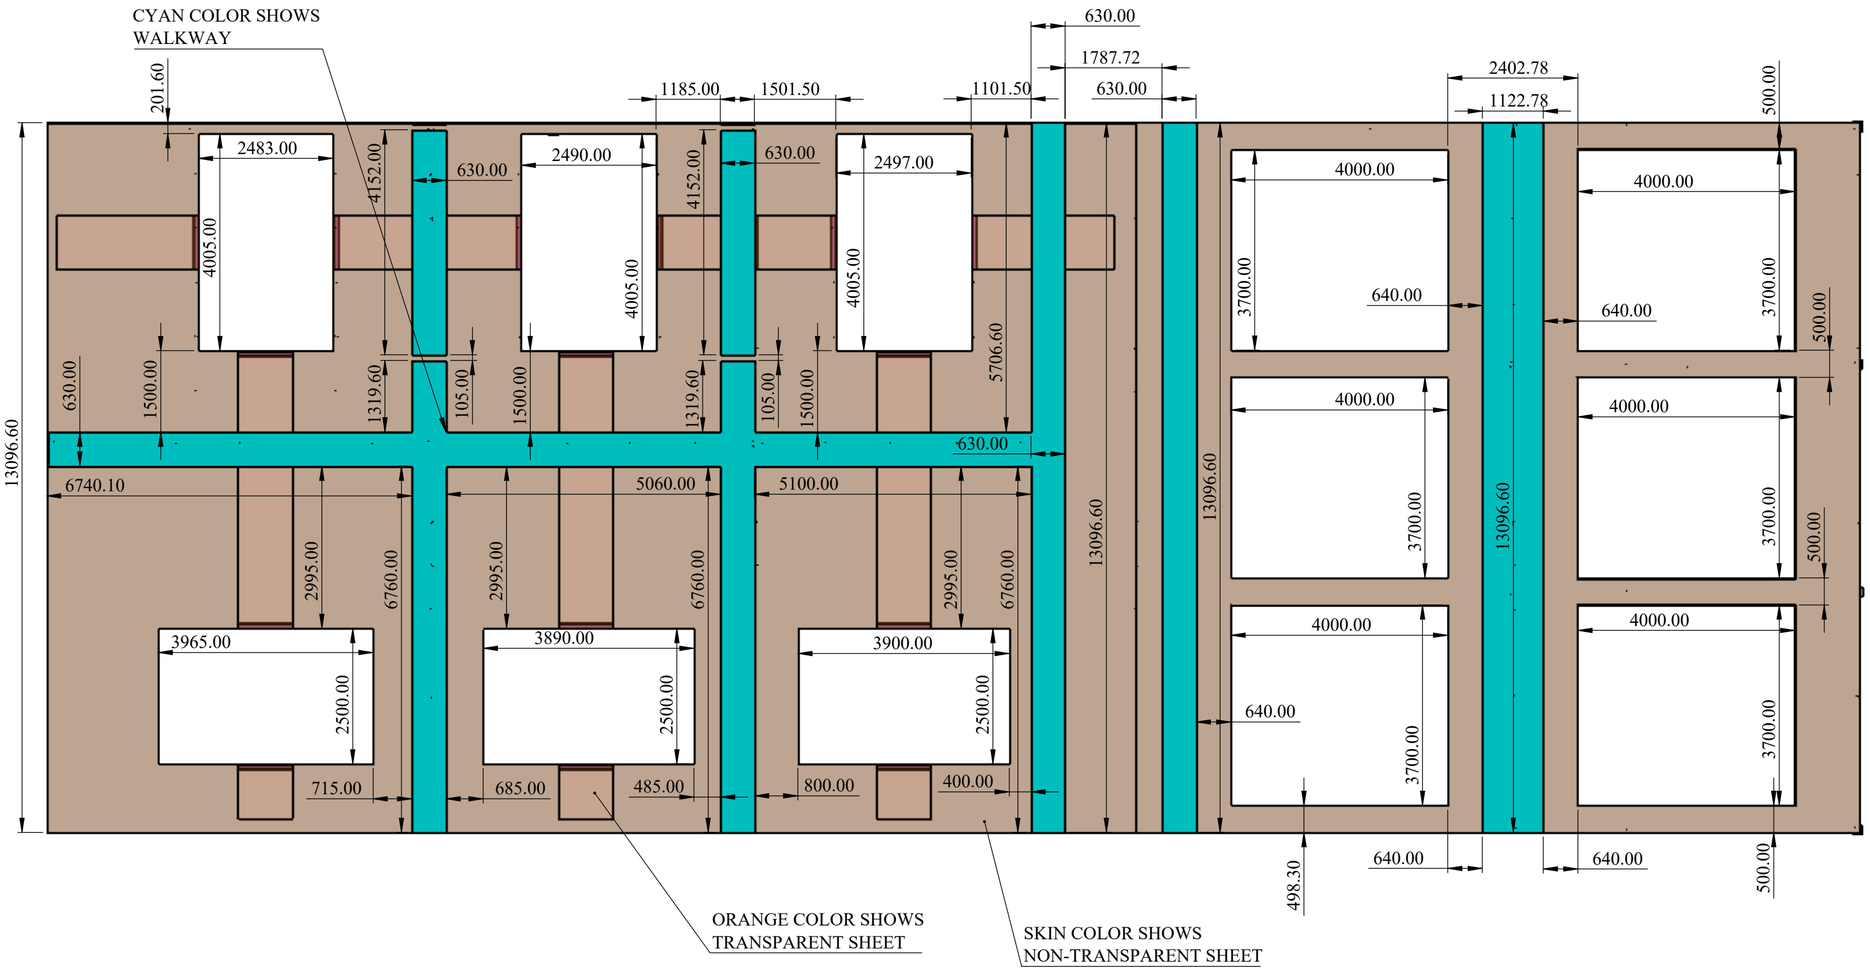

NOTE :

SPECIAL INSTRUCTION'S :

TITLE - ROOF AUTOMATION

DWG NO - NTPL-244-PM-001-00-00-00

NIHVA Technologies Pvt. Ltd.

NIHVA TECHNOLOGIES PVT.LTD.PUNE
Website - www.nihva.com

	NAME	SIGNATURE	DATE
DRAWN	V.W.		28-08-2025
CHK'D	S.P.		04-09-2025
APPV'D	V.T.		05-09-2025

PRODUCT - RETRACTABLE ROOF

PROJECT NO - NTPL-244-PM | REVISION - 00

SITE LOCATION - GUJARAT | WEIGHT -

MATRIAL - | QTY - 1


If any queries contact - Design@nihva.com

ALL DIMENSION ARE IN mm | A2


PROJECTION METHOD:


SCALE :

DRAWING

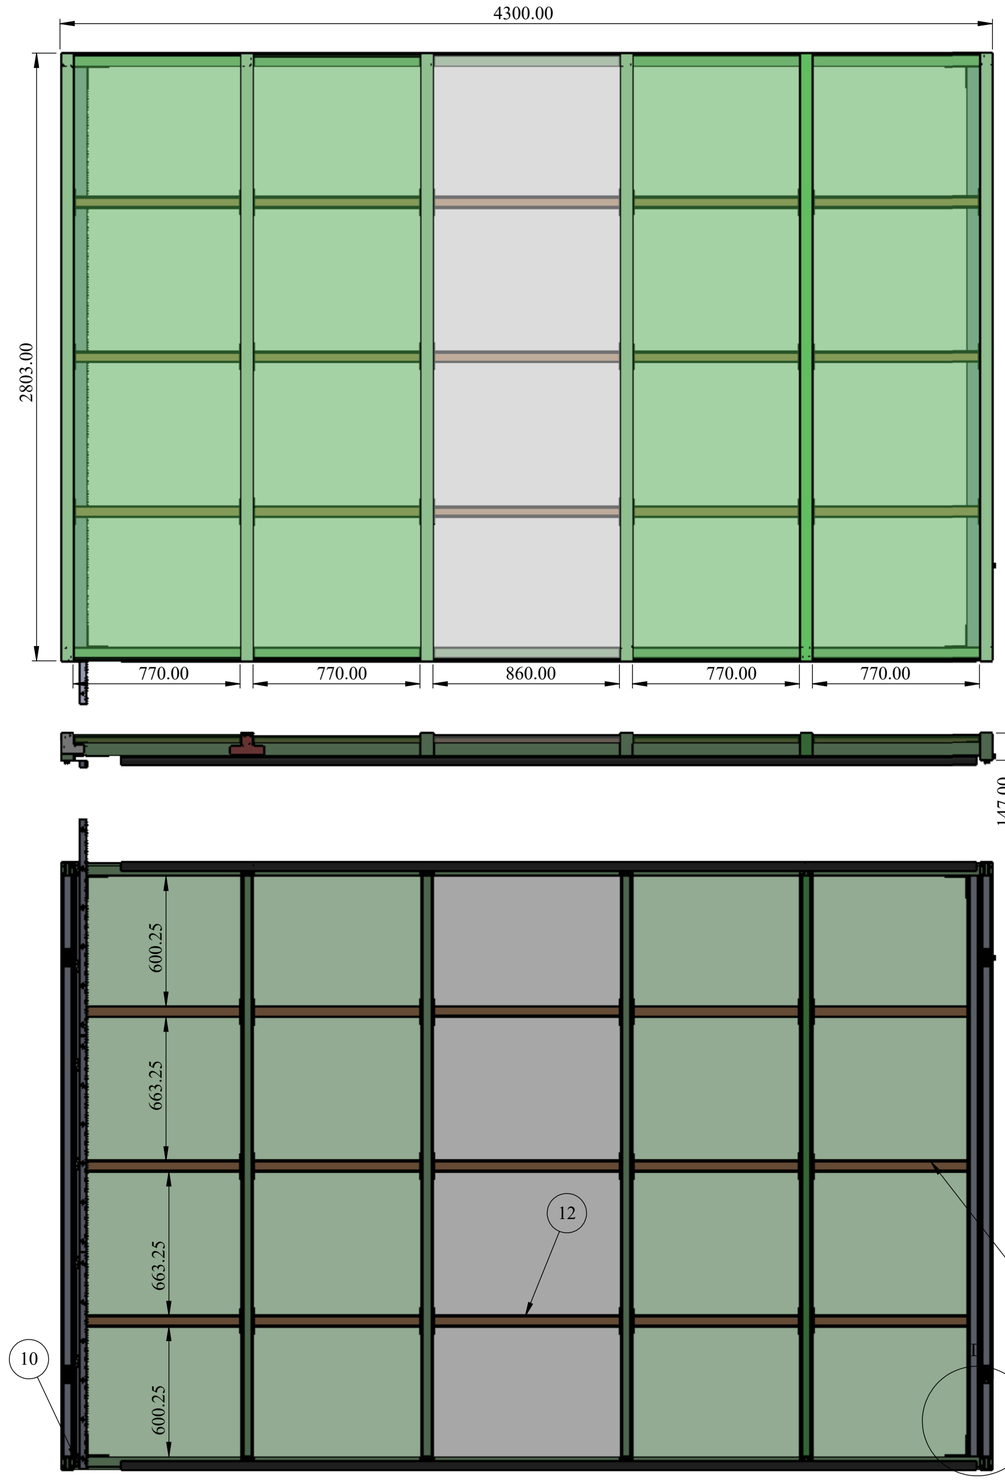

ITEM NO.	PART NUMBER	DESCRIPTION	QTY.
1	.rev0202paneel modify-03.		1
2	.Rev_02_SS WHEEL.	SS WHEEL ∅65X18	4
3	NP-PROF01	MS50X50X4T	2
4	NP-PROF01	MS50X50X4T	2
5	.Rev_02_panel modifiy-02 intermediate support assembly.		12
6	T PLATE	156X91X3 MM THK	1
7	L PLATE	91X106X3 MM THK	1
8	.Rev_02_AL INSIDE CORNER WELD PLATE.	196X40X3 MM THK	4
9	C-MSBL12-35.SLDASM	SHOULDER BOLT	1
10	RACK SUPPORT PLATE.		7
11	.Rev_02_RACK..		3
12	.rev0202panel modifiy-03 intermediate support assembly.		3

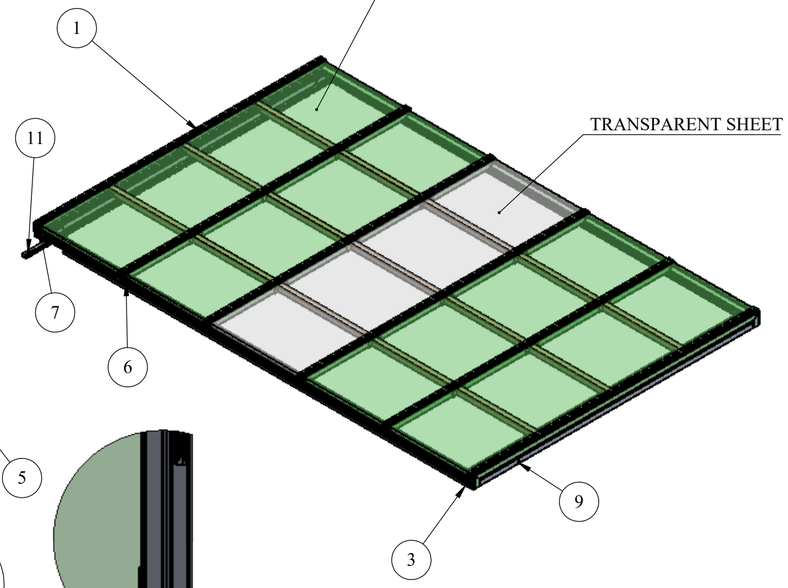

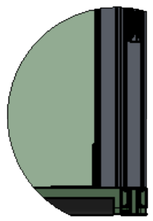

DETAIL D
SCALE 1 : 10

REV DESCRIPTION	DATE	REV NO
	28-08-2025	REV 00
1.		

NOTE :

PANEL ASM - SECTION 1
QTY - 06 No'S.


SPECIAL INSTRUCTION'S :


TITLE - ROOF AUTOMATION				NIHVA Technologies Pvt. Ltd.	NIHVA TECHNOLOGIES PVT.LTD.PUNE Website - www.nihva.com
DWG NO - NTPL-244-PM-001-00-00-00					
	NAME	SIGNATURE	DATE	PRODUCT - RETRACTABLE ROOF	
DRAWN	V.W.		28-08-2025	PROJECT NO - NTPL-244-PM	REVISION - 00
CHK'D	S.P.		04-09-2025	SITE LOCATION - GUJARAT	WEIGHT -
APPV'D	V.T.		05-09-2025	MATRIAL -	QTY - 1
If any queries contact - Design@nihva.com				PROJECTION METHOD:	SCALE :
ALL DIMENSION ARE IN mm			A2		SHEET 3 OF 11

DRAWING


ITEM NO.	PART NUMBER	DESCRIPTION	QTY.
1	.rev0202paneel modify-03.		06


REV DESCRIPTION	DATE	REV NO
	08-08-2025	REV 00
1.		

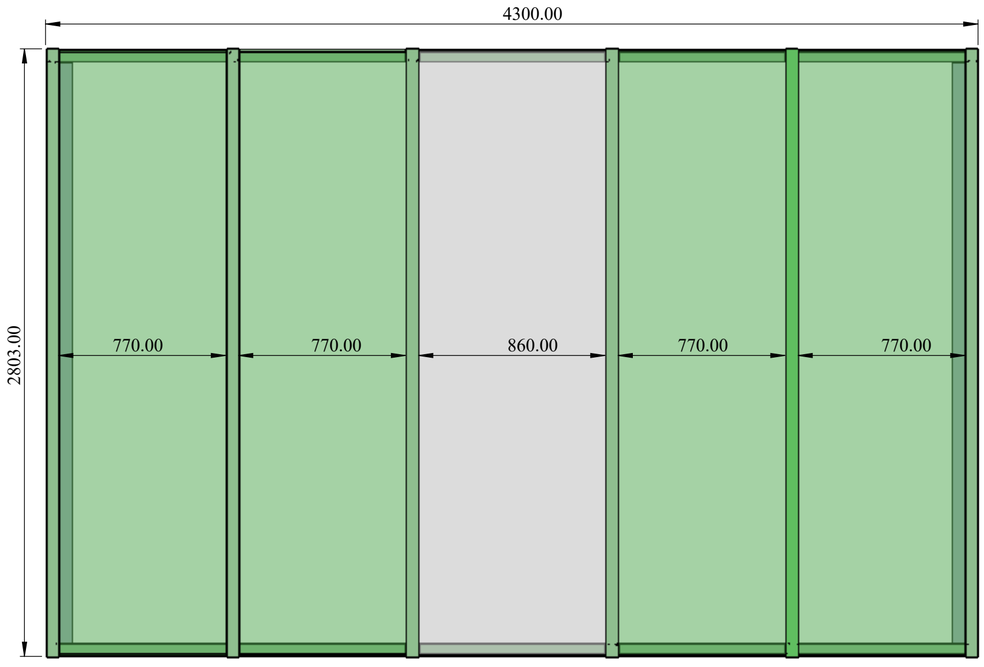

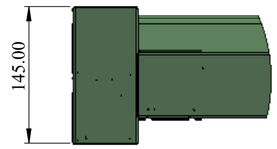

DETAIL C
SCALE 1 : 4

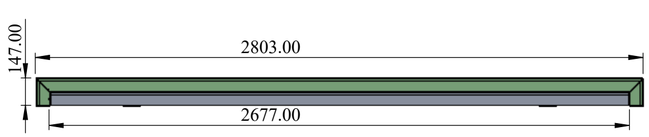

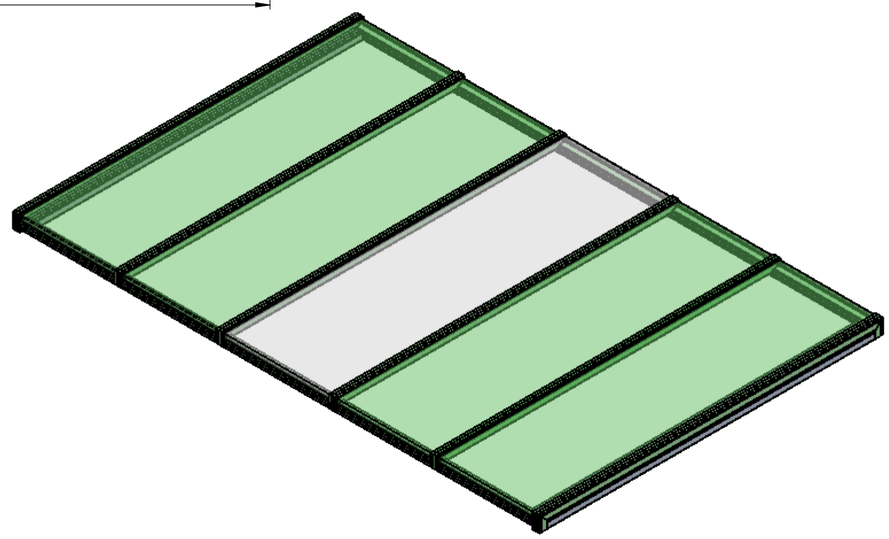

NOTE :

SECTION NO 1 - PANEL
QTY - 06 No's


SPECIAL INSTRUCTION'S :


TITLE - ROOF AUTOMATION			
DWG NO - NTPL-244-PM-001-00-00-00			
NIHVA Technologies Pvt. Ltd.			NIHVA TECHNOLOGIES PVT.LTD.PUNE Website - www.nihva.com
	NAME	SIGNATURE	DATE
DRAWN	V.W.		28-08-2025
CHK'D	S.P.		04-08-2025
APPV'D	V.T.		05-08-2025
PRODUCT - RETRACTABLE ROOF			
PROJECT NO - NTPL-244-PM			REVISION - 00
SITE LOCATION - GUJARAT			WEIGHT -
MATRIAL -			QTY - 1
If any queries contact - Design@nihva.com			SCALE :
ALL DIMENSION ARE IN mm	A2		PROJECTION METHOD:

DRAWING

REV DESCRIPTION	DATE	REV NO
	28-08-2025	REV 00
1.		

ITEM NO.	PART NUMBER	DESCRIPTION	QTY.
1	AL PROFILE	REC - 50X50X2 THK	1
2	.Rev_02_NP-PLT01.	AL - 120X50X3T	2

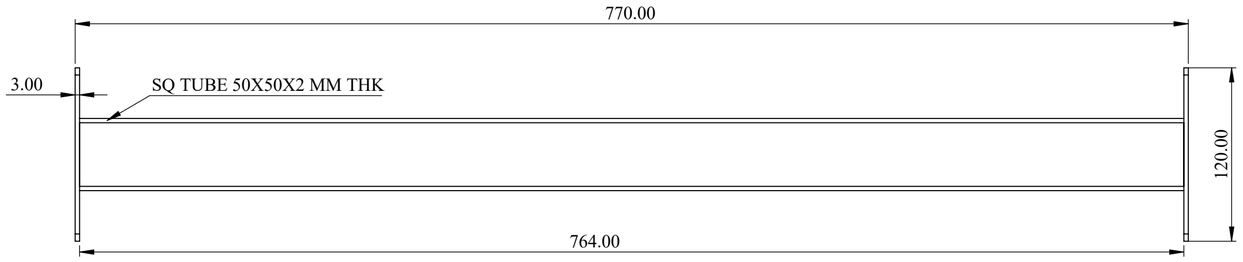

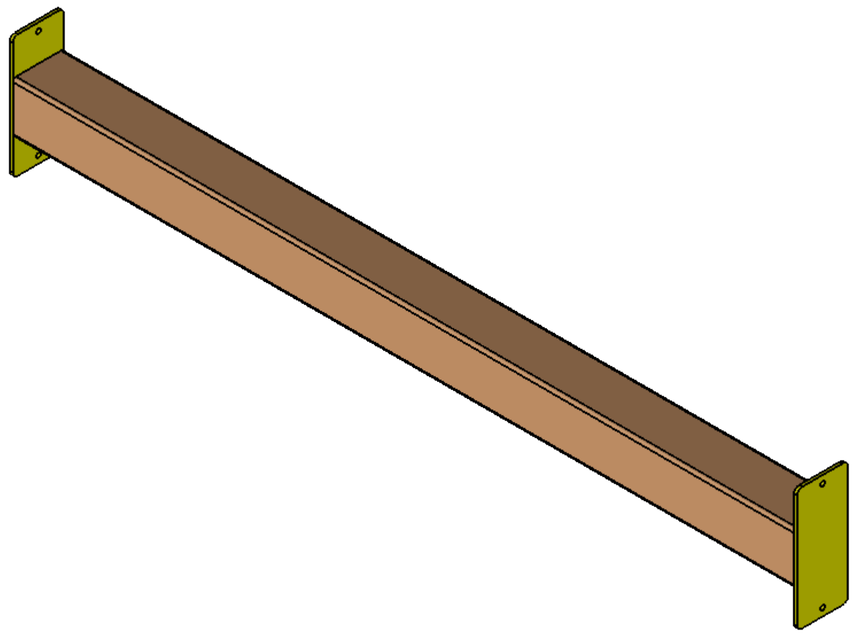

NOTE :

NAME : INTERMEDIATE SUPPORT TUBE
SIZE : 50X50X2 MM THK - 770 MM L
QTY : ONE PANEL REQ QTY - 15 NOS
TOTAL QTY REQ - 90 NOS

SPECIAL INSTRUCTION'S :

TITLE - ROOF AUTOMATION

DWG NO - NTPL-244-PM-001-00-00-00

NIHVA Technologies Pvt. Ltd.


NIHVA TECHNOLOGIES PVT.LTD.PUNE
Website - www.nihva.com


	NAME	SIGNATURE	DATE
DRAWN	V.W.		28-08-2025
CHK'D	S.P.		04-09-2025
APPV'D	V.T.		05-09-2025

PRODUCT - RETRACTABLE ROOF
PROJECT NO - NTPL-244-PM | REVISION - 00
SITE LOCATION - GUJARAT | WEIGHT -
MATRIAL - | QTY - 1
If any queries contact - Design@nihva.com | PROJECTION METHOD: | SCALE :
ALL DIMENSION ARE IN mm | A2 | SHEET 5 OF 11

DRAWING

ITEM NO.	PART NUMBER	DESCRIPTION	QTY.
1	AL PROFILE	REC - 50X50X2T	1
2	.rev0202NP-PLT01.	AL - 120X50X3T	2

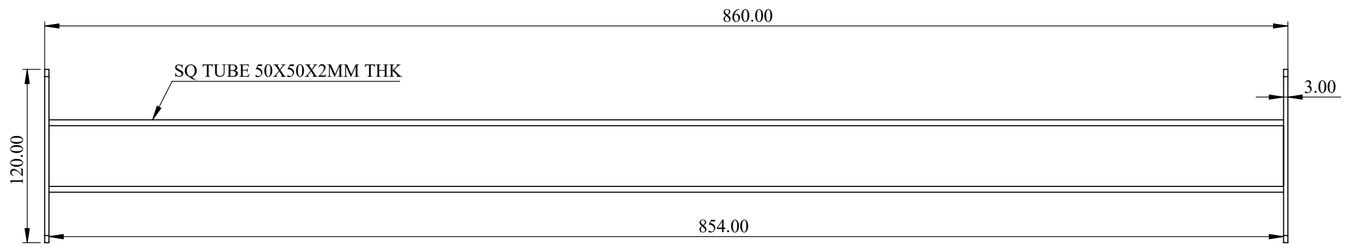

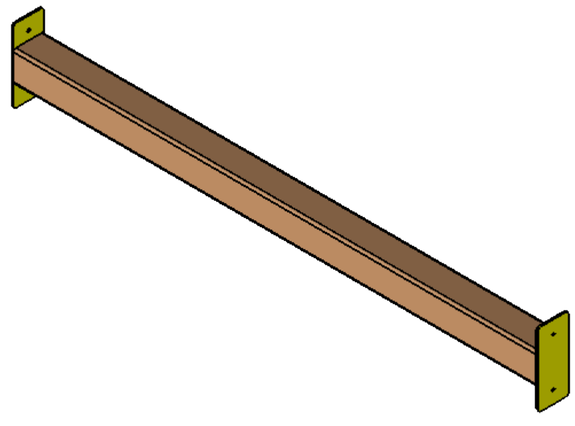

REV DESCRIPTION	DATE	REV NO
	28-08-2025	REV 00
1.		

NOTE :

NAME : INTERMEDIATE SUPPORT TUBE
SIZE : 50X50X2 MM THK - 860 MM L
QTY : ONE PANEL REQ QTY - 3 NOS
TOTAL QTY REQ - 18 NOS

SPECIAL INSTRUCTION'S :

TITLE - ROOF AUTOMATION

DWG NO - NTPL-244-PM-001-00-00-00

NIHVA Technologies Pvt. Ltd.

NIHVA TECHNOLOGIES PVT.LTD.PUNE
Website - www.nihva.com


	NAME	SIGNATURE	DATE
DRAWN	V.W.		28-08-2025
CHK'D	S.P.		04-09-2025
APPV'D	V.T.		05-09-2025


PRODUCT - RETRACTABLE ROOF
PROJECT NO - NTPL-244-PM | REVISION - 00
SITE LOCATION - GUJARAT | WEIGHT -
MATRIAL - | QTY - 1
If any queries contact - Design@nihva.com | PROJECTION METHOD: | SCALE :
ALL DIMENSION ARE IN mm | A2 | SHEET 6 OF 11


DRAWING

REV DESCRIPTION	DATE	REV NO
	28-08-2025	REV 00
1.		

ITEM NO.	PART NUMBER	DESCRIPTION	QTY.
1	NYLON WHEEL	NYLON WHEEL ∅65X18	04

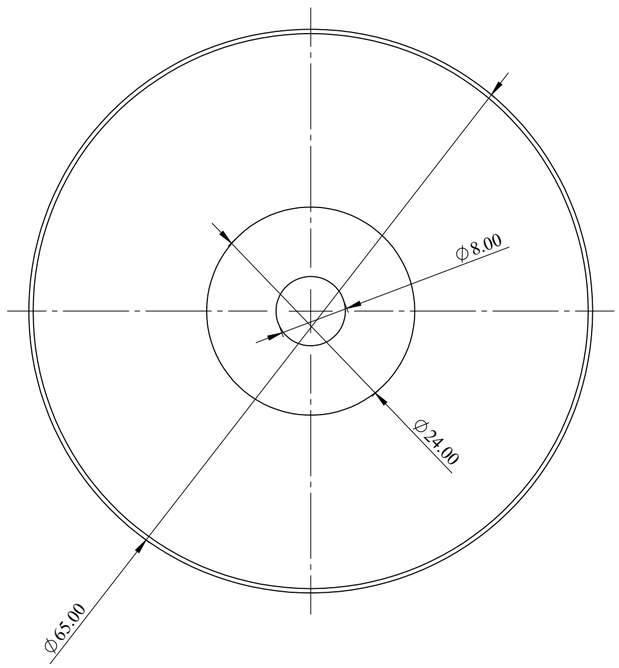

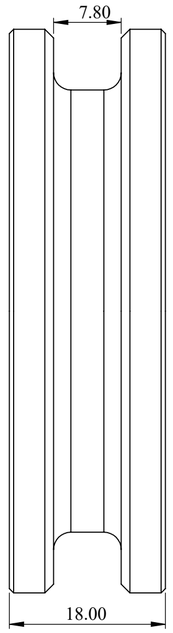

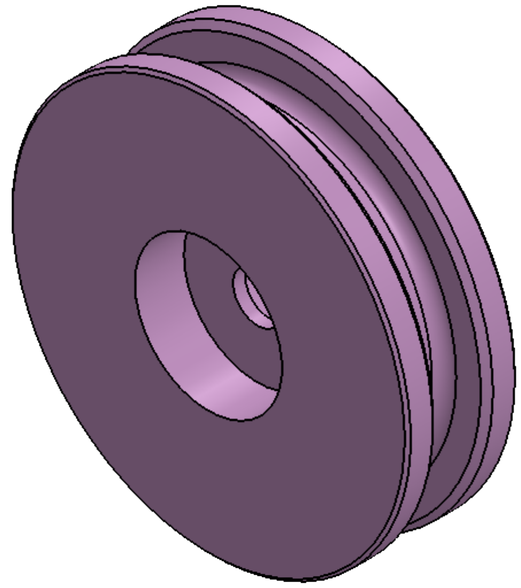

NOTE :

NYLON WHEEL - DIA 65X W 18 MM
ONE PANEL REQ QTY - 04 No'S.
TOTAL REQ QTY - 24 No'S

SPECIAL INSTRUCTION'S :

TITLE - ROOF AUTOMATION

DWG NO - NTPL-244-PM-001-00-00-00

NIHVA Technologies Pvt. Ltd.

NIHVA TECHNOLOGIES PVT.LTD.PUNE
Website - www.nihva.com


	NAME	SIGNATURE	DATE
DRAWN	V.W.		28-08-2025
CHK'D	S.P.		04-09-2025
APPV'D	V.T.		05-09-2025


PRODUCT - RETRACTABLE ROOF
PROJECT NO - NTPL-244-PM | REVISION - 00
SITE LOCATION - GUJARAT | WEIGHT -
MATRIAL - | QTY - 1
If any queries contact - Design@nihva.com | PROJECTION METHOD: | SCALE :
ALL DIMENSION ARE IN mm | A2 | SHEET 7 OF 11

DRAWING

REV DESCRIPTION	DATE	REV NO
	28-08-2025	REV 00
1.		

ITEM NO.	PART NUMBER	DESCRIPTION	QTY.
1	L PLATE	91X106X3 MM THK	04

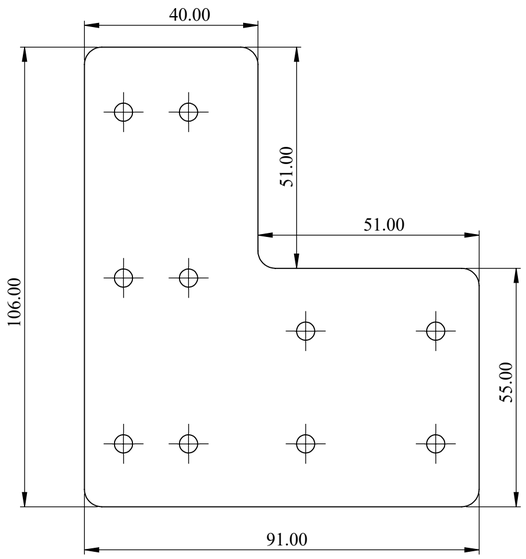

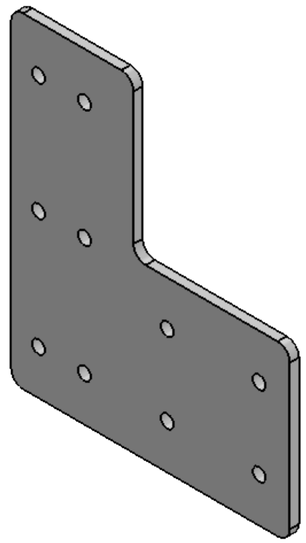

NOTE :

NAME - L PLATE
SIZE - 106X91X3 MM THK
THK - 3 MM
ONE PANEL REQ QTY - 4 No'S
TOTAL REQ QTY - 24 No'S
MTL - SS.

SPECIAL INSTRUCTION'S :

TITLE - ROOF AUTOMATION

DWG NO - NTPL-244-PM-001-00-00-00

NIHVA TECHNOLOGIES PVT.LTD.PUNE
Website - www.nihva.com


	NAME	SIGNATURE	DATE
DRAWN	V.W.		28-08-2025
CHK'D	S.P.		04-09-2025
APPV'D	V.T.		05-09-2025


PRODUCT - RETRACTABLE ROOF
PROJECT NO - NTPL-244-PM
REVISION - 00
SITE LOCATION - GUJARAT
WEIGHT -
MATRIAL -
QTY - 1
SCALE :
PROJECTION METHOD:
If any queries contact - Design@nihva.com
ALL DIMENSION ARE IN mm
A2

DRAWING

REV DESCRIPTION	DATE	REV NO
	28-08-2025	REV 00
1.		

ITEM NO.	PART NUMBER	DESCRIPTION	QTY.
1	L ANGLE PLATE	17X52X3 MM THK	08

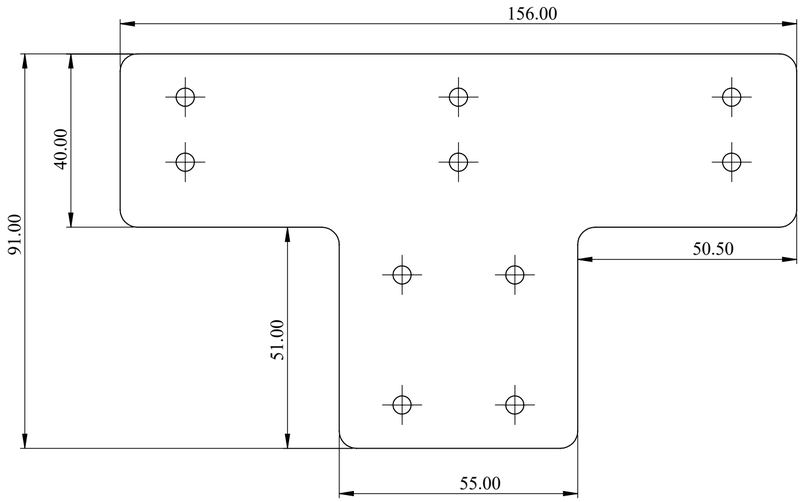

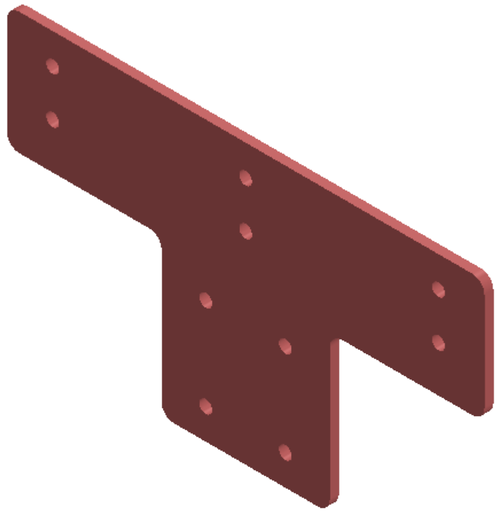

NOTE :

NAME - T PLATE
SIZE - 156X91X3 MM THK
THK - 3 MM
MTL - SS
ONE PANEL REQ QTY - 08 No'S
TOTAL REQ QTY - 48 No'S.

SPECIAL INSTRUCTION'S :

TITLE - ROOF AUTOMATION

DWG NO - NTPL-244-PM-001-00-00-00

NIHVA Technologies Pvt. Ltd.

NIHVA TECHNOLOGIES PVT.LTD.PUNE
Website - www.nihva.com

	NAME	SIGNATURE	DATE		
DRAWN	V.W.		28-08-2025	PROJECT NO - NTPL-244-PM	REVISION - 00
CHK'D	S.P.		04-09-2025	SITE LOCATION - GUJARAT	WEIGHT -
APPV'D	V.T.		05-09-2025	MATRIAL -	QTY - 1

If any queries contact - Design@nihva.com

ALL DIMENSION ARE IN mm | A2


PROJECTION METHOD:


SCALE :


DRAWING


ITEM NO.	PART NUMBER	DESCRIPTION	QTY.
1	RACK SUPPORT PLATE.		08

REV DESCRIPTION	DATE	REV NO
	28-08-2025	REV 00
1.		

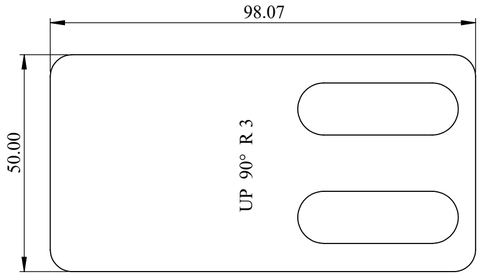

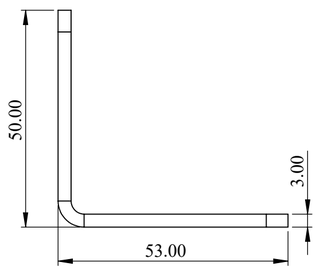

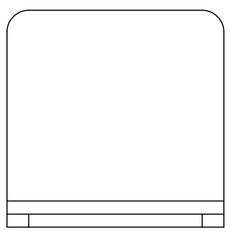

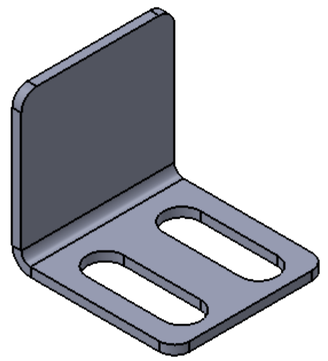

NOTE :

NAME - RACK SUPPORT PLATE
SIZE - 98.07X50X3 MM THK
THK - 3 MM
MTL - MS
ONE PANEL PANEL REQ QTY -8 No'S
TOTAL REQ QTY - 48 No'S.

SPECIAL INSTRUCTION'S :

TITLE - ROOF AUTOMATION

DWG NO - NTPL-244-PM-001-00-00-00

NIHVA Technologies Pvt. Ltd.

NIHVA TECHNOLOGIES PVT.LTD.PUNE
Website - www.nihva.com


	NAME	SIGNATURE	DATE
DRAWN	V.W.		28-08-2025
CHK'D	S.P.		04-09-2025
APPV'D	V.T.		05-09-2025


PRODUCT - RETRACTABLE ROOF
PROJECT NO - NTPL-244-PM
REVISION - 00
SITE LOCATION - GUJARAT
WEIGHT -
MATRIAL -
QTY - 1
If any queries contact - Design@nihva.com
ALL DIMENSION ARE IN mm
A2
PROJECTION METHOD:
SCALE :
SHEET 10 OF 11

DRAWING

REV DESCRIPTION	DATE	REV NO
	28-08-2025	REV 00
1.		

ITEM NO.	PART NUMBER	DESCRIPTION	QTY.
1	.Rev_02_RACK..		3

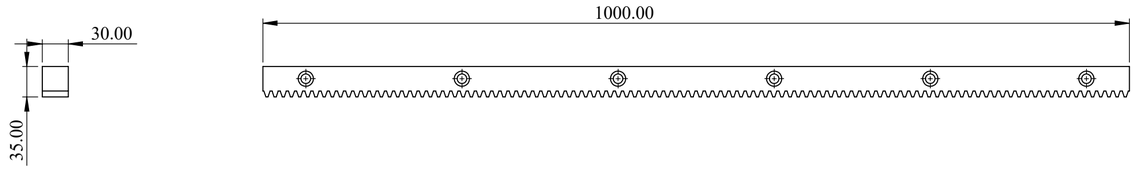

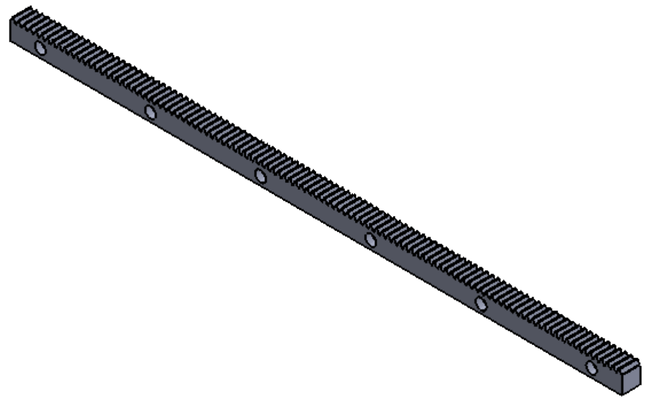

NOTE :

NAME - RACK
ONE PANEL REQ QTY - 3 No'S
TOTAL REQ QTY - 18 No'S.

SPECIAL INSTRUCTION'S :

TITLE - ROOF AUTOMATION

DWG NO - NTPL-244-PM-001-00-00-00

NIHVA Technologies Pvt. Ltd.

NIHVA TECHNOLOGIES PVT.LTD.PUNE
Website - www.nihva.com

	NAME	SIGNATURE	DATE		
DRAWN	V.W.		28-08-2025	PRODUCT - RETRACTABLE ROOF	
CHK'D	S.P.		04-09-2025	PROJECT NO - NTPL-244-PM	REVISION - 00
APPV'D	V.T.		05-09-2025	SITE LOCATION - GUJARAT	WEIGHT -
				MATRIAL -	QTY - 1
If any queries contact - Design@nihva.com				PROJECTION METHOD:	SCALE :
ALL DIMENSION ARE IN mm			A2		SHEET 11 OF 11