




SIDE VIEW

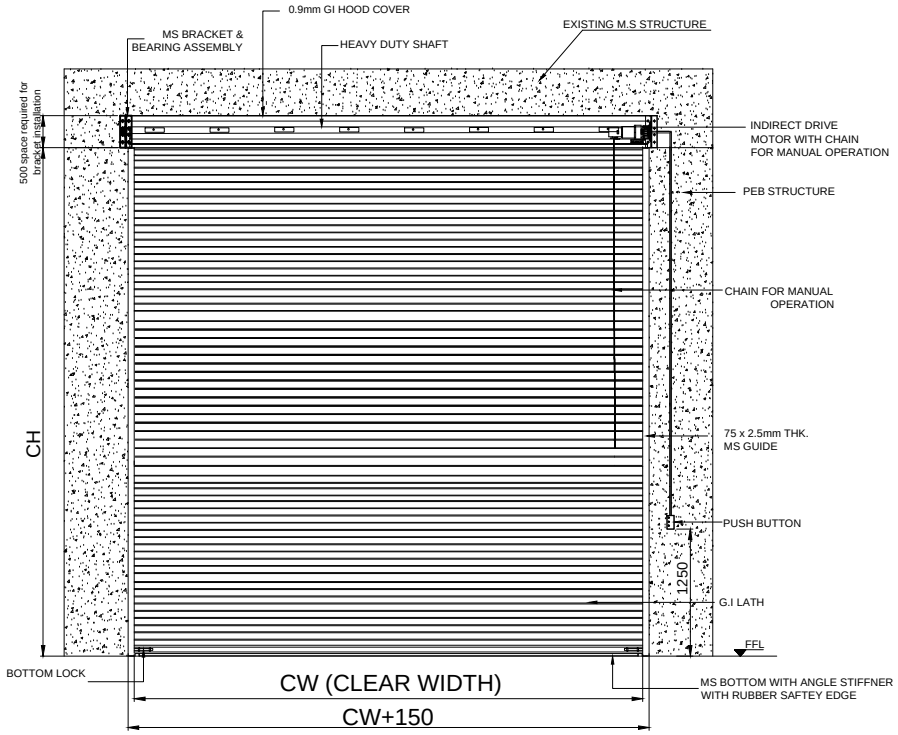


ELEVATION

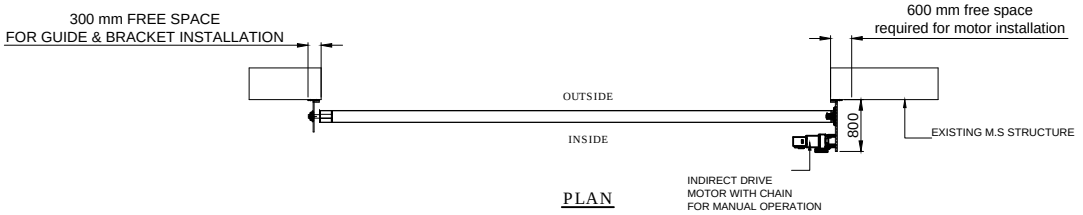

PLAN

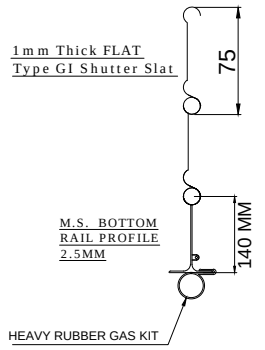

M.S. BOTTOM RAIL PROFILE 2.5MM

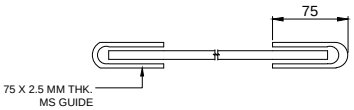

NOTE-
1. ALL CIVIL WORK WILL BE CLIENT'S SCOPE.

TOLERANCE - ±10mm

CLEAR WIDTH	CLEAR HEIGHT	QTY.
4000mm	5000mm	02 NOS
2500mm	3000mm	17 NOS

S.NO	RAL CODE	COLOR
01	RAL 9002	WHITE GRAY

This drawing & design is the property of NIHVA TECHNOLOGIES. Not to be sold or copied to any other concern.

TITLE
MOTORISED ROLLING SHUTTER

	NAME	SIGN	DATE
DRAWN	P.A		14.12.2019
CHECK	G.J		14.12.2019
APPRD.			

If any queries contact : design@nihva.com

ALL DIMENSION ARE IN mm

NIHVA
NIHVA TECHNOLOGIES PVT. LTD.
Website:- www.nihva.com
NIHVA TECHNOLOGIES PVT. LTD. PUNE
Tel : 020 66304033
Email:- info@nihva.com

CLIENT - SYNERGY PROPERTY DEVELOPMENT SERVICES PVT LTD

PROJECT -

SITE LOCATION - CHAKAN

DWG. NO. : NIHVA/19-20/0171 | REV- R00

SCALE: NTS | WT: | SHEET: 01 OF 01