



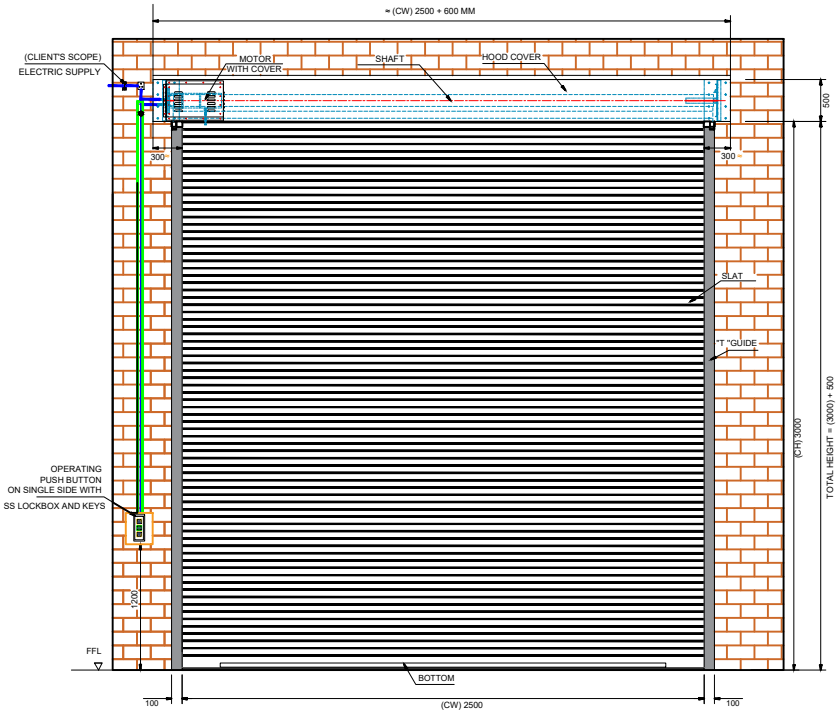

INSIDE ELEVATION

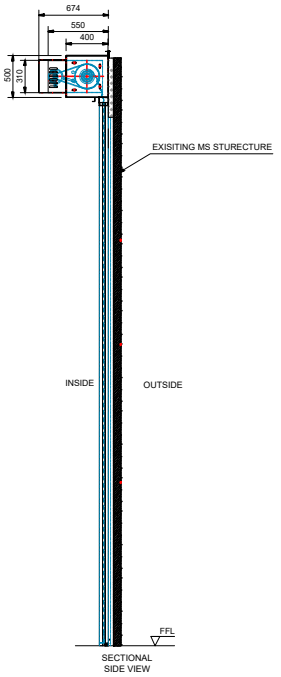

TECHNICAL SPECIFICATION:-

SR.	SPECIFICATION	DETAILS
1.	Description & Drive	Motorised Rolling Shutter (direct Drive)
2.	Location Area	Inside
3.	Mounting Surface	WALL MOUNTING
4.	Slat	AS PER NIHVA STD.
5.	Bottom Profile	MS Plate 100 x 2.5 mm thick with Angle Stiffner with rubber seal
6.	Guide Profile	M.S." T " Shape profile 100 x 3 mm Thk.
7.	Hood Cover & Motor Cover	Made of GI Sheet Thickness 0.9 mm
8.	Surface finish	PRIMER + 1 LAYER OF QD PAINT
9	Accessories	Push Button Single side

SHUTTER SIZES :-

SR.	CLEAR WIDTH	CLEAR HEIGHT	QTY.
01	2500 mm	3000 mm	1

Note :-

1. All Dimension are in mm
2. This drawing is only for understanding purpose

This drawing & designing is the property of NIHVA TECHNOLOGIES. Not to be sold or copied to any other concern

TITLE :- MOTORISED ROLLING SHUTTER

NIHVA TECHNOLOGIES PVT. LTD. PUNE
Tel : 020 66304033
Email:- info@nihva.com
Website:- www.nihva.com

	NAME	DATE	
DRAWN	B.S.	24/01/2025	CLIENT - SMP INFRASTRUCTURE PVT. LTD.
CHECK	V.M.	24/01/2025	PROJECT - ROLLING SHUTTER
APPROVAL	V.T.	24/01/2025	FORMAT NO - NIHVA-DD-F-03
			DWG. NO. : NIHVA/24-25/SMP/250124 — REV-00
			SCALE: NTS — WT: — SHEET: 01 OF 01
ALL DIMENSION ARE IN mm			If any queries contact : design@nihva.com