

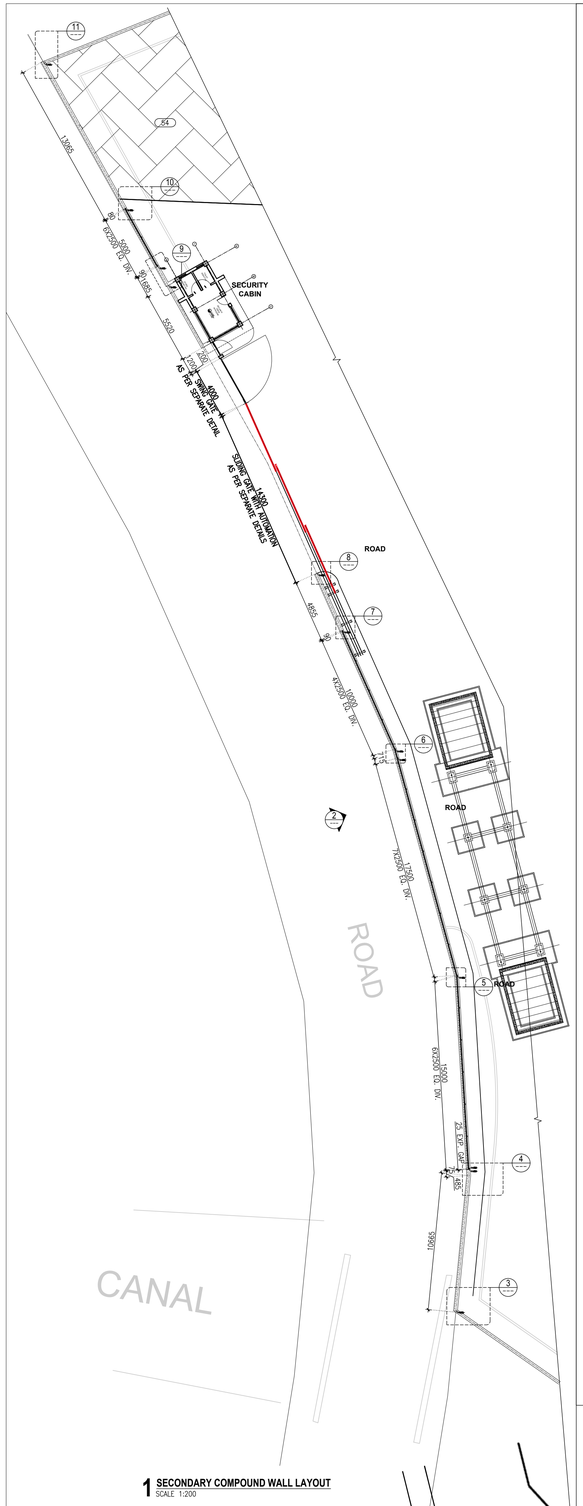



1 SECONDARY COMPOUND WALL LAYOUT
SCALE 1:200

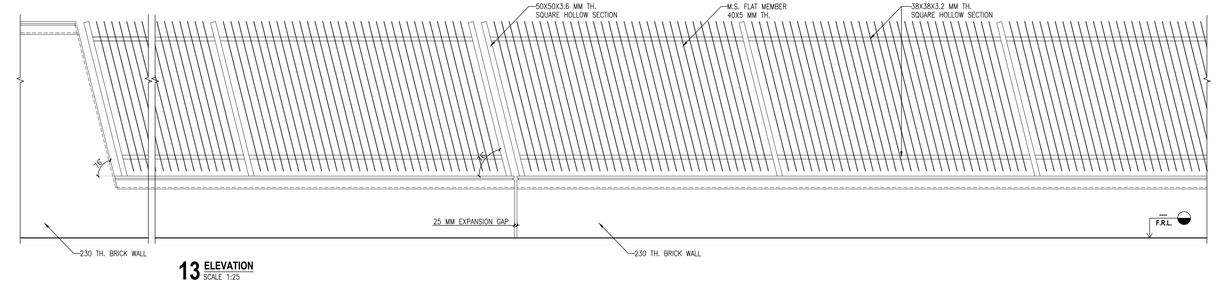


13 ELEVATION
SCALE 1:25

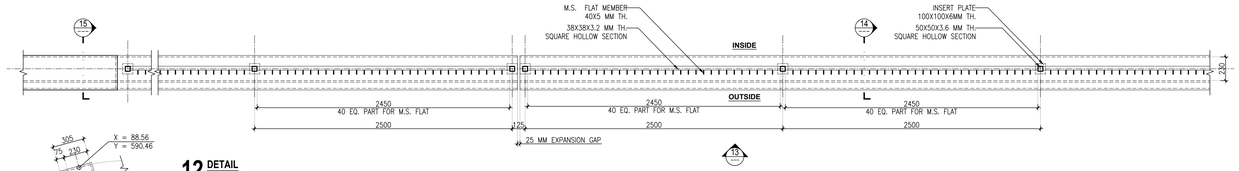

12 DETAIL
SCALE 1:25

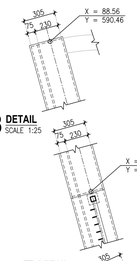

8 DETAIL
SCALE 1:25

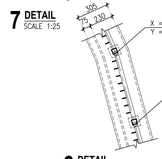


7 DETAIL
SCALE 1:25

6 DETAIL
SCALE 1:25

5 DETAIL
SCALE 1:25

4 DETAIL
SCALE 1:25


3 DETAIL
SCALE 1:25

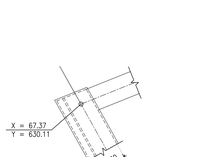


11 DETAIL
SCALE 1:25

10 DETAIL
SCALE 1:25


9 DETAIL
SCALE 1:25

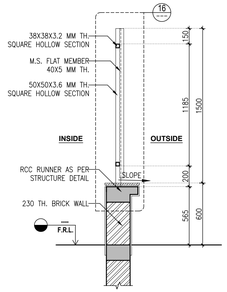


14 SECTION
SCALE 1:25

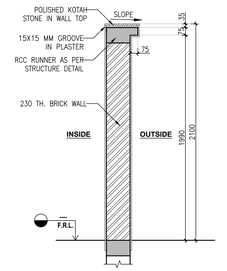


15 SECTION
SCALE 1:25

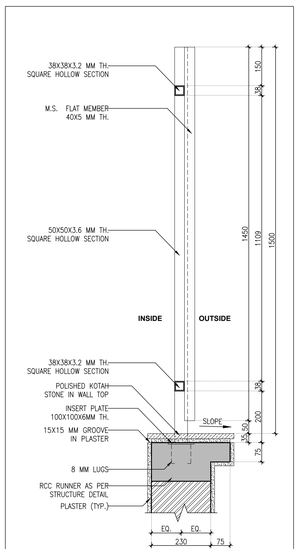

16 DETAIL
SCALE 1:10

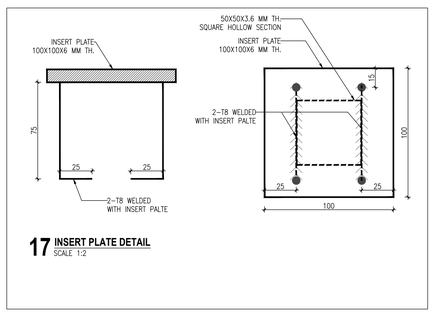

17 INSERT PLATE DETAIL
SCALE 1:2

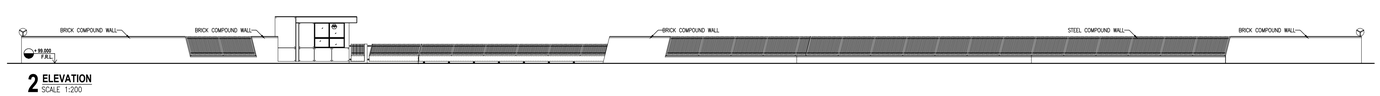

2 ELEVATION
SCALE 1:200

THIS DRAWING & DESIGN IS THE SOLE PROPERTY OF VMS & SHALL NOT BE COPIED, TRACED OR REPRODUCED BY ANY MEANS WITHOUT PRIOR WRITTEN CONSENT OF THE FIRM.

GENERAL NOTES :

1. ALL THE DIMENSIONS ARE UNFINISHED DIMENSIONS.
2. ALL DIMENSIONS ARE IN MM AND LEVELS ARE IN MT, UNLESS OTHERWISE MENTIONED.
3. ALL THE DIMENSIONS SHALL BE READ & NOT TO BE MEASURED.
4. IN CASE OF ANY DISCREPANCY, BRING IT TO THE NOTICE OF THE ARCHITECT IMMEDIATELY.
5. DETAIL DRAWING PRECEDES THE GENERAL DRAWING

IMPORTANT NOTE :

1. REFER DRAWING C.E.101, C.R.101 FOR F.G.L & F.R.L.
2. SLIDING & SWING GATE WITH AUTOMATION AS PER VENDORS DETAILED SHOP DRAWING APPROVED BY VMS

STANDARD DRAWING SYMBOLS:

+ FINISHED LEVEL
+ UNFINISHED LEVEL

SECTION SYMBOL
UPPER HALF INDICATES DIAGRAM NO. (NUMERICAL VALUE) IN DRAWING SHEET & LOWER HALF INDICATES DRAWING NO.

ELEVATION SYMBOL
UPPER HALF INDICATES DIAGRAM NO. IN DRAWING SHEET & LOWER HALF INDICATES DRAWING NO.

WINDOW SYMBOL
UPPER HALF INDICATES WINDOW NO. & LOWER HALF INDICATES DRAWING NO.

DOOR SYMBOL
UPPER HALF INDICATES DOOR NO. & LOWER HALF INDICATES DRAWING NO.

GRAPHIC LEGEND :

MASONRY CUT IN PLAN/SECTION.


RCC COLUMN CUT IN PLAN.

FOR CONSTRUCTION

NO.	DATE	DESCRIPTION	DRAWN BY	CHECKED BY
R1	10-12-2021	GENERALLY REVISED	ANAND	DARSH

REVISION HISTORY

KEY PLAN
SCALE : N.T.S.

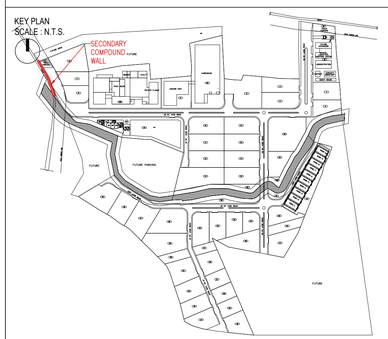

REFERENCE DRAWINGS :

01. ARCHITECTURAL :	-
02. STRUCTURAL :	-
03. HVAC :	-
04. ELECTRICAL :	-
05. UTILITIES :	-

SECONDARY COMPOUND WALL & DETAILS

PMC
Technopak Advisors Pvt. Ltd.
Gurgaon.

fanidhar
MEGA FOOD PARK - AT MUDARDA, MEHSANA
khet se bazaar tak...

PROJECT NO.	SCALE :	DRAWN :	ANAND
2017	AS NOTED	CHECKED:	DARSH
	DATE : 01-10-2020	APPROVED:	KINJAL
		COORDINATION CHECKED:	NITESH

VMS ENGINEERING & DESIGN SERVICES (P) LTD.
CHITRAKOOT FLATS, BEHIND TIMES OF INDIA, OFF ASHRAM ROAD,
AHMEDABAD-380 009. PHONE: +91 (079) 2658-8829/4488, 40236236
FAX : +91 (079) 2658 5596 WWW.VMSCONSULTANTS.COM

SHEET SIZE	DRAWING NO.	CONSTRUCTION	REVISION:
600x 1000	A.G.105	C	R1