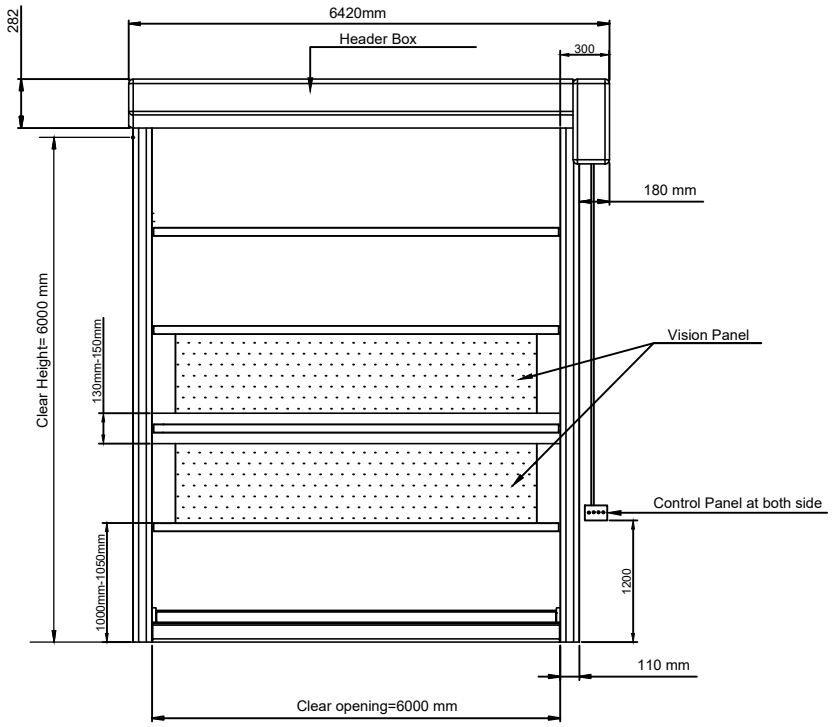
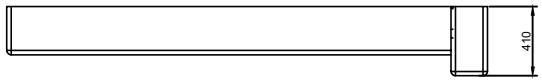
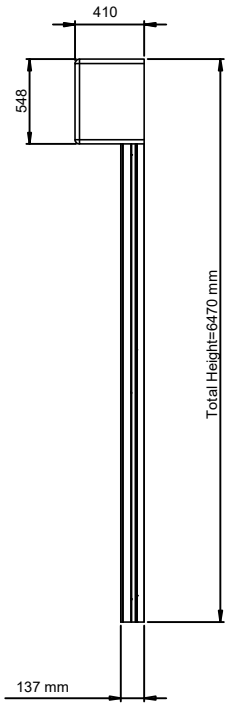



Note:--

1) All Dimension are in MM
2) Opening speed will be 0.5-1.5m/s
3) 1.5kw motor will be used
4) All curtain are closed vinyl(pvc)
5) Segment height can be change from the bars 50 to 100mm
6) RAL shade = RAL 9002

TOLERANCE - ±10mm

| Clear Width | Clear Height | QTY |
|---|---|---|
| 6000 MM | 6000 MM | 1NO |

| Rev No. | Revision | Date | Revised By |
|---|---|---|---|
| 1. | Total height of the door has been changed from 6020mm to 6470mm +150mm installation space | 24/08/2022 | Sujata |
| 2. | Vision panel, control panel,Segment height tolerance has been added. | 10/11/2022 | Sujata |
| 3. | Door qty has been changed | 18/01/2023 | Sujata |
| 4. | RAL shade added. | 20/03/2023 | Nirmala |

This drawing & design is the property of NIHVA TECHNOLOGIES. Not to be sold or copied to any other concern.

TITLE:- HIGH SPEED DOOR

NIHVA TECHNOLOGIES PVT. LTD.

NIHVA TECHNOLOGIES PVT. LTD. PUNE
Tel : 020 66304033
Email:- info@nihva.com
Website:- www.nihva.com

| | NAME | DATE | SIGN |
|---|---|---|---|
| DRAWN | SUJATA.B | 09/08/2022 | |
| CHECK | | | |
| APPRD. | AMIT.K | 09/08/2022 | |

If any queries contact : design@nihva.com

ALL DIMENSION ARE IN mm

CLIENT - RONAK BUILD.

LOCATION -Pune

PRODUCT - HSD

DWG NO:-NIHVA/21-22/CLT/0104_1 | REV- 03

SCALE: NTS | SCALE:-- 1:1 | SHEET: 01 OF 01