


TOP VIEW

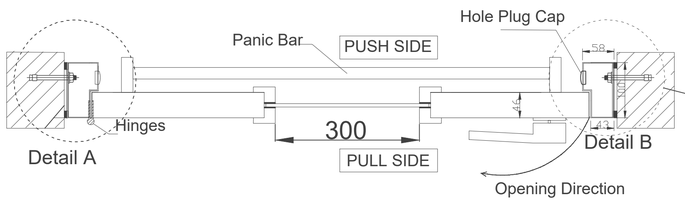


SECTION 'X'-'X'

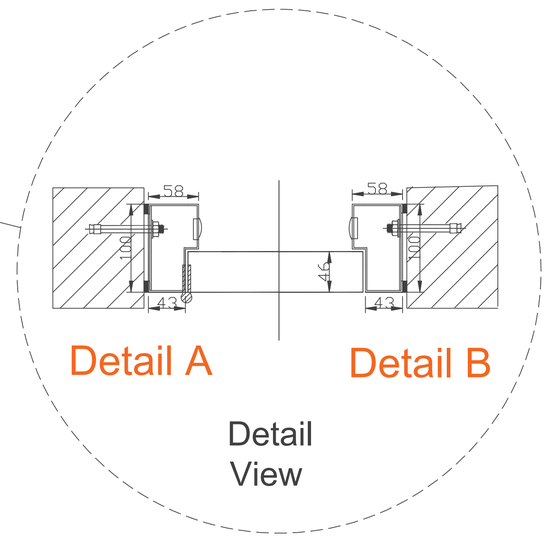

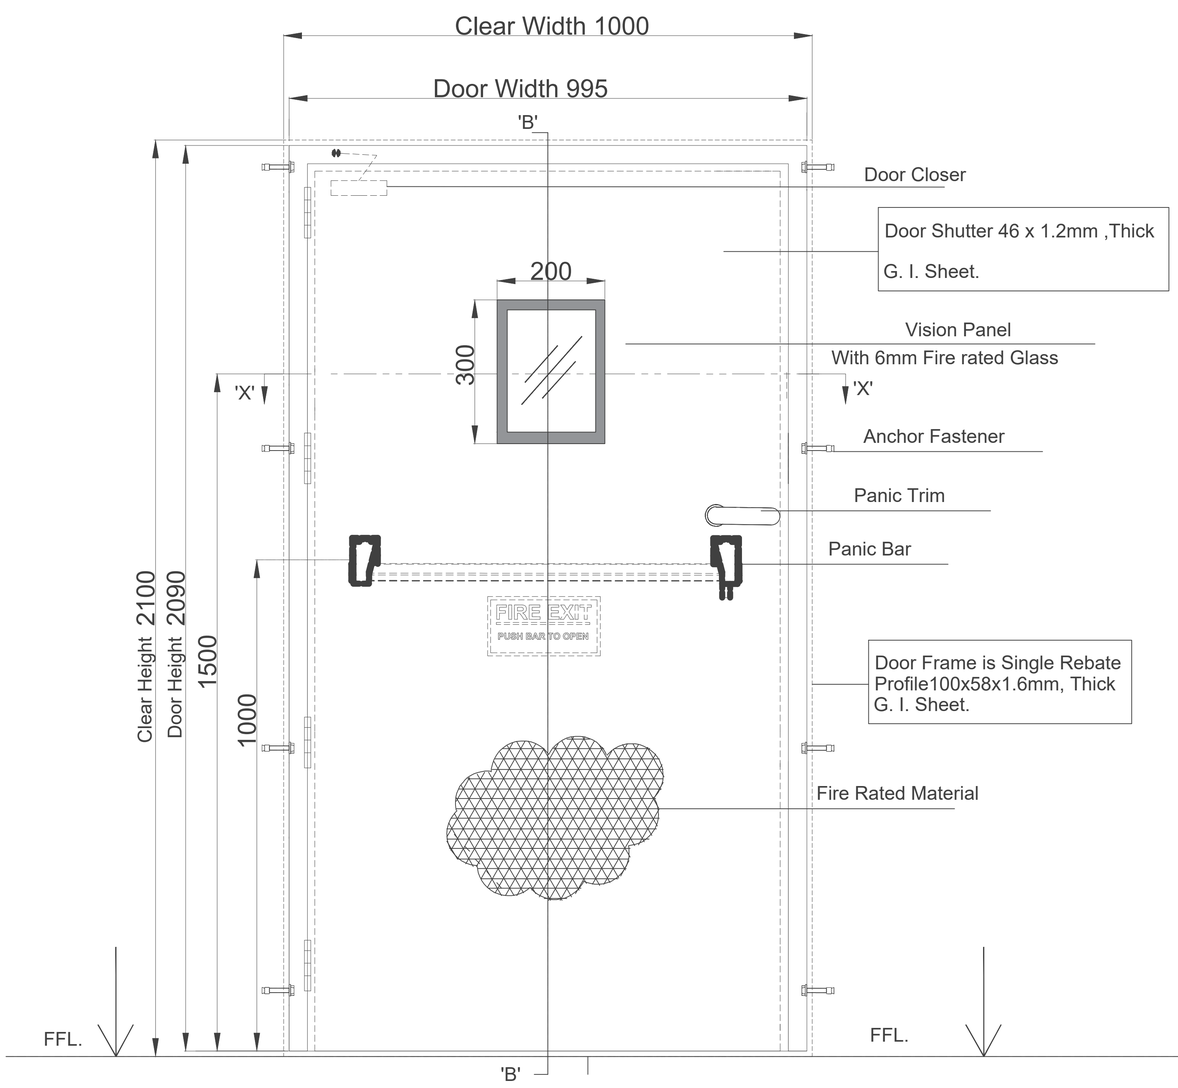

ELEVATION

SIDE VIEW

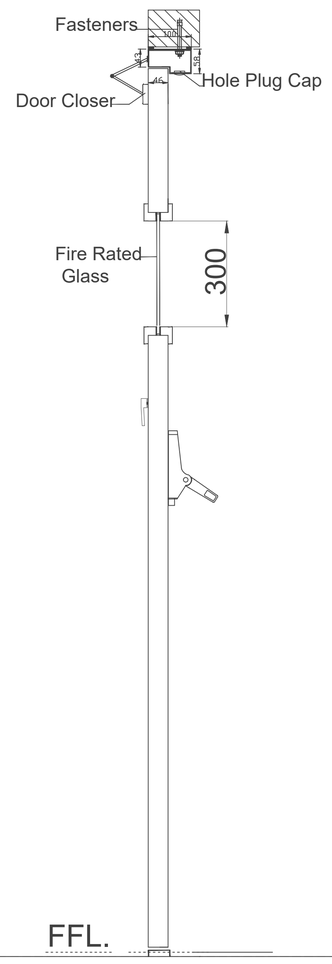

SECTION B-B

TECHNICAL SPECIFICATION :

Sr.	DESCRIPTION & DETAILS
01	Door frame - 100X58 mm x1.6mm thick G.I. Sheet
02	Door Shutter - 46 mm x1.2mm thick G.I. Sheet
03	SS Ball Bearing Hinges 4"x3"x3mm
04	Single Leaf Panic Bar
05	External Panic Trim
06	Anchor Fasteners (M10x100mm Dia)
07	Heavy Duty Door Closer (TS 1000)
08	Vision Window With 6mm Fire Rated Glass
09	Fire Rating - 120 Minutes

Note :-

1. All Dimension are in mm
2. This drawing is only for understanding purpose
3. RAL code confirm by client

SIZE:

Sr.	Clear Width	Clear Height	Qty
01	1000	2100	01

This Drawing & Design is the property of NIHVA TECHNOLOGIES. Not to be sold or copied to any other concern.

TITLE :- FIRE DOOR			NIHVA TECHNOLOGIES PVT. LTD. PUNE Tel : 020 66304033 Email : info@nihva.com Website : www.nihva.com	
NAME	DATE	SIGN		
B.S	10/03/2025		CLIENT -TATA MOTOR	
S.W	10/03/2025		LOCATION - CHINCHWAD,PUNE	
V.T	10/03/2025		PRODUCT - FIRE DOOR	QTY-01 Nos
If any queries contact : design2@nihva.com			DWG NO - NIHVA/24-25/00XX	REV- 0
All dimensions are in MM			SCALE : NTS	SHEET : 01 OF 01