Revision		Date	By
A	Corrected mullion hoist positions, floor pits altered	2022-09-02	EB

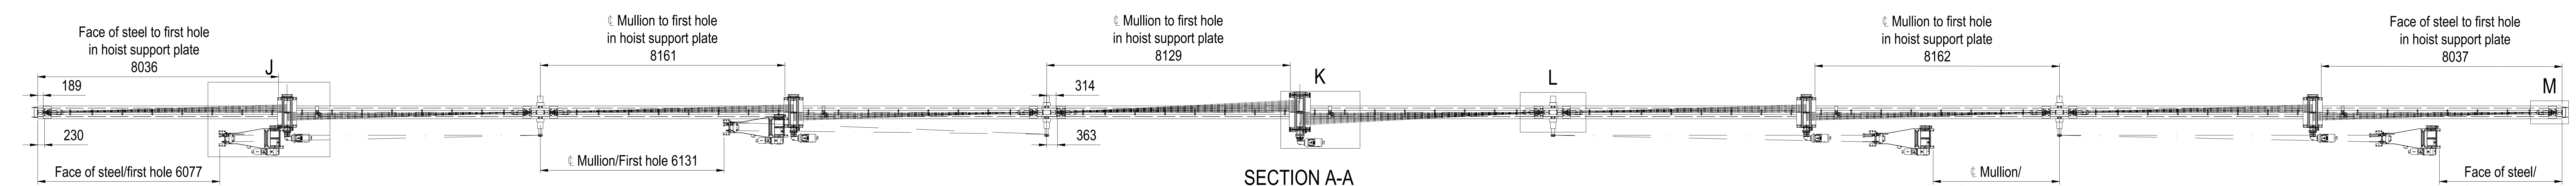

SECTION A-A

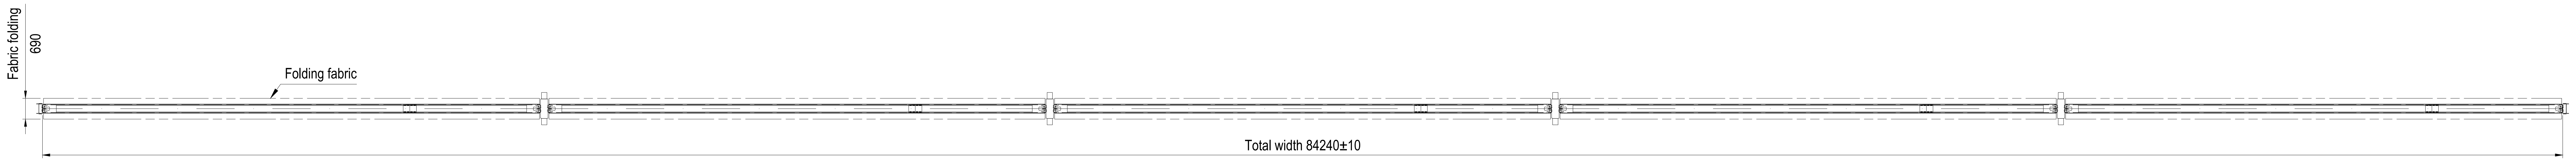

SECTION B-B

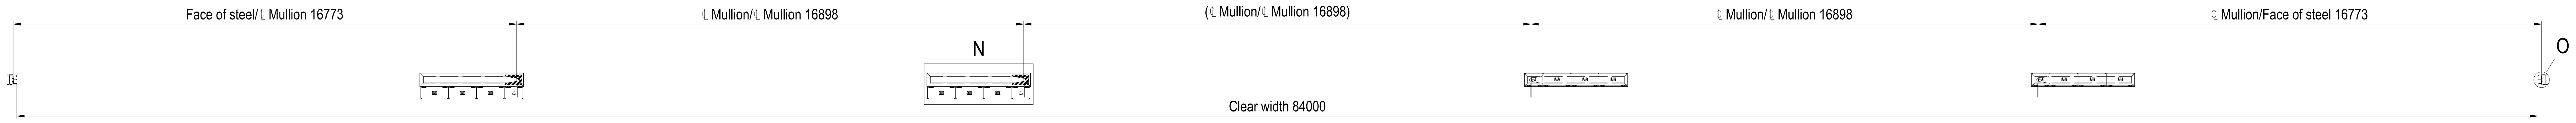
Face of steel/℄ Mullion 16773
℄ Mullion/℄ Mullion 16898
(℄ Mullion/℄ Mullion 16898)
℄ Mullion/℄ Mullion 16898
℄ Mullion/Face of steel 16773
N
O
Clear width 84000

SECTION C-C

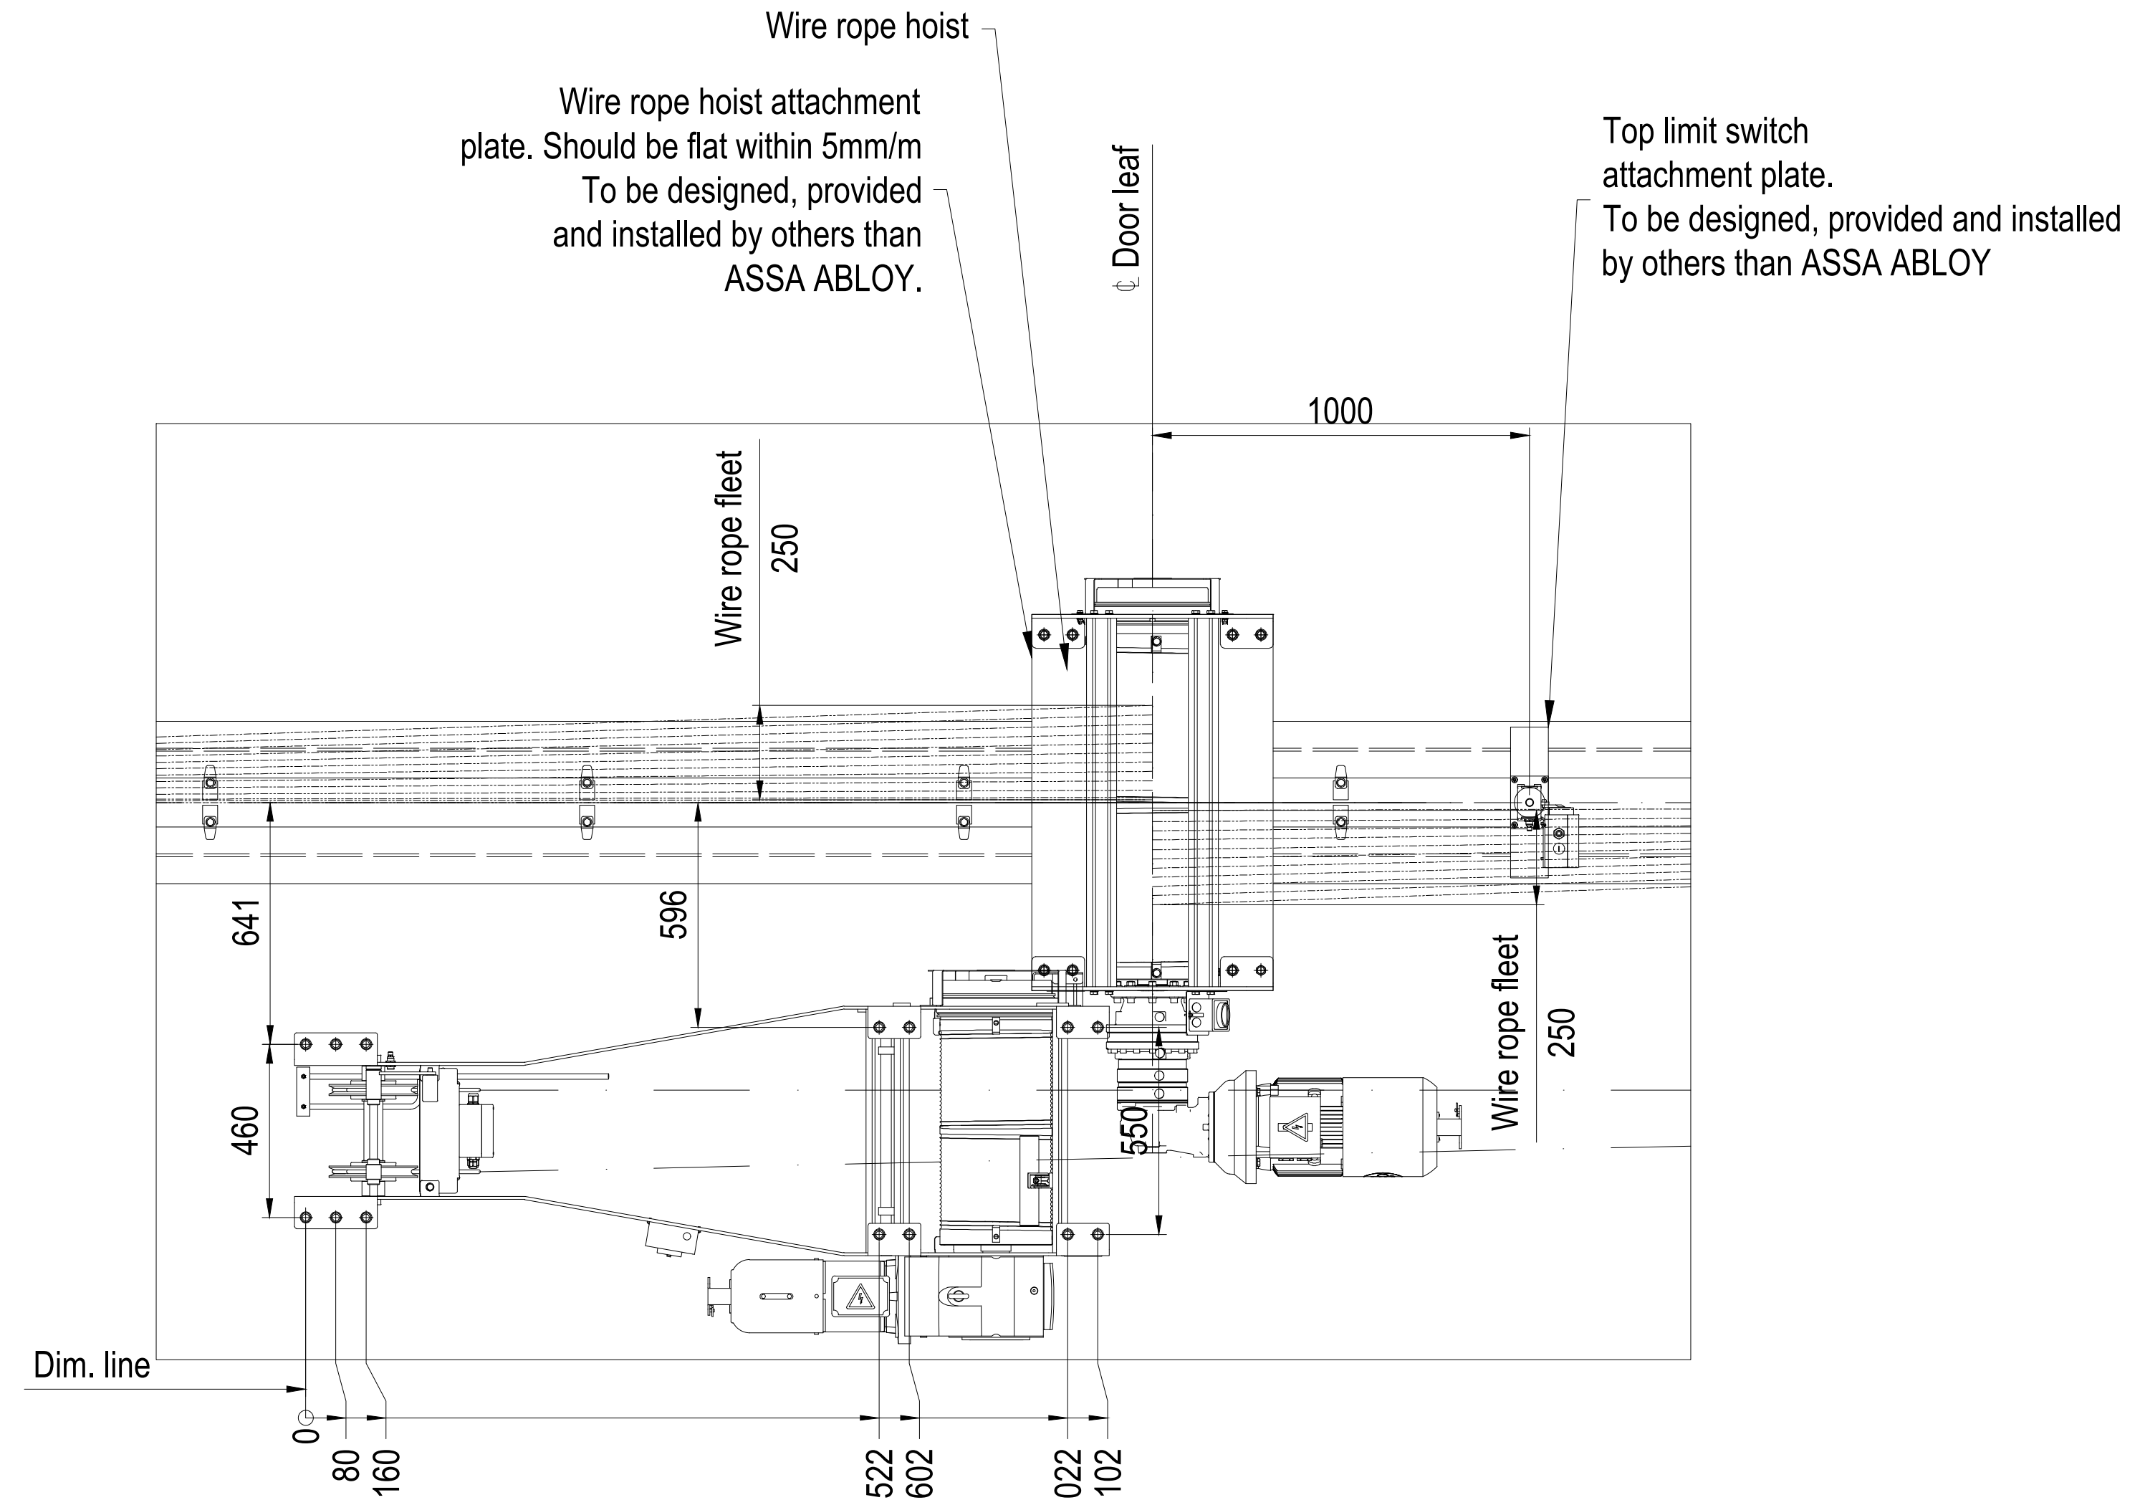

DETAIL J, SCALE (1:20)

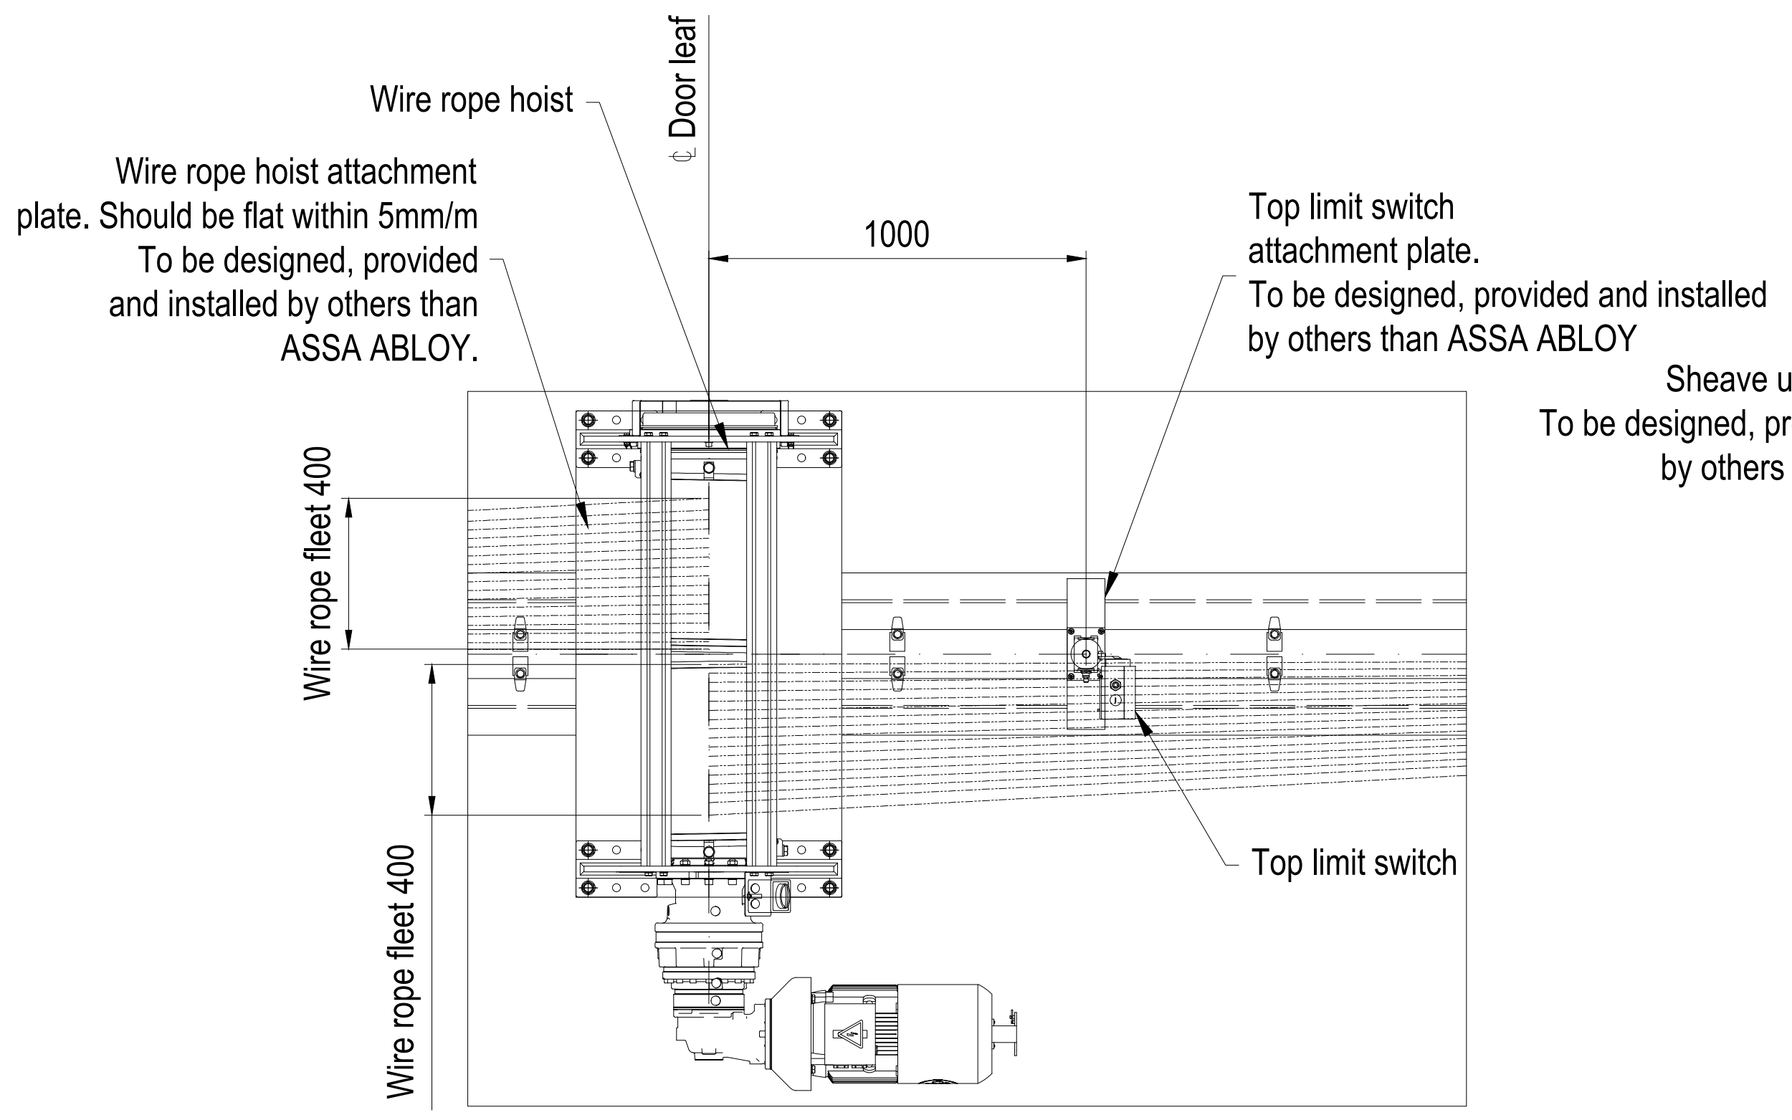

DETAIL K, SCALE (1:20)

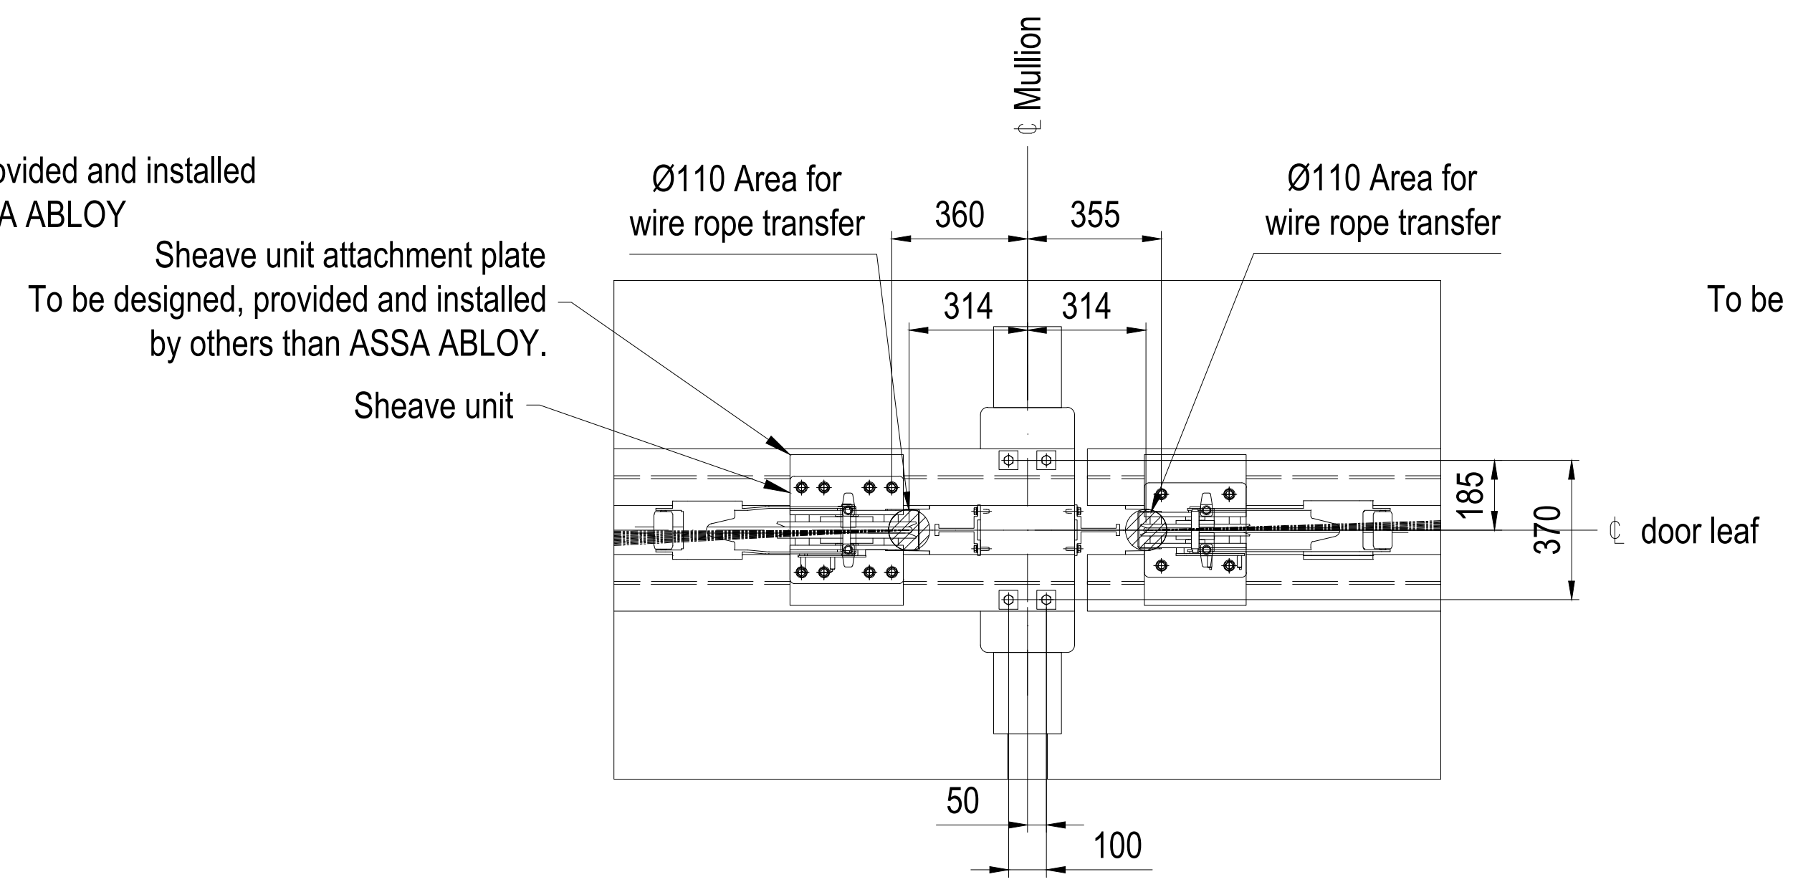

DETAIL L, SCALE (1:20)

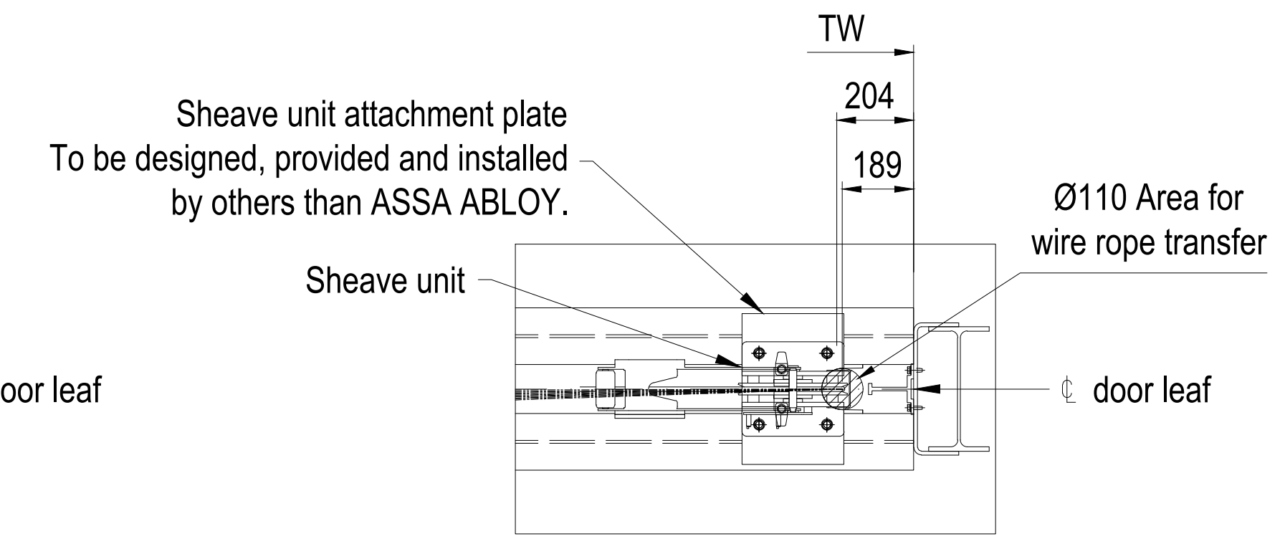
TW
204
189
Sheave unit attachment plate
To be designed, provided and installed
by others than ASSA ABLOY.
Ø110 Area for
wire rope transfer
Sheave unit
℄ door leaf

DETAIL M, SCALE (1:20)

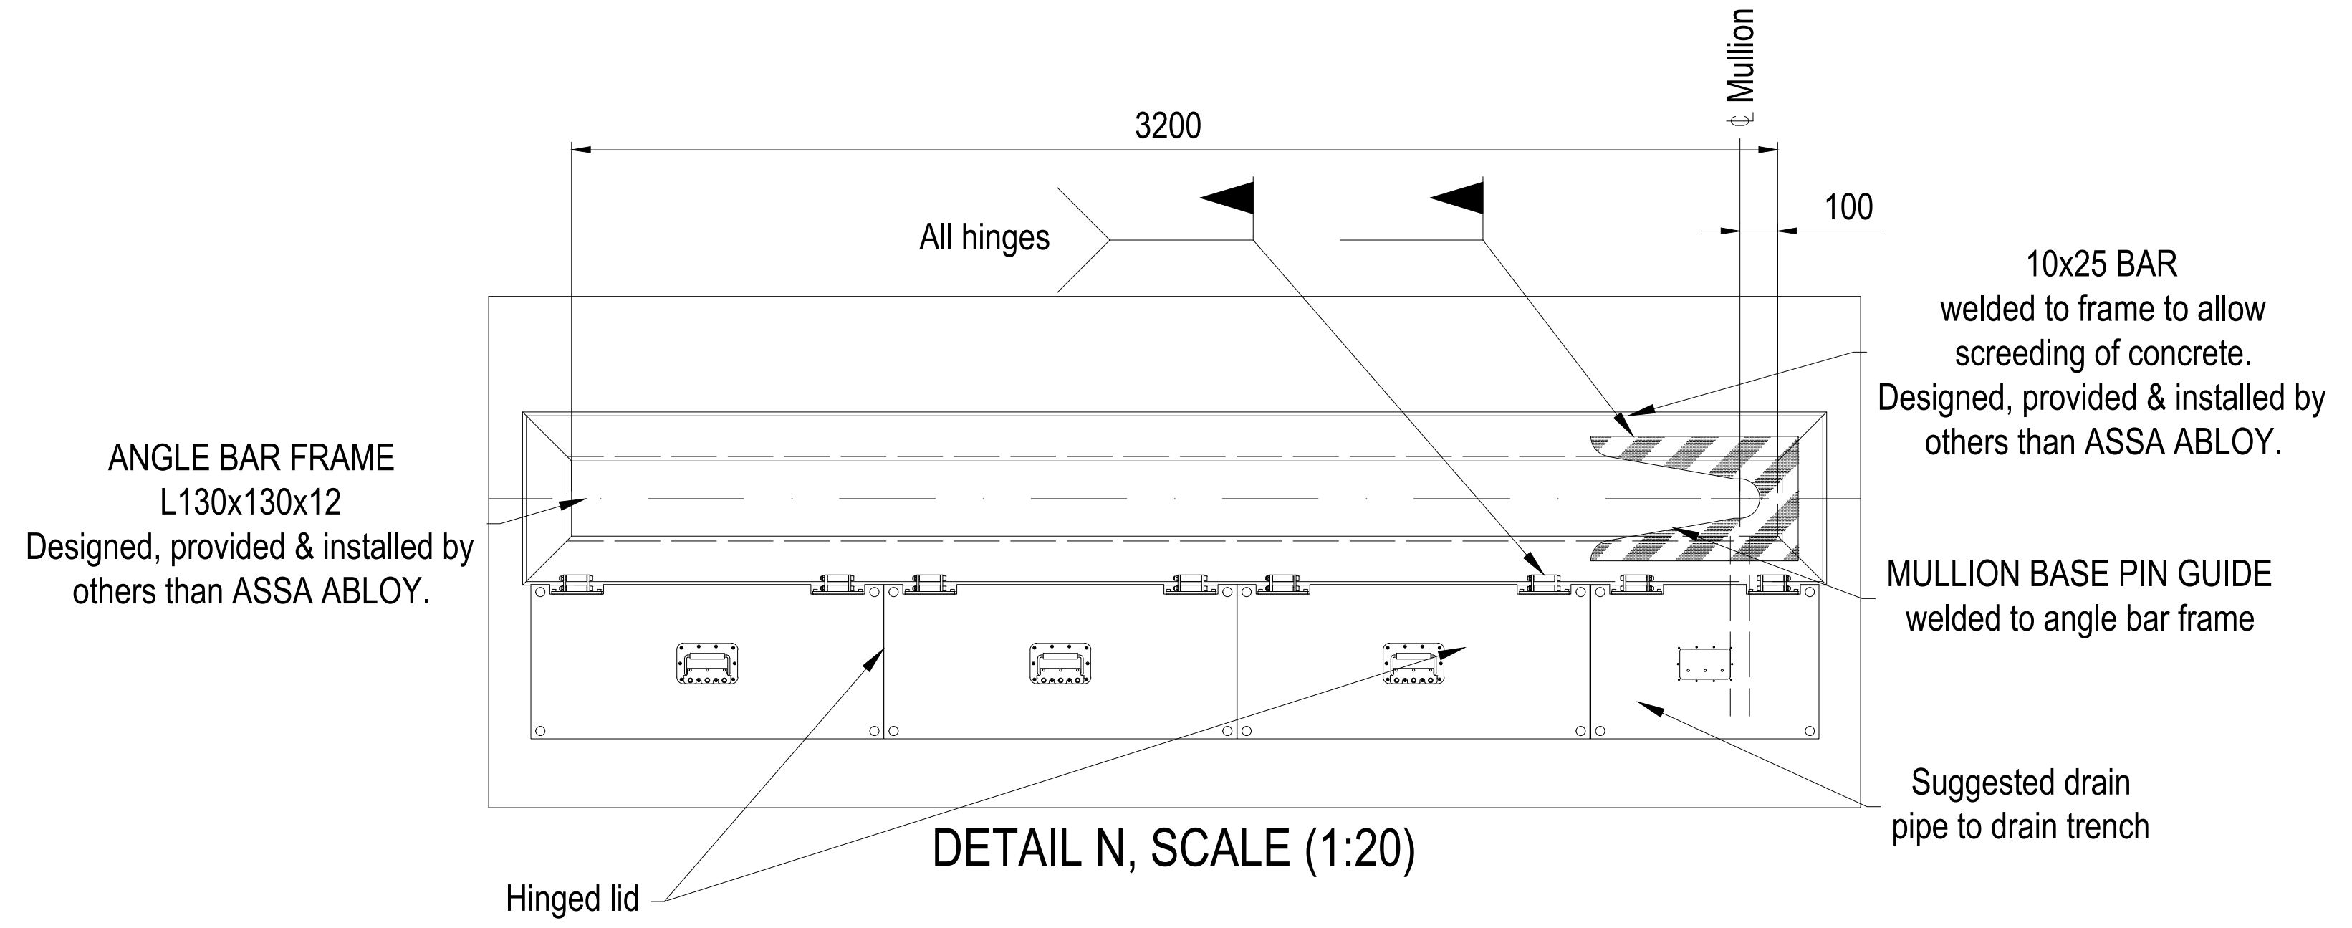

DETAIL N, SCALE (1:20)

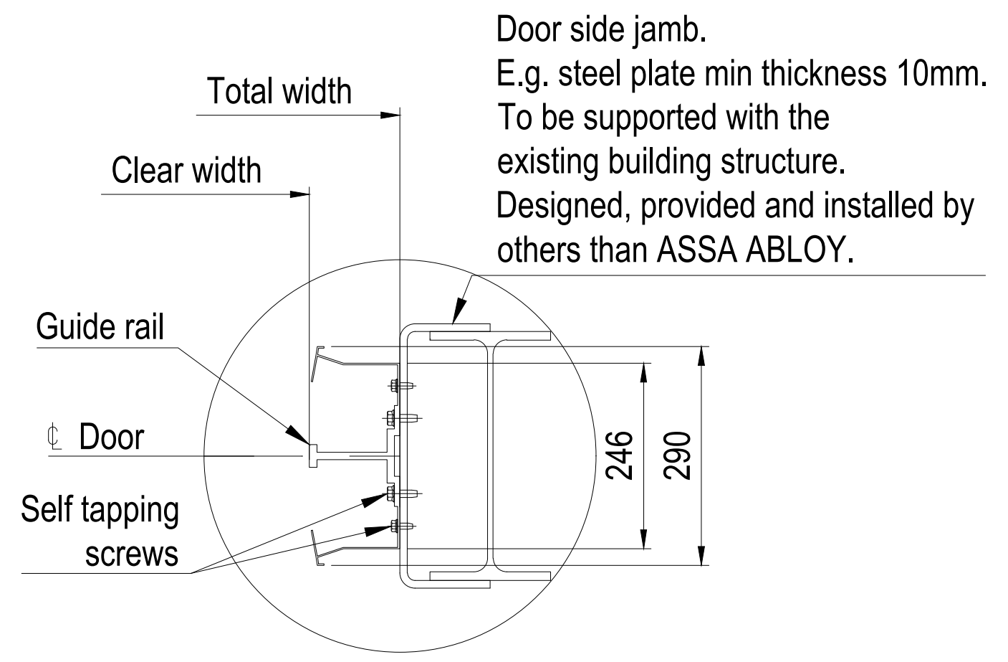

DETAIL O, SCALE (1:10)

DOOR IDENTITY NUMBER: 84800001

LOAD DIAGRAM & NOTES, ref. to drwng. no. 77446

INTERFACE, SECTIONS ref. to drwng. no. 77445

INTERFACE, ELEVATION ref. to drwng. no. 77443

DESIGNED	SIZE	SCALE
EB	A1F	1:100

CODE
84800
ITEM NO

DATE
2022-08-23

ASSA ABLOY

If not otherwise stated:
Tolerances
ISO 2768-m
EN ISO 13920-B
Cutting class
ISO 9013-442
Weld class
ISO 5817-C
Surface finish
Smooth raw surface

GMR Aero Technic Hangar1
India
Megadoor 84000x23000/14000
Interface, Plan views

PLOT DATE

DRAWING NO
77444

REVISION
A

This document is the property of ASSA ABLOY Entrance Systems AB and shall not without our written permission be copied, imparted to a third party or used for any other unauthorized purpose.