


NOTE:~ MTL : MS

BUSH Ø45 X 103L = 17 NOS

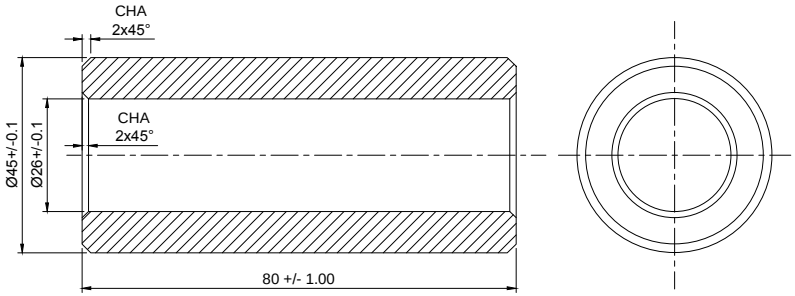

NOTE:~ MTL : MS

BUSH Ø45 X 80L = 8 NOS

NOTE : ~ WELD AT LIP

NOTE : ~ PLEASE MAINTAIN 8 MM GAP BETWEEN TWO LIP BUSHES.

This drawing & design is the property of NIHVA TECHNOLOGIES. Not to be sold or copied to any other concern.

TITLE

LIP MOUNTING BUSH

NIHVA TECHNOLOGIES PVT. LTD.

NIHVA TECHNOLOGIES PVT. LTD. PUNE
Tel : 020 66304033
Email:- info@nihva.com
Website:- www.nihva.com

	NAME	SIGN	DATE
DRAWN	P.A		12.12.18
CHECK	P.A		12.12.18
APPRD.	P.A		12.12.18

If any queries contact : design@nihva.com

ALL DIMENSION ARE IN mm

CLIENT -

PROJECT - DLAG1010

SITE LOCATION -

DWG. NO. :NIHVA/18-19/VDR/282

SCALE: NTS | WT: | REV- 0