
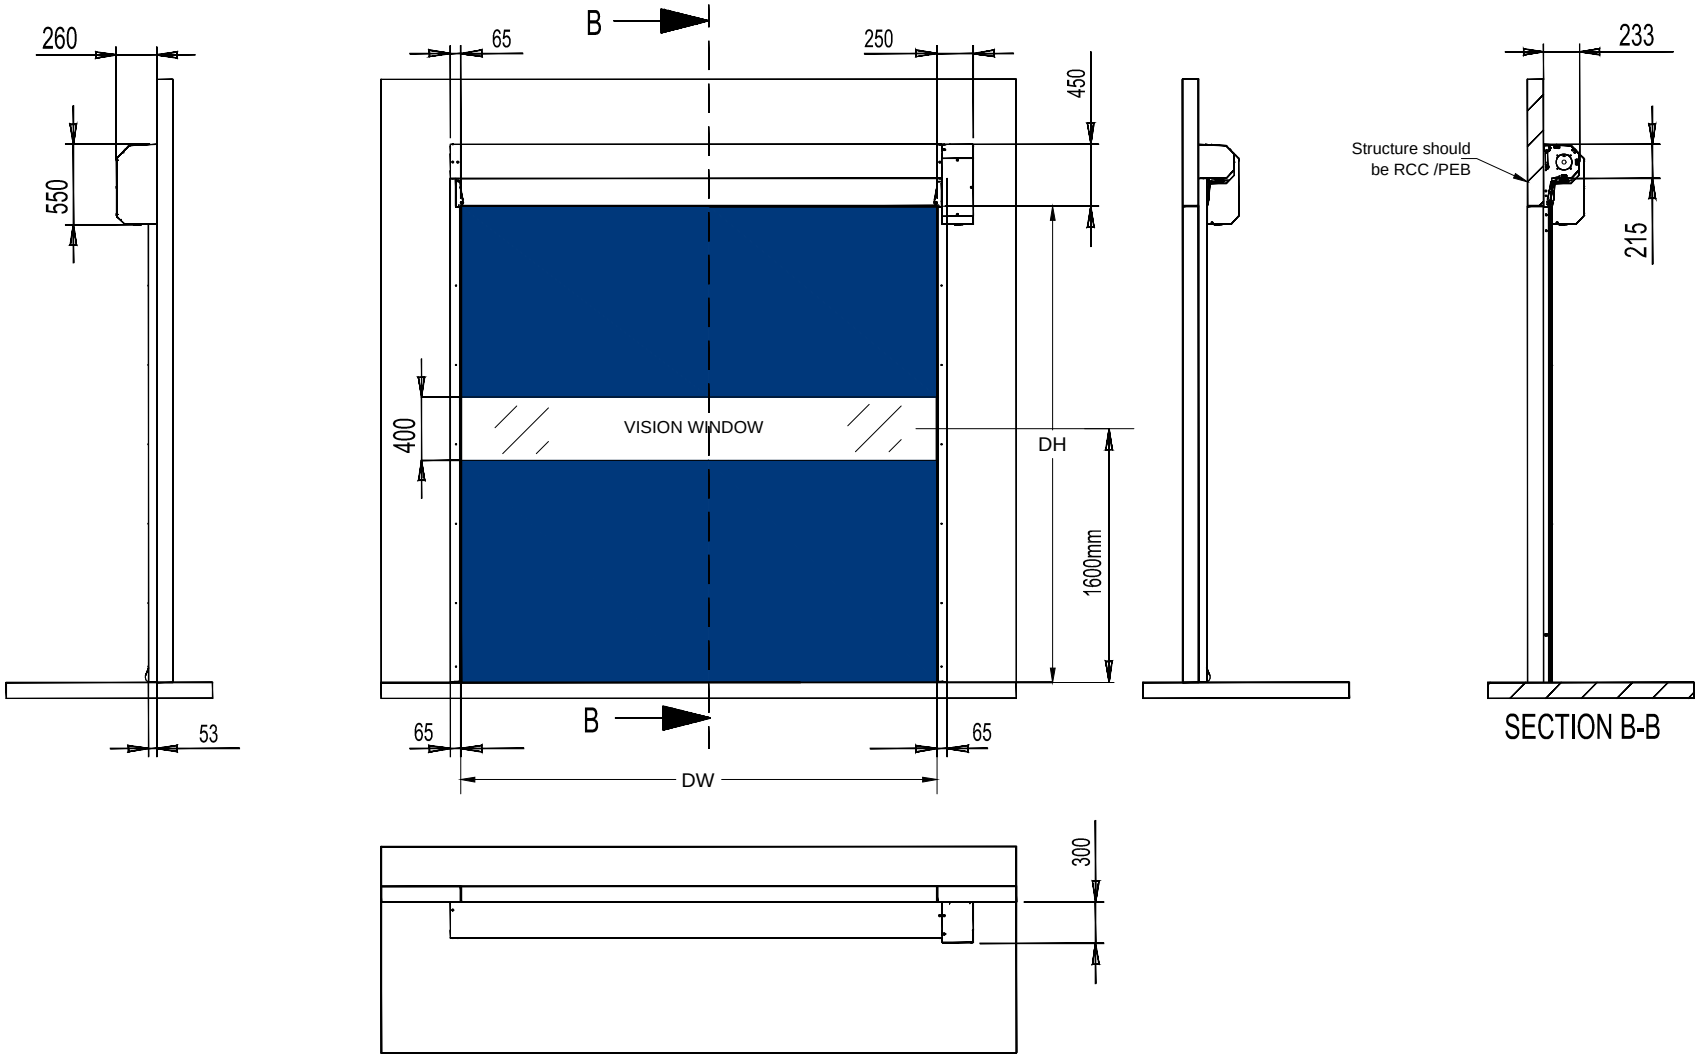


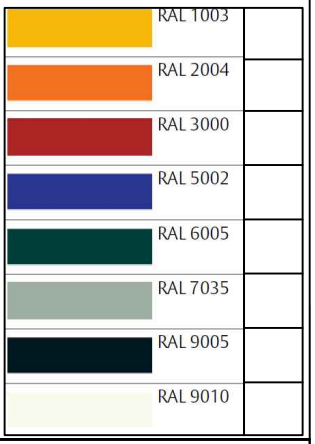

DOOR DIMENSION				
SR NO	DW	DH	MOTOR LOCATION	QUANTITY
1	1900	2280	RIGHT HAND SIDE	01

Note-
1. All Civil work will be in clients scope.
2. Client has to choose motor side (Right/left) according to the site conditions. Standard door comes with Right side Motor mounting.
3. All Construction in stainless steel AISI304

This drawing & designing is the property of NIHVA TECHNOLOGIES. Not to be sold or copied to any other concern.

TITLE: HIGH SPEED DOOR HS9020GHY.

NIHVA TECHNOLOGIES PVT. LTD.

NIHVA TECHNOLOGIES PVT. LTD. PUNE
Tel : 020 66304033
Email:- info@nihva.com
Website:- www.nihva.com

	NAME	SIGN	DATE
DRAWN	SURAJ		22/10/18
CHECK	PRADEEP		22/10/18
APPROVAL	R.D		22/10/18

CLIENT - EMCURE PHARMACEUTICALS PVT. LTD .
PROJECT - EMCURE PHARMACEUTICALS PVT. LTD .
SITE - Pune
If any queries contact : design@nihva.com
DWG. NO. : NIHVA/18-19/0159 REV- 0
ALL DIMENSION ARE IN mm
SCALE: NTS WT: SHEET: 01 OF 01