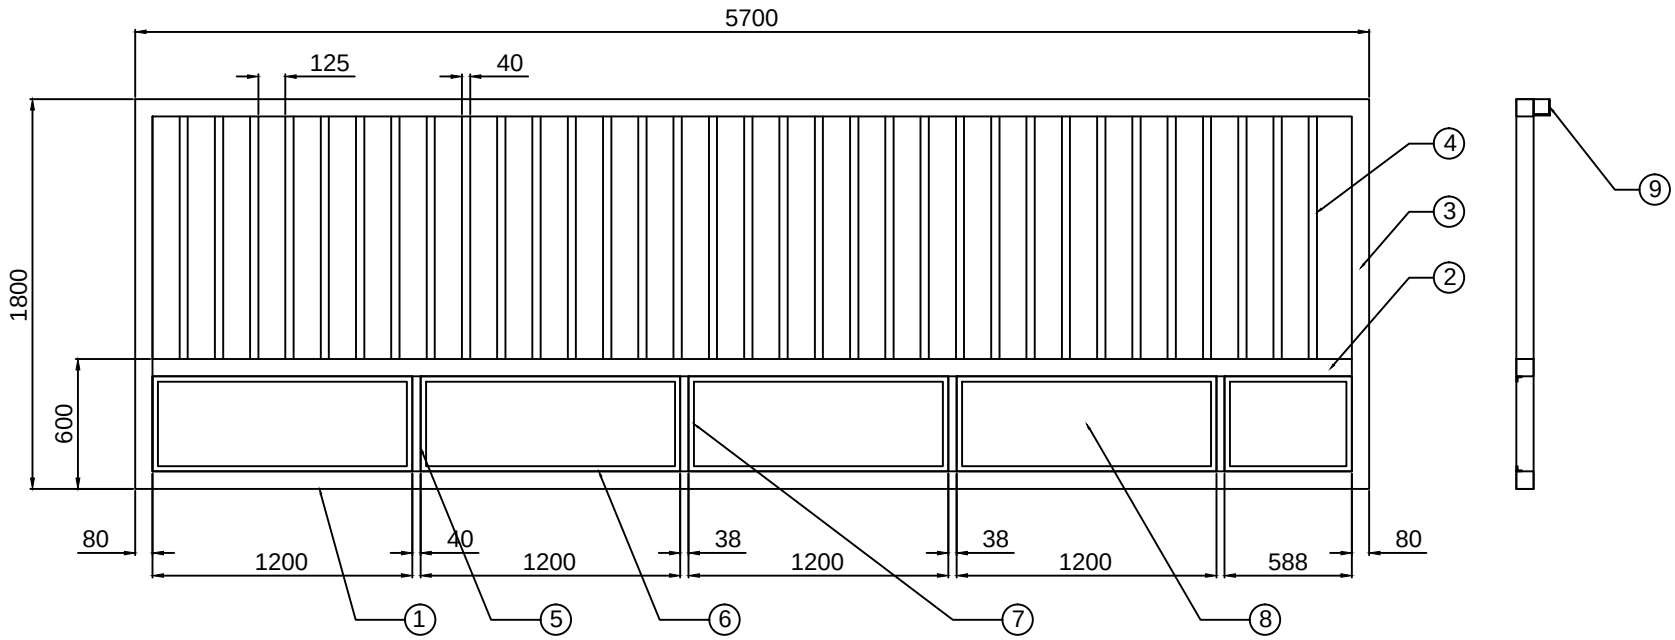

SR NO	DESCRIPTION	SPECIFICATION	QTY
9	ISA	75 X 6 X 5700L	1 NO
8	PERFORATED SHEET	430 X 1 X 1190	5 NOS
7	ISA	25 X 25 X 3 X 440L	10 NOS
6	ISA	25 X 25 X 3 X 1200L	10 NOS
5	SQ. TUBE	40 X 40 X 2.6 THK X 440L	4 NOS
4	SQ. TUBE	40 X 40 X 2.6 THK X 1120L	34 NOS
3	SQ. TUBE	80 X 80 X 3.2 THK X 1800L	2 NOS
2	SQ. TUBE	80 X 80 X 3.2 THK X 5540L	1 NO
1	SQ. TUBE	80 X 80 X 3.2 THK X 5700L	2 NOS

MASTER LEAF QTY = 2 NOS

This drawing & designing is the property of NIHVA TECHNOLOGIES. Not be sold or copy to any other concern.

TITLE: MASTER LEAF

	NAME	SIGN	DATE
DRAWN	P.V.A		05.10.2019
CHECK	G.J		05.10.2019
APPROVAL			

NIHVA TECHNOLOGIES PVT. LTD.
NIHVA TECHNOLOGY PVT. LTD. PUNE
Tel : 020 66304033
Email:- info@nihva.com
Website:- www.nihva.com

CLIENT -

PROJECT -

SITE LOCATION -

DWG. NO. : NIHVA/19-20/VDR/167 | REV: R00

If any queries contact : projects@nihva.com | SCALE: 01 | WT: | SHEET: 01 OF 01

ALL DIMENSION ARE IN mm