
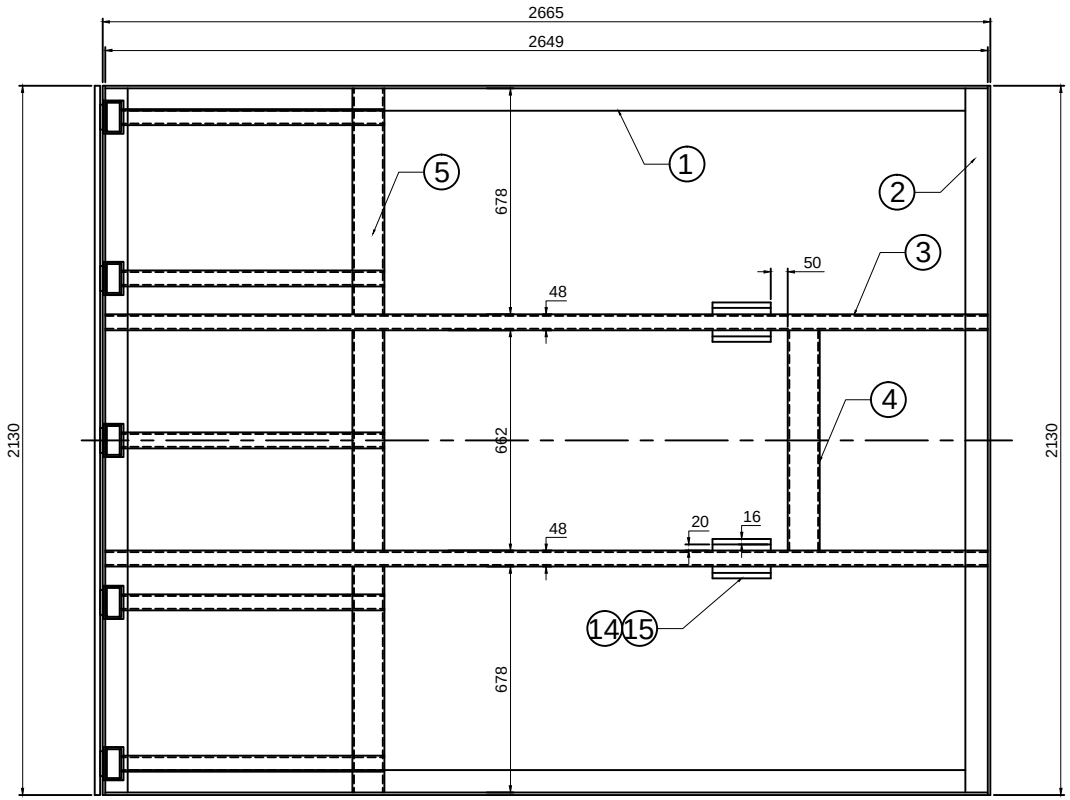


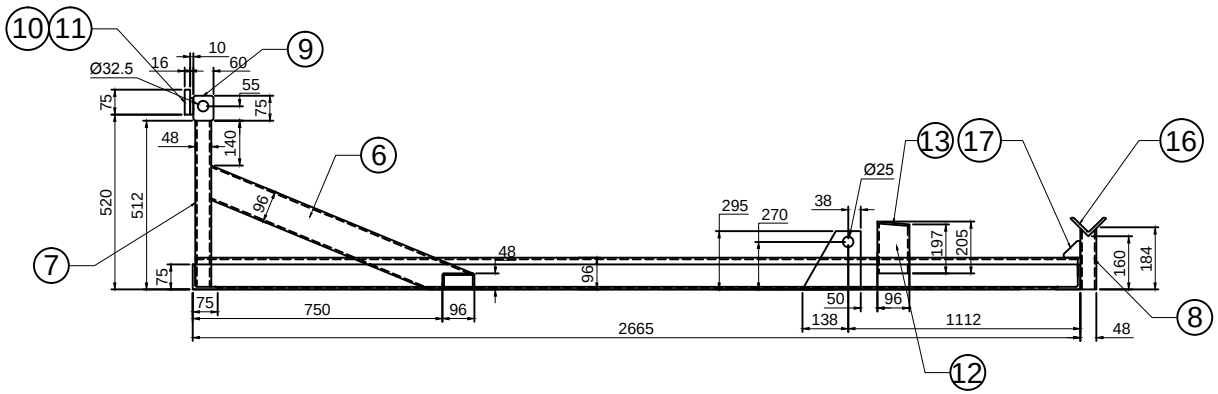

NOTE:~ MTL : MS

PART NO.	PART NAME	DESCRIPTION	QTY
1.	ISA	75 X 75 X 8 X 2650L (NOTCH)	2 NOS
2.	ISA	75 X 75 X 8 X 2130L	2 NOS
3.	R.TUBE	96 X 48 X 4.8 THK X 2650L	2 NOS
4.	R.TUBE	96 X 48 X 4.8 THK X 662L	2 NOS
5.	R.TUBE	96 X 48 X 4.8 THK X 678L	2 NOS
6.	R.TUBE	96 X 48 X 4.8 THK X 850L	5 NOS
7.	R.TUBE	96 X 48 X 4.8 THK X 510L	5 NOS
8.	R.TUBE	96 X 48 X 4.8 THK X 184L	2 NOS
9.	SOLID	75 X 60 X 100L	5 NOS
10.	FLAT	50 X 10 X 75L	5 NOS
11.	FLAT	75 X 16 X 2160L	2 NOS
12.	R.TUBE	96 X 48 X 4.8 THK X 200L	2 NOS
13.	FLAT	50 X 5 X 100L	2 NOS
14.	FLAT	100 X 20 X 150L	4 NOS
15.	PROFILE	295 X 16 X 300L	4 NOS
16.	ISA	75 X 8 X 75 X 120L	2 NOS
17.	PROFILE	50 X 10 X 50L	2 NOS

TITLE

BASE FRAME ASSLY

	NAME	SIGN	DATE
DRAWN	P.V.A		17.10.2019
CHECK	V.M.T		17.10.2019
APPRD.			

If any queries contact : design@nihva.com

ALL DIMENSION ARE IN mm

NIHVA

NIHVA TECHNOLOGIES PVT. LTD.

NIHVA TECHNOLOGIES PVT. LTD, PUNE
Tel : 020 66304033
Email:- info@nihva.com
Website:- www.nihva.com

CLIENT -

PROJECT -

SITE LOCATION -

DWG. NO. : NIHVA/19-20/VDR/174

SCALE: NTS | WT: | REV- 01